RECORD OF TITLE
UNDER LAND TRANSFER ACT 2017
FREEHOLD

Guaranteed Search Copy issued under Section 60 of the Land Transfer Act 2017

R.W. Muir
Registrar-General
of Land

Identifier	**451953**
Land Registration District	**Taranaki**
Date Issued	10 March 2009

Prior References
TNB3/970

Estate	Fee Simple
Area	338.5727 hectares more or less
Legal Description	Lot 2 Deposited Plan 413240

Registered Owners
Henry Raymond Matthews, Melody June Wallace and John Cain

Interests

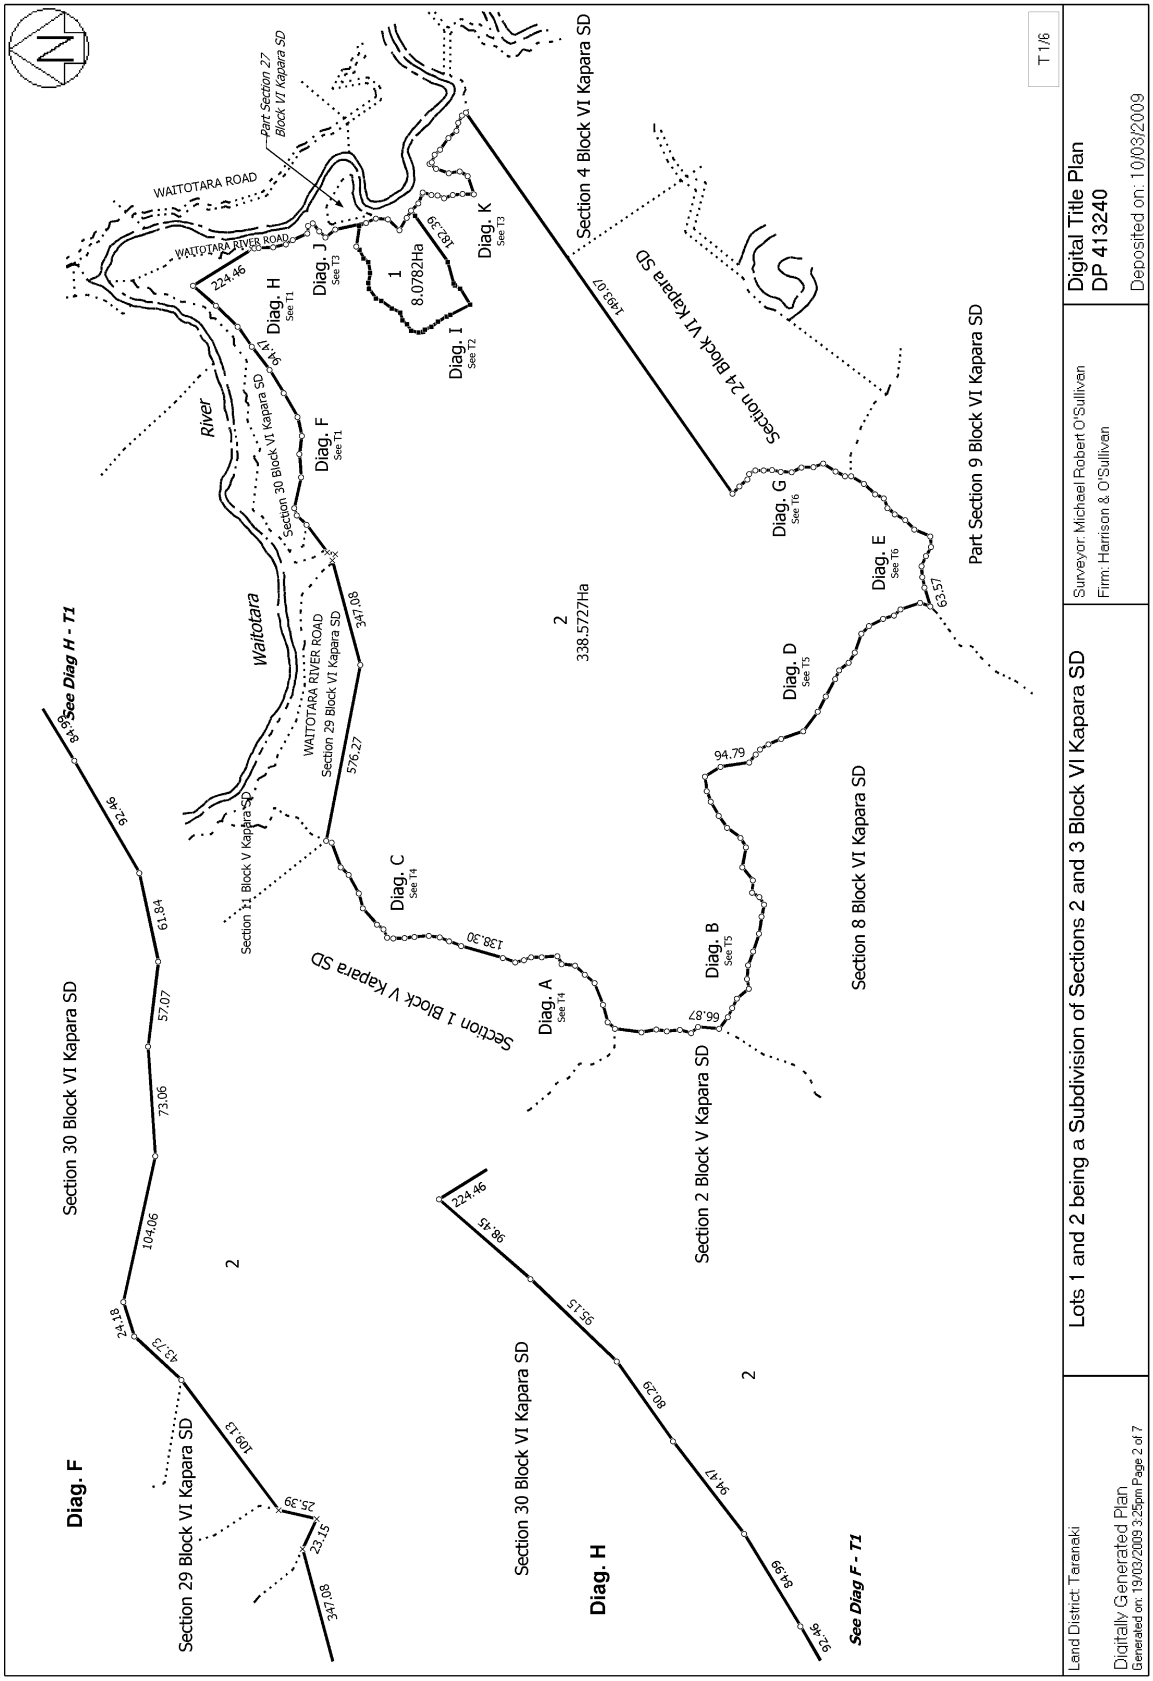
8772014.1 Notice pursuant to Section 195(2) Climate Change Response Act 2002 - 24.5.2011 at 7:00 am

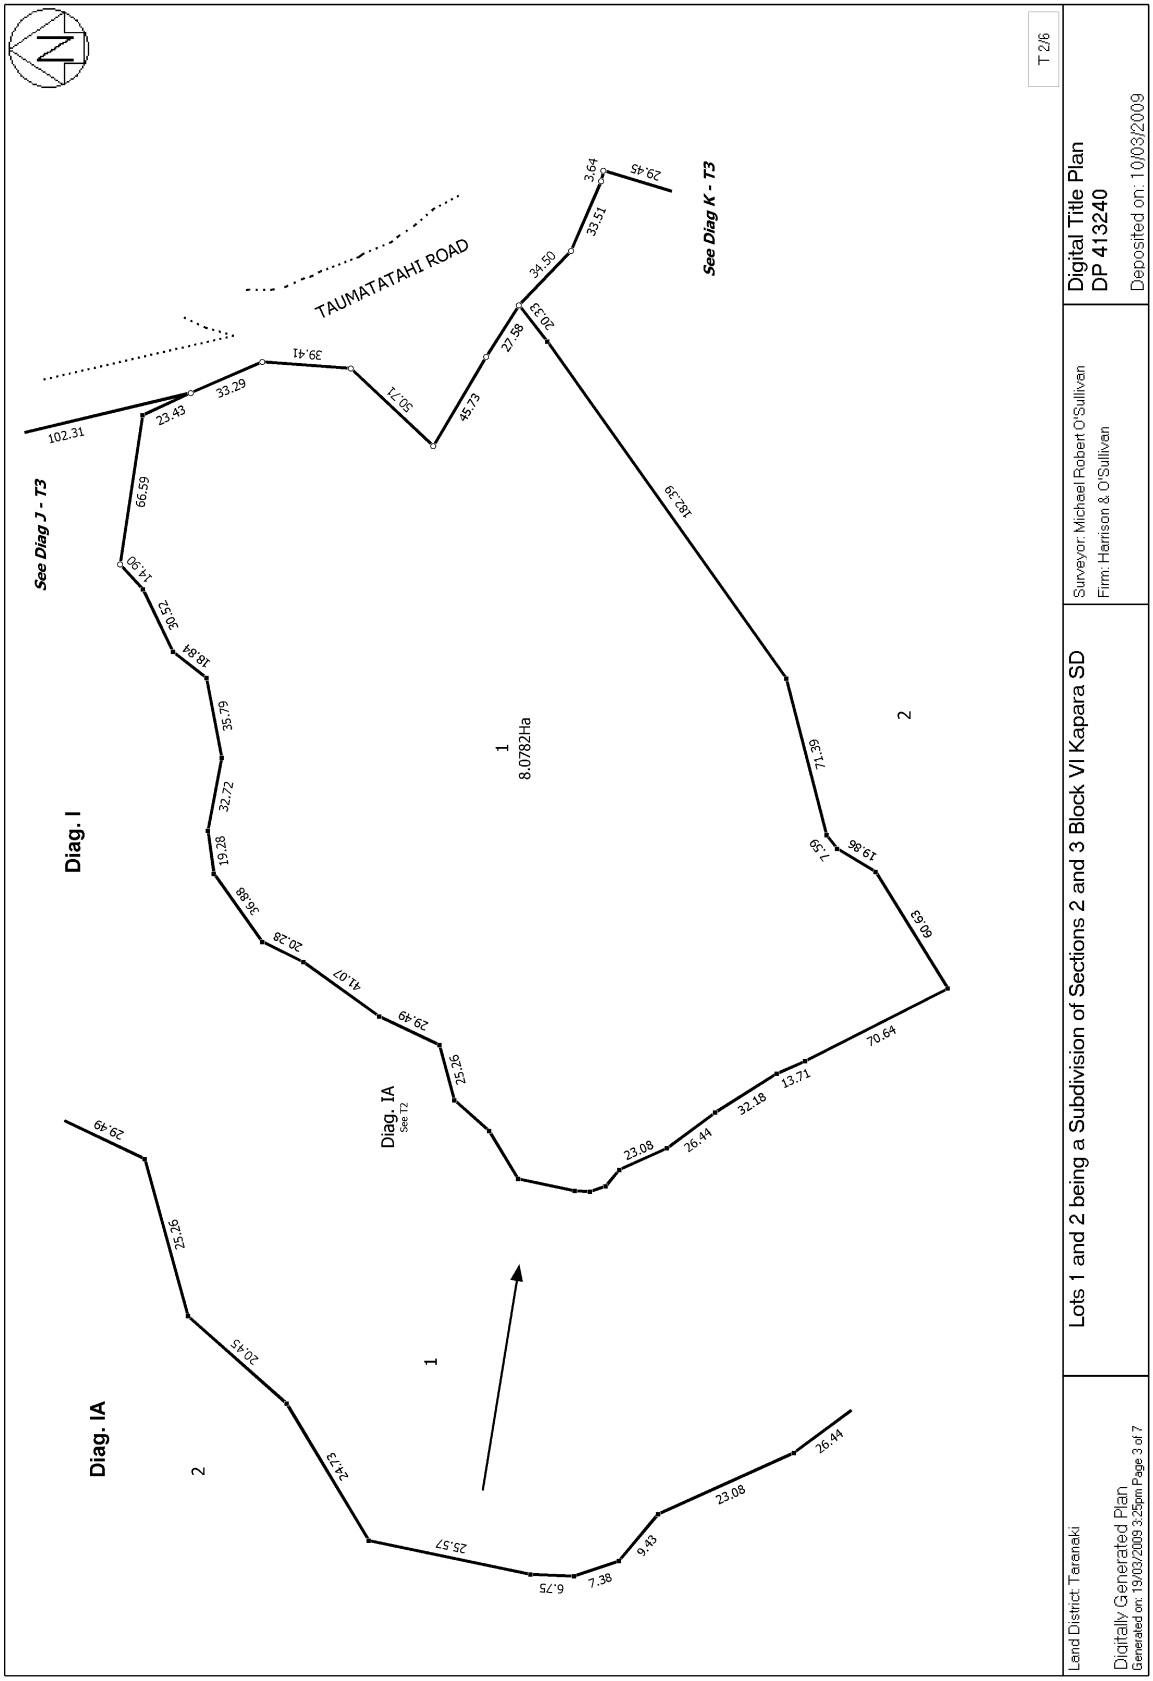
12717687.18 Forestry Right pursuant to the Forestry Rights Registration Act 1983 to Nirvana Farms Limited - 7.6.2023 at 2:45 pm

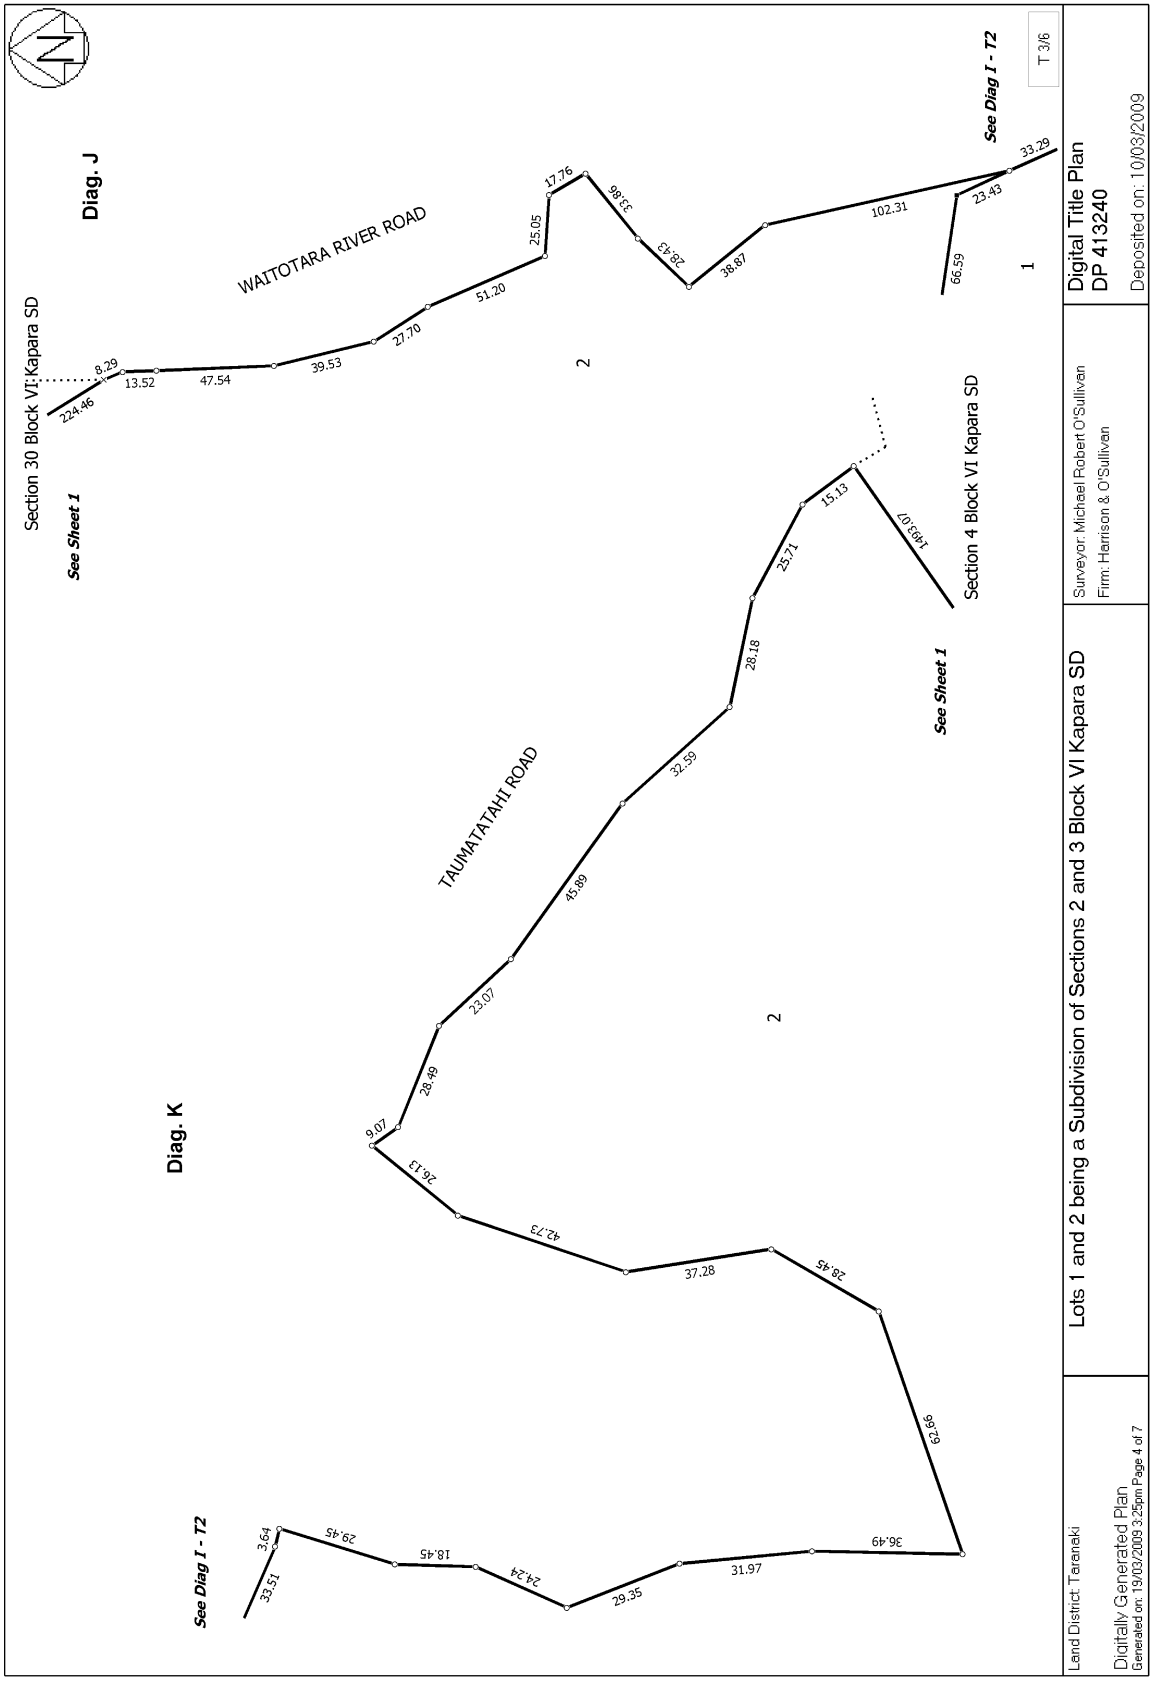
12717687.20 Mortgage to Vitol Asia PTE. Ltd. - 7.6.2023 at 2:45 pm

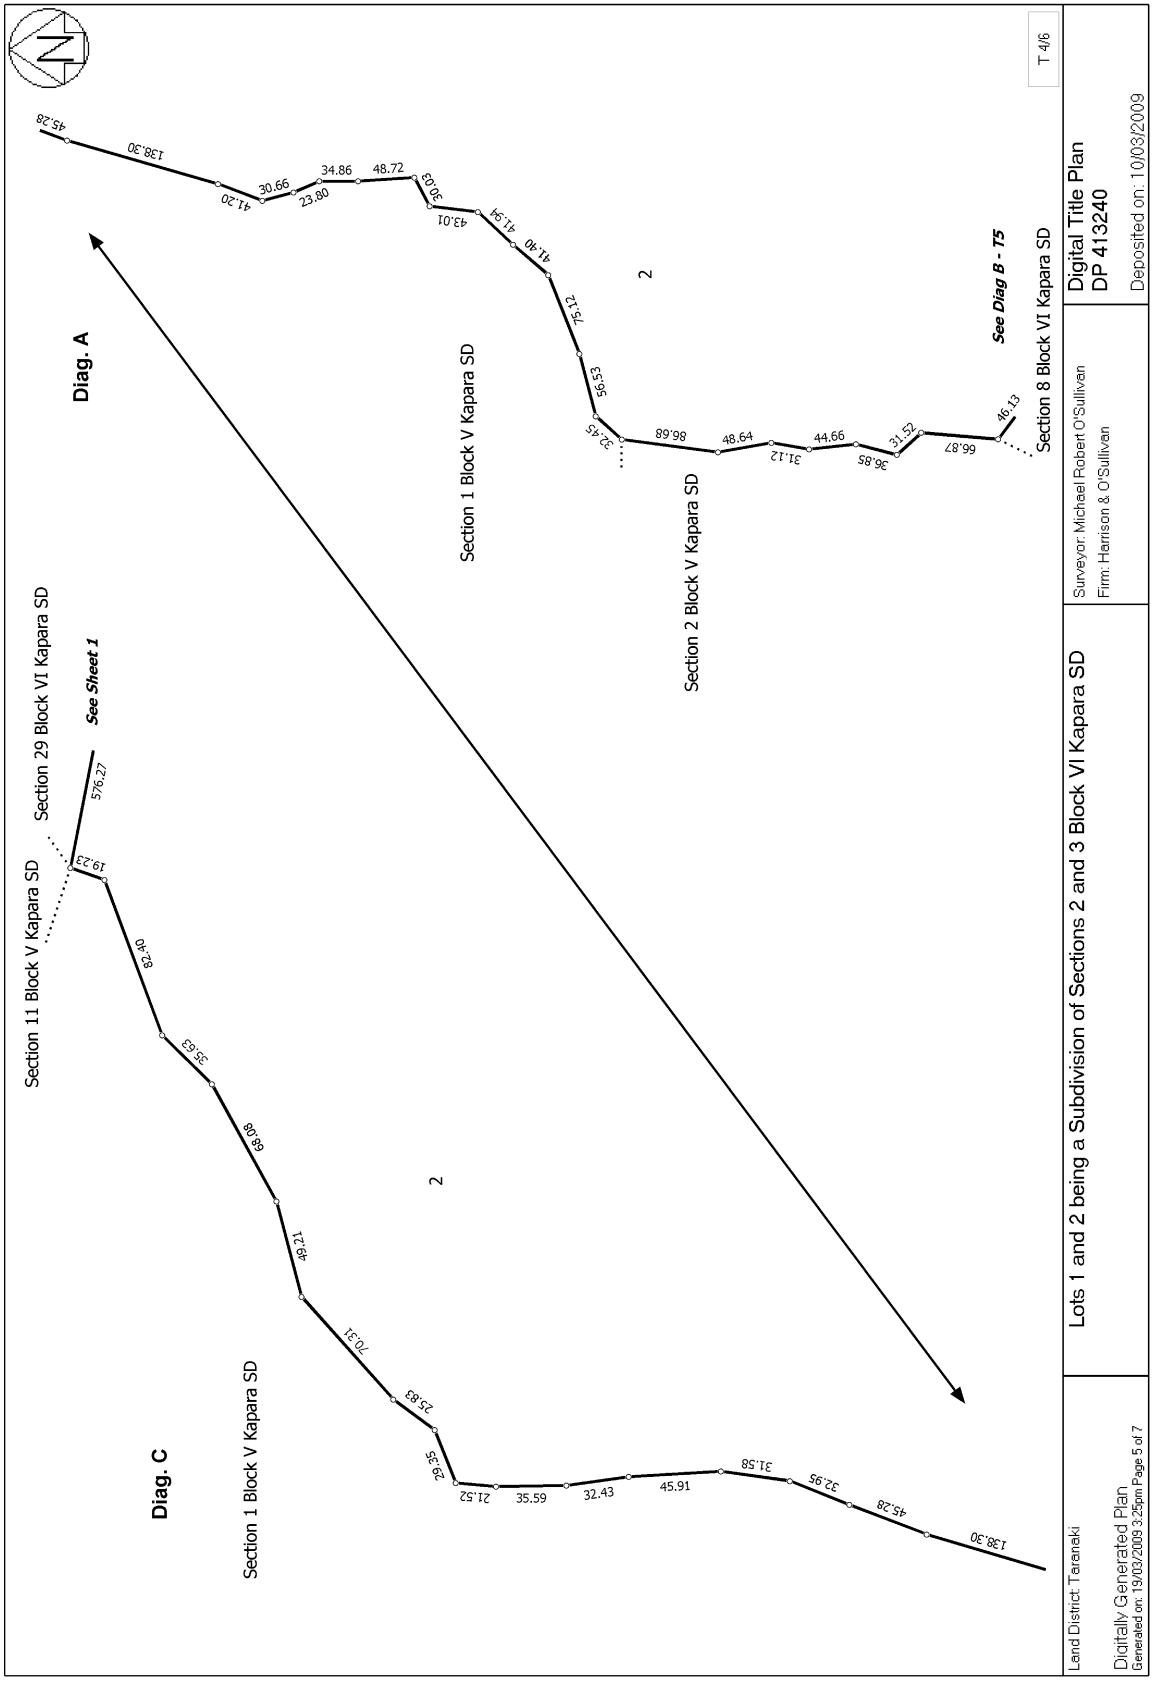
12717687.21 Mortgage of Forestry Right 12717687.18 to Vitol Asia PTE. Ltd. - 7.6.2023 at 2:45 pm

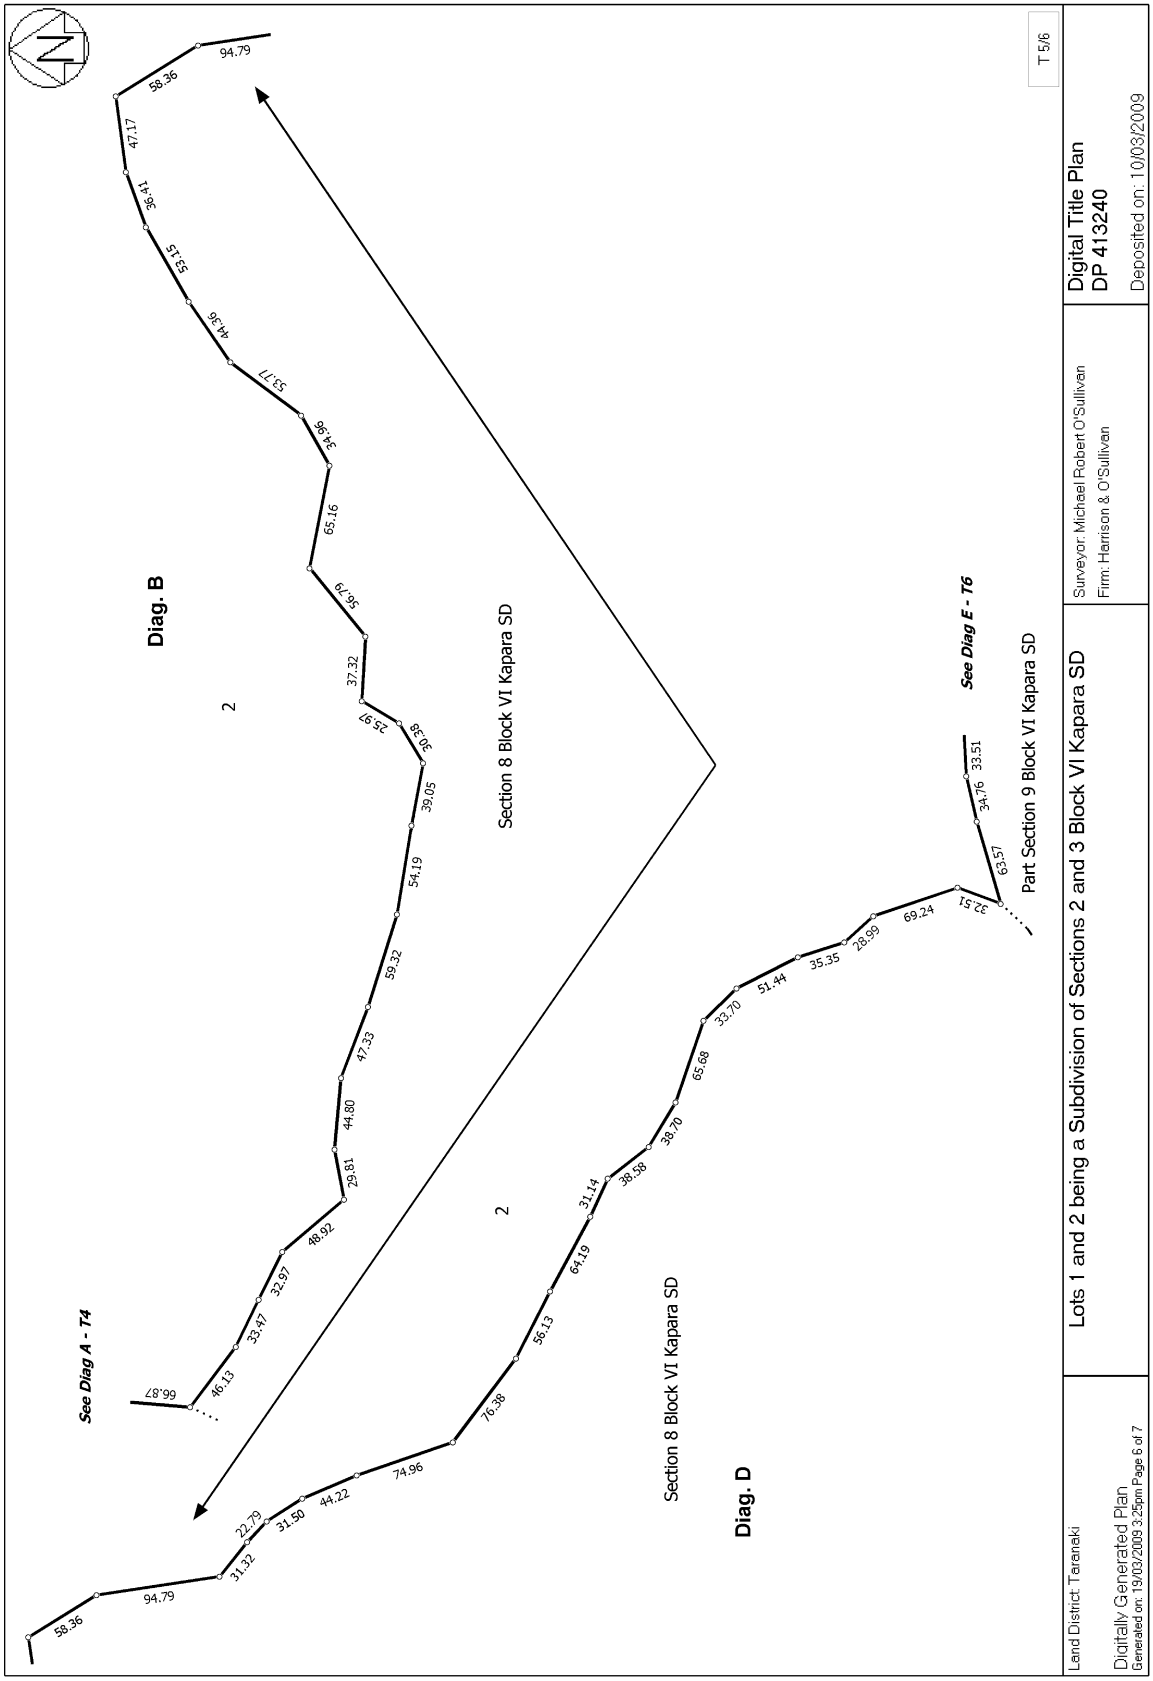
13068155.1 Notice pursuant to Section 195(2) Climate Change Response Act 2002 - 23.7.2024 at 4:31 pm

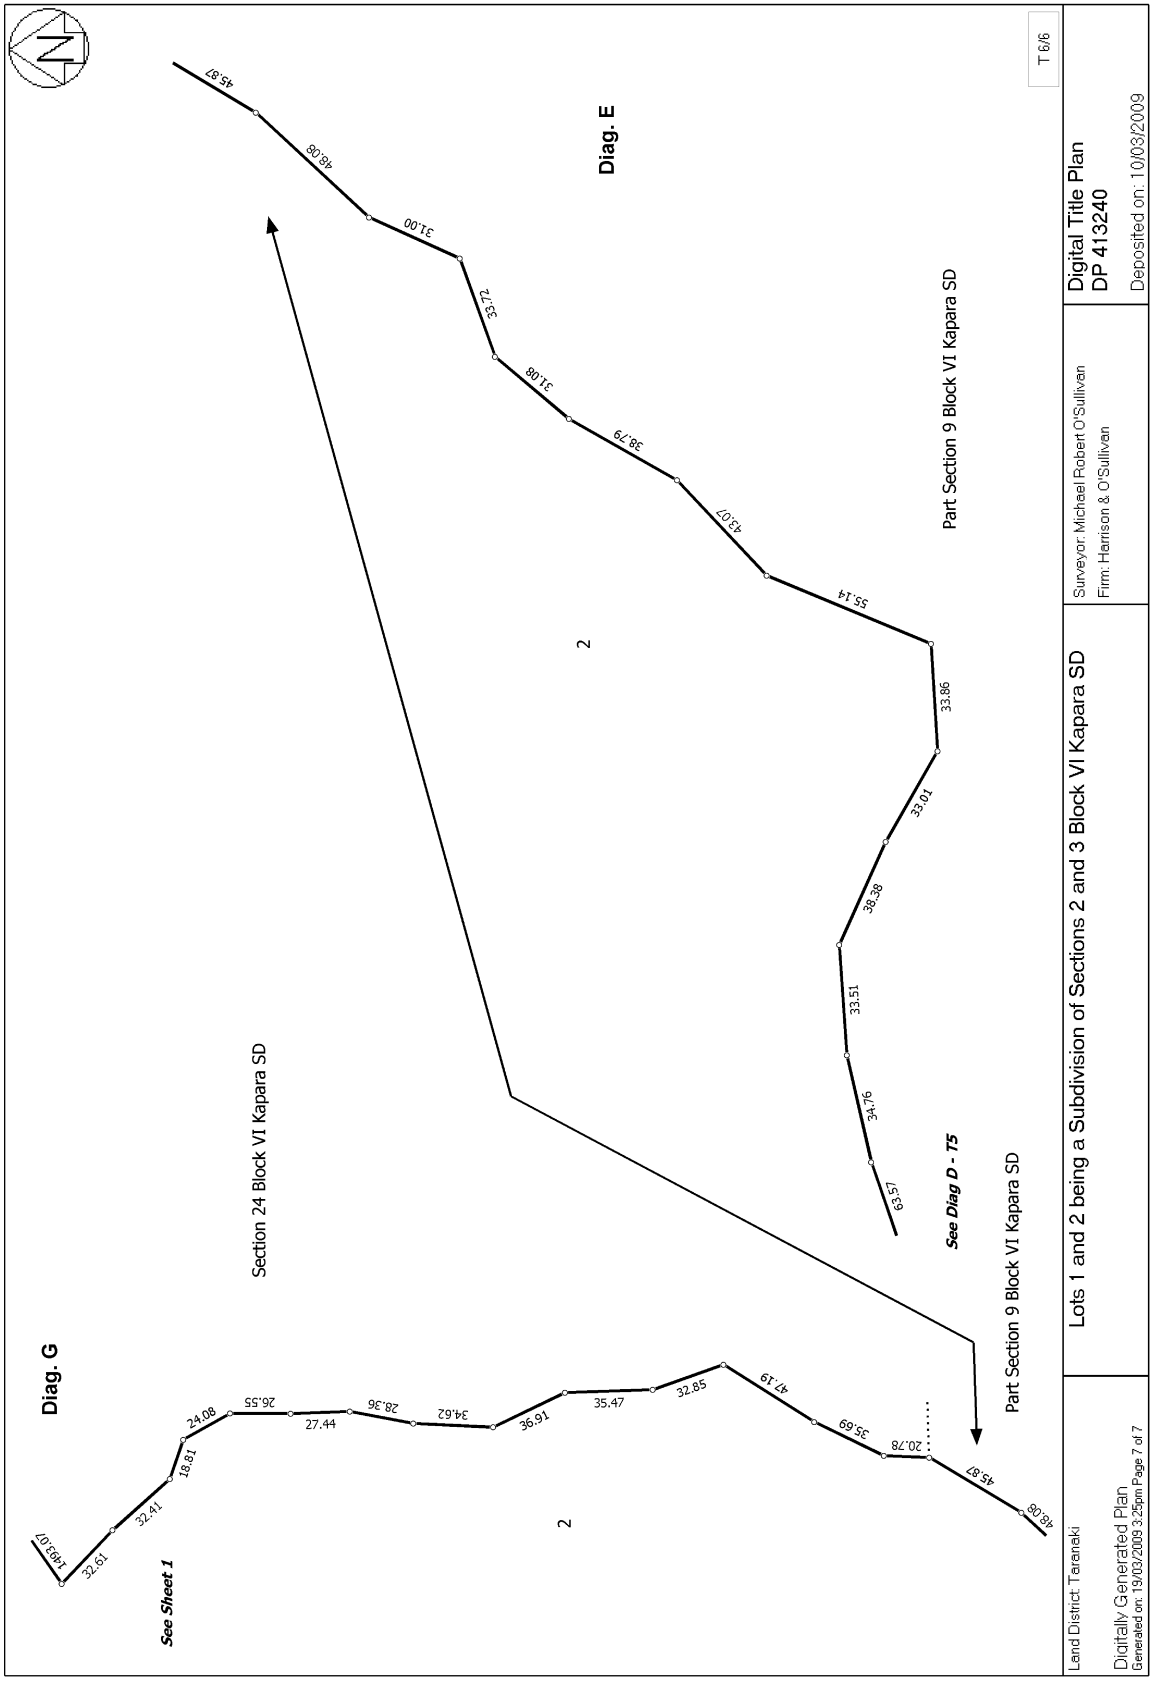

T 1/6
Lots 1 and 2 being a Subdivision of Sections 2 and 3 Block VI Kapara SD
Digital Title Plan
DP 413240
Deposited on: 10/03/2009
Surveyor: Michael Robert O'Sullivan
Firm: Harrison & O'Sullivan
Land District: Taranaki
Digitally Generated Plan
Generated on: 19/03/2009 3:25pm Page 2 of 7
WAITOTARA ROAD
WAITOTARA RIVER ROAD
Part Section 27 Block VI Kapara SD
Waitotara River
Section 30 Block VI Kapara SD
Section 29 Block VI Kapara SD
Section 1 Block V Kapara SD
Section 2 Block V Kapara SD
Section 8 Block VI Kapara SD
Section 4 Block VI Kapara SD
Section 24 Block VI Kapara SD
Part Section 9 Block VI Kapara SD
Diag. A See T4
Diag. B See T5
Diag. C See T4
Diag. D See T5
Diag. E See T6
Diag. F See T1
Diag. G See T6
Diag. H See T1
Diag. I See T2
Diag. J See T3
Diag. K See T3
1 8.0782Ha
2 338.5727Ha
2
Diag. F
See Diag H - T1
Diag. H
See Diag F - T1
224.46
182.39
1893.07
347.08
576.27
138.30
66.87
94.79
63.57
98.45
95.15
80.29
94.47
84.99
96.76
347.08
23.15
25.39
109.13
43.73
24.18
104.06
73.06
57.07
61.84
96.76
84.99


N
T 2/6
See Diag J - T3
See Diag K - T3
TAUMATATAHI ROAD
Diag. I
Diag. IA
See T2
Diag. IA
1
8.0782Ha
2
1
2
102.31
23.43
33.29
39.41
50.71
45.73
27.58
20.53
34.50
33.51
3.64
29.45
182.39
66.59
14.90
30.52
18.84
35.79
32.72
19.28
9.68
20.28
41.07
29.49
25.26
23.08
26.44
13.71
32.18
70.64
80.63
19.86
1.59
71.39
29.49
25.26
20.45
24.73
25.57
6.75
7.38
9.43
23.08
26.44
Land District Taranaki
Digitally Generated Plan
Generated on: 19/03/2009 3:25pm Page 3 of 7
Lots 1 and 2 being a Subdivision of Sections 2 and 3 Block VI Kapara SD
Surveyor: Michael Robert O'Sullivan
Firm: Harrison & O'Sullivan
Digital Title Plan
DP 413240
Deposited on: 10/03/2009


Diag. J
Diag. K
WAITOTARA RIVER ROAD
TAUMATATAHI ROAD
Section 30 Block VI Kapara SD
Section 4 Block VI Kapara SD
See Sheet 1
See Diag I - T2
T 3/6
Digital Title Plan
DP 413240
Deposited on: 10/03/2009
Surveyor: Michael Robert O'Sullivan
Firm: Harrison & O'Sullivan
Lots 1 and 2 being a Subdivision of Sections 2 and 3 Block VI Kapara SD
Land District: Taranaki
Digitally Generated Plan
Generated on: 19/03/2009 3:25pm Page 4 of 7


Diag. A
Diag. C
Section 11 Block V Kapara SD
Section 29 Block VI Kapara SD
Section 1 Block V Kapara SD
Section 1 Block V Kapara SD
Section 2 Block V Kapara SD
Section 8 Block VI Kapara SD
See Sheet 1
See Diag B - T5
2
2
T 4/6
Land District Taranaki
Lots 1 and 2 being a Subdivision of Sections 2 and 3 Block VI Kapara SD
Digitally Generated Plan
Generated on: 19/03/2009 3:25pm Page 5 of 7
Surveyor: Michael Robert O'Sullivan
Firm: Harrison & O'Sullivan
Digital Title Plan
DP 413240
Deposited on: 10/03/2009


T 5/6
Diag. B
Diag. D
Section 8 Block VI Kapara SD
Section 8 Block VI Kapara SD
Part Section 9 Block VI Kapara SD
See Diag A - T4
See Diag E - T6
Lots 1 and 2 being a Subdivision of Sections 2 and 3 Block VI Kapara SD
Land District: Taranaki
Digitally Generated Plan
Generated on: 19/03/2009 3:25pm Page 6 of 7
Surveyor: Michael Robert O'Sullivan
Firm: Harrison & O'Sullivan
Digital Title Plan
DP 413240
Deposited on: 10/03/2009


Diag. G
Diag. E
See Sheet 1
See Diag D - T5
Section 24 Block VI Kapara SD
Part Section 9 Block VI Kapara SD
Part Section 9 Block VI Kapara SD
2
2
T 6/6
Lots 1 and 2 being a Subdivision of Sections 2 and 3 Block VI Kapara SD
Digital Title Plan
DP 413240
Deposited on: 10/03/2009
Surveyor: Michael Robert O'Sullivan
Firm: Harrison & O'Sullivan
Land District: Taranaki
Digitally Generated Plan
Generated on: 19/03/2009 3:25pm Page 7 of 7