RECORD OF TITLE
UNDER LAND TRANSFER ACT 2017
FREEHOLD

Guaranteed Search Copy issued under Section 60 of the Land Transfer Act 2017

R.W. Muir
Registrar-General
of Land

Identifier **690021**
Land Registration District **Wellington**
Date Issued 19 November 2015

Prior References
WN53B/172 WN53B/173

Estate Fee Simple
Area 27.2445 hectares more or less
Legal Description Lot 1 Deposited Plan 484884 and Lot 4 Deposited Plan 85385

Registered Owners
Nirvana Farm Limited

Interests

Subject to Section 8 Atomic Energy Act 1945

Subject to Section 3 Geothermal Energy Act 1953

Subject to Section 3 Petroleum Act 1937

Subject to Sections 6 and 8 Mining Act 1971

Subject to Part IV A Conservation Act 1987

Subject to Sections 5 and 261 Coal Mines Act 1979

Subject to a right to transmit electricity over part Lot 4 DP 85385 marked A on DP 85385 specified in Easement Certificate B808192.5 - 27.10.2000 at 9.57 am

Subject to Section 241(2) Resource Management Act 1991 (affects DP 484884)

Land Covenant (in gross) in favour of Vitol Asia PTE. Ltd. created by Covenant Instrument 12717687.16 - 7.6.2023 at 2:45 pm

12717687.17 Mortgage to Vitol Asia PTE. Ltd. - 7.6.2023 at 2:45 pm

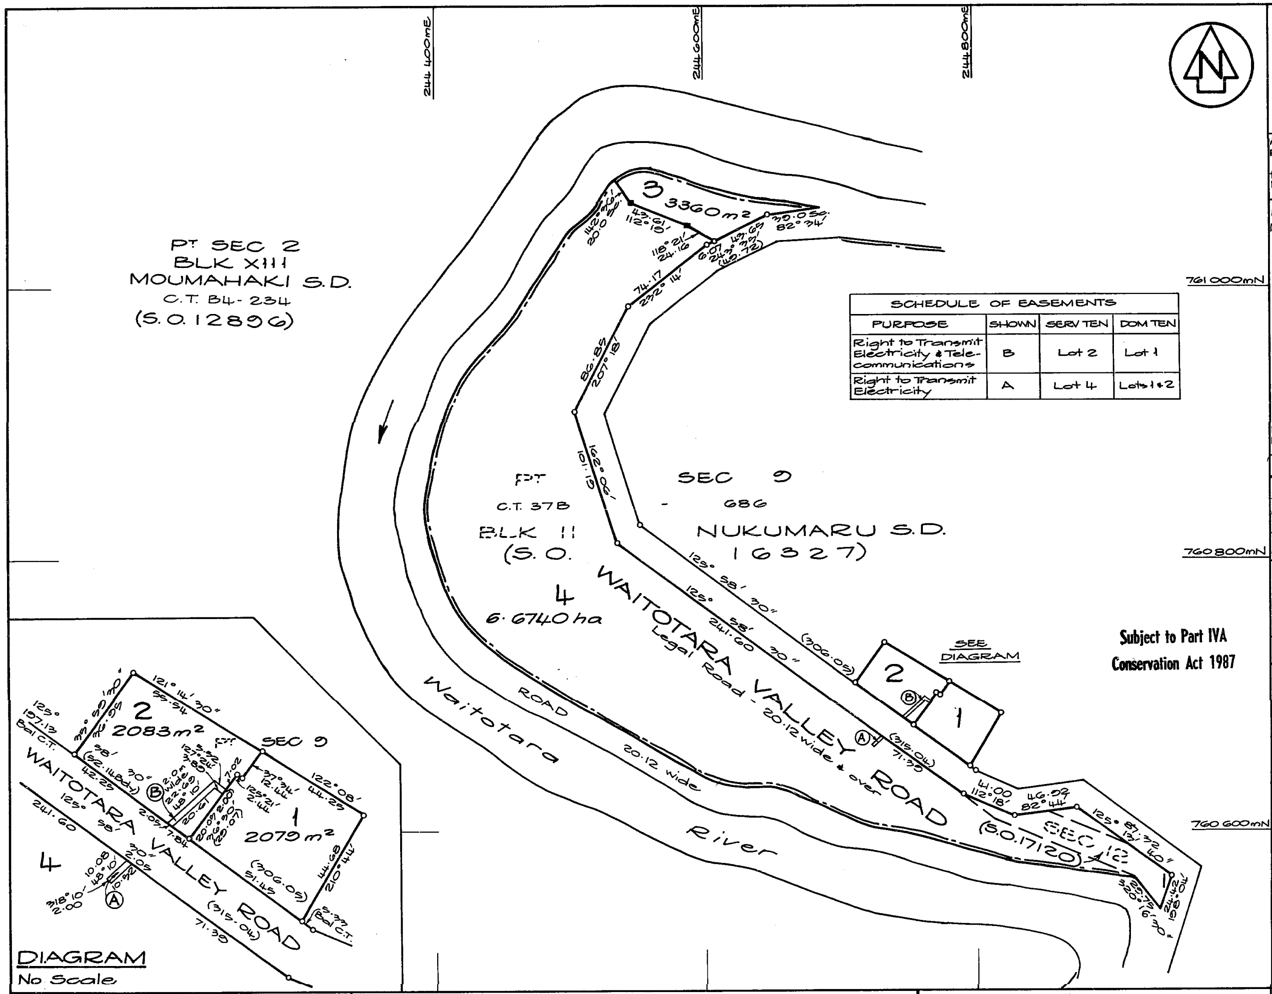

SCHEDULE OF EASEMENTS			
PURPOSE	SHOWN	SERV TEN	DOM TEN
Right to Transmit Electricity & Tele-communications	B	Lot 2	Lot 1
Right to Transmit Electricity	A	Lot 4	Lots 1+2

Subject to Part IVA Conservation Act 1987

Approvals APPROVED

R.R. Marshall

REGISTERED OWNERS

Approved pursuant to Section 223 of the Resource Management Act 1991 on the 11 day of December 1997. Subject to the amalgamation condition set out hereon.

The common seal of the South Taranaki District Council is affixed hereto in the presence of:

CHAIRMAN OF THE JUDICIAL COMMITTEE

GENERAL MANAGER

Pursuant to Section 224(c) of the Resource Management Act 1991 I hereby certify that all the conditions of the subdivision consent have been complied with to the satisfaction of the South Taranaki District Council
Dated this 11 day of December 1997

GENERAL MANAGER

AMALGAMATION CONDITION

That Lot 3 hereon be transferred to the owner of Part Section 2 Block XIII Moumahaki Survey District (C.T. B4/234) and that one Certificate of Title be issued to include those parcels.
Land Registry Office Reference B.621944.1

NEW C of T ALLOCATED:
Lot 1 - 53B/169
Lot 2 - 53B/170
Lot 3 and C.T. B4/234 - 53B/171
Lot 4 - 53B/172   Bal - 53B/173

Total Area 7.4262ha

Comprised in C.T. 37B - 686 (Part)

I, MICHAEL ROBERT O'SULLIVAN
Registered Surveyor and holder of an annual practising certificate (or who may act as a registered surveyor pursuant to section 25 of the Survey Act 1986) hereby certify that this plan has been made from surveys executed by me or under my directions, that both plan and survey are correct and have been made in accordance with the Survey Regulations 1972 or any regulations made in substitution thereof.
Dated at Wanganui *this* 26th *day of* November 1997 *Signature* M.R. O'Sullivan

Field Book 6412 *p.* 1 - 12 *Traverse Book* 575 *p.* 31-35
Reference Plans S.Os 15071, 16327, 17120, 32036, 33344
Examined .... *Correct* S. Collins

Approved as to Survey
12/2/98 Chief Surveyor

Deposited this 27th day of October 19 2000
for Registrar-General of Land
District Land Registrar

File
Received 13-1-98
Instructions

85385

LAND DISTRICT Wellington
SURVEY BLK. & DIST. 11 Nukumaru
NZMS 261 SHT R21 RECORD MAP No ....

LOTS 1 - 4 BEING SUBDIVISION OF
SEC 12 & PT SEC 9 BLK 11 NUKUMARU S.D

TERRITORIAL AUTHORITY South Taranaki District 97-086
Surveyed by Harrison & O'Sullivan
Scale 1 : 2000 Date Nov 1997

A.J. BEVIN, SURVEYOR GENERAL, LAND INFORMATION, NEW ZEALAND.

[redacted] [redacted]

L.I.N.Z. FORM DI5 "APPROVED M92/03"

AARQUE

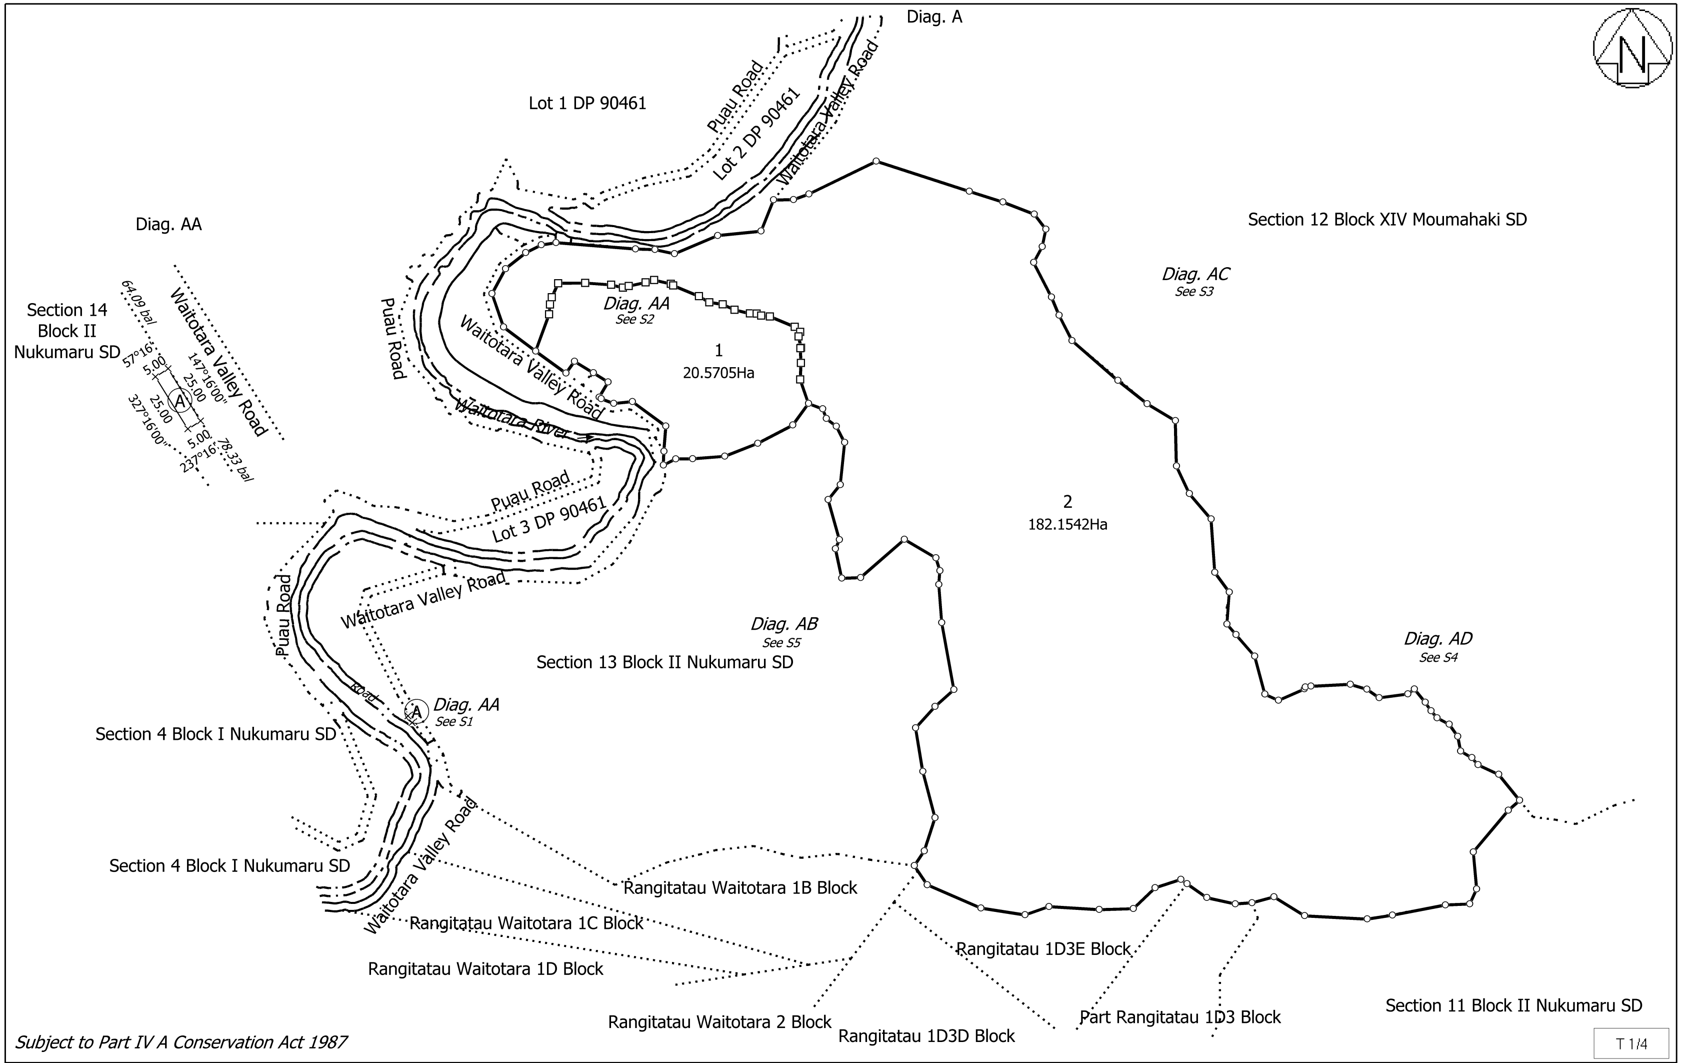

Subject to Part IV A Conservation Act 1987

Land District: Wellington Digitally Generated Plan Generated on: 01/07/2015 2:29pm Page 3 of 6	Lots 1 & 2 Being Subdivision of Part Section 9 Block II Nukumaru SD and Easement over Section 14 Block II Nukumaru SD	Surveyor: Steven Paul Archer Firm: A & C Surveys Ltd (Wanganui)	Title Plan LT 484884 Approved on: 1/07/2015