RECORD OF TITLE
UNDER LAND TRANSFER ACT 2017
FREEHOLD

Guaranteed Search Copy issued under Section 60 of the Land Transfer Act 2017

R.W. Muir
Registrar-General
of Land

Identifier **753569**

Land Registration District **Wellington**

Date Issued 09 March 2017

Prior References

WN29A/242 WN501/180

Estate Fee Simple

Area 89.7128 hectares more or less

Legal Description Lot 2-3 Deposited Plan 500597

Registered Owners

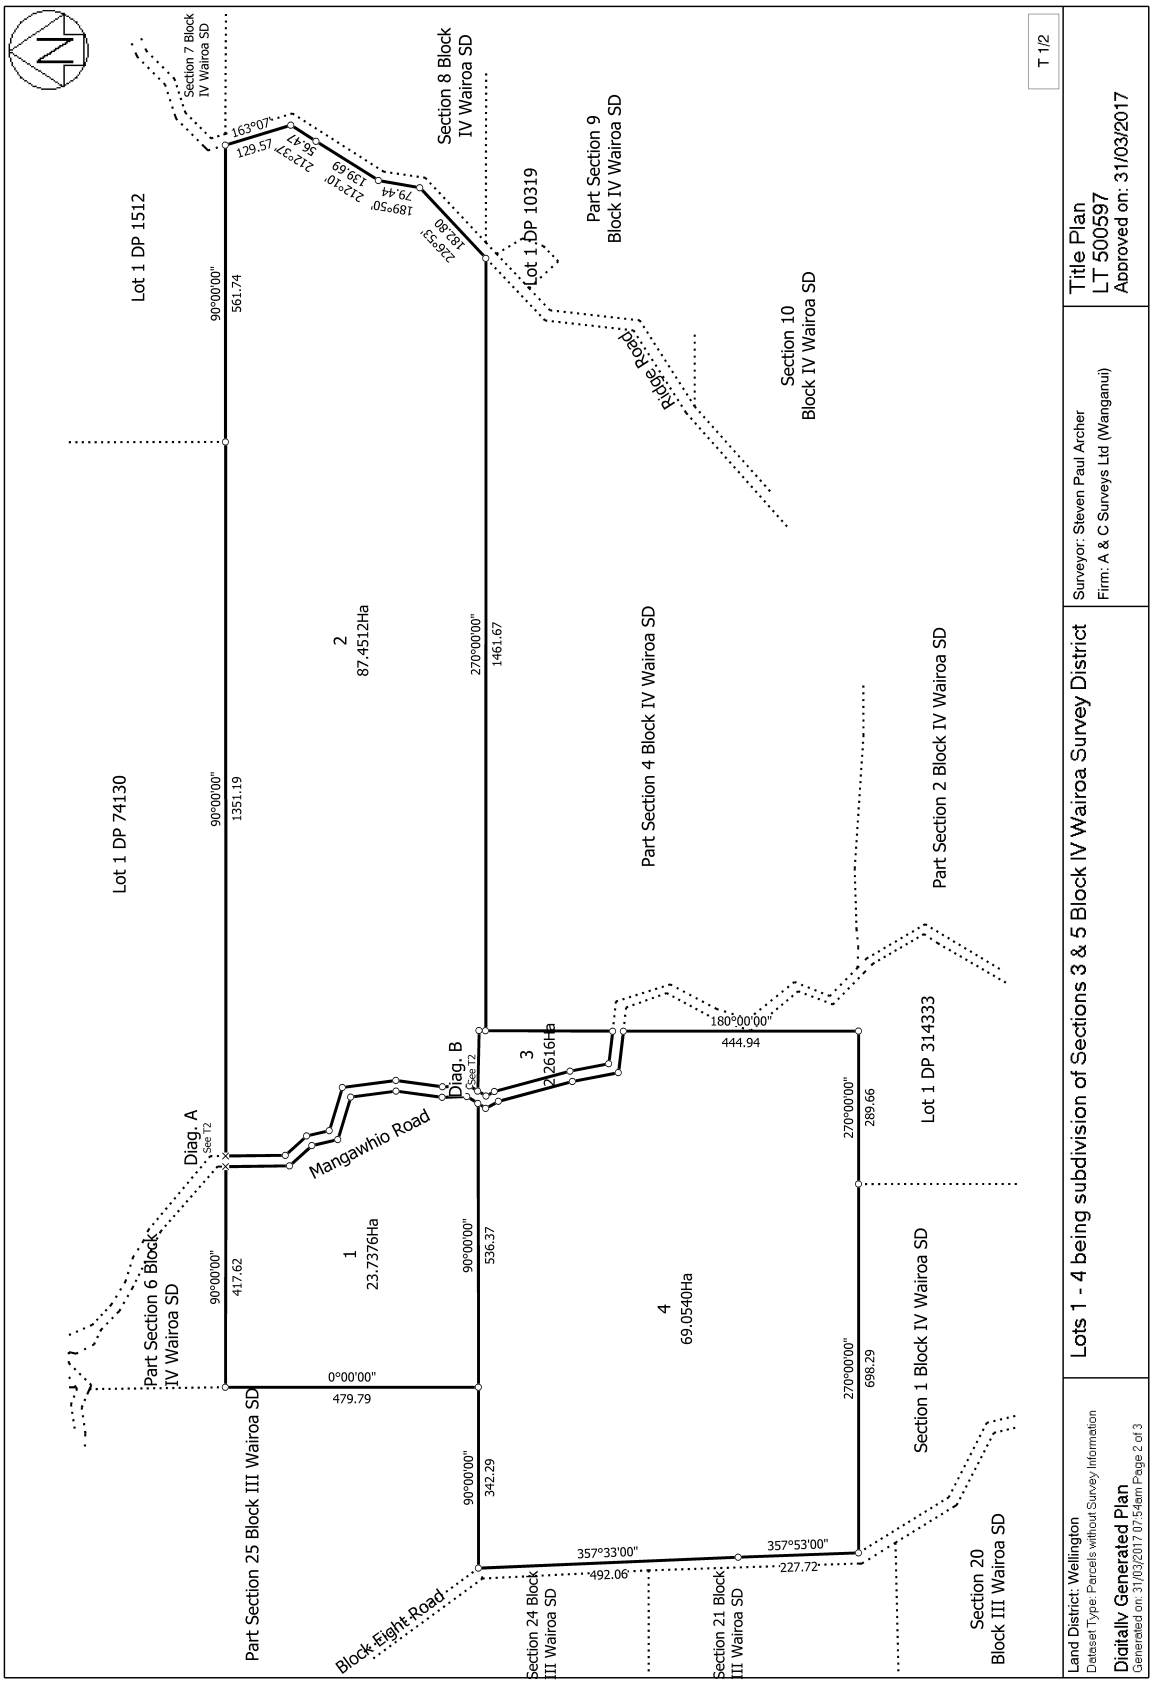
Nirvana Farm Limited

Interests

Subject to Section 241(2) and Sections 242(1) and (2) Resource Management Act 1991 (affects DP 500597)

Land Covenant (in gross) in favour of Vitol Asia PTE. Ltd. created by Covenant Instrument 12717687.16 - 7.6.2023 at 2:45 pm

12717687.17 Mortgage to Vitol Asia PTE. Ltd. - 7.6.2023 at 2:45 pm


T 1/2
Title Plan
LT 500597
Approved on: 31/03/2017
Surveyor: Steven Paul Archer
Firm: A & C Surveys Ltd (Wanganui)
Lots 1 - 4 being subdivision of Sections 3 & 5 Block IV Wairoa Survey District
Land District: Wellington
Dataset Type: Parcels without Survey Information
Digitally Generated Plan
Generated on: 31/03/2017 07:54am Page 2 of 3
Section 7 Block IV Wairoa SD
Section 8 Block IV Wairoa SD
Part Section 9 Block IV Wairoa SD
Lot 1 DP 10319
Ridge Road
Section 10 Block IV Wairoa SD
Lot 1 DP 1512
Lot 1 DP 74130
Part Section 4 Block IV Wairoa SD
Part Section 2 Block IV Wairoa SD
Lot 1 DP 314333
Section 1 Block IV Wairoa SD
Part Section 6 Block IV Wairoa SD
Part Section 25 Block III Wairoa SD
Section 24 Block III Wairoa SD
Section 21 Block III Wairoa SD
Section 20 Block III Wairoa SD
Mangawhio Road
Block Eight Road
Diag. A
See T2
Diag. B
See T2
1
23.7376Ha
2
87.4512Ha
3
2.2616Ha
4
69.0540Ha
163°07'
129.57
56.47
212°37'
139.69
212°10'
79.44
189°50'
182.60
226°53'
561.74
90°00'00"
1351.19
90°00'00"
1461.67
270°00'00"
417.62
90°00'00"
536.37
90°00'00"
479.79
0°00'00"
342.29
90°00'00"
444.94
180°00'00"
289.66
270°00'00"
698.29
270°00'00"
492.06
357°33'00"
227.72
357°53'00"