


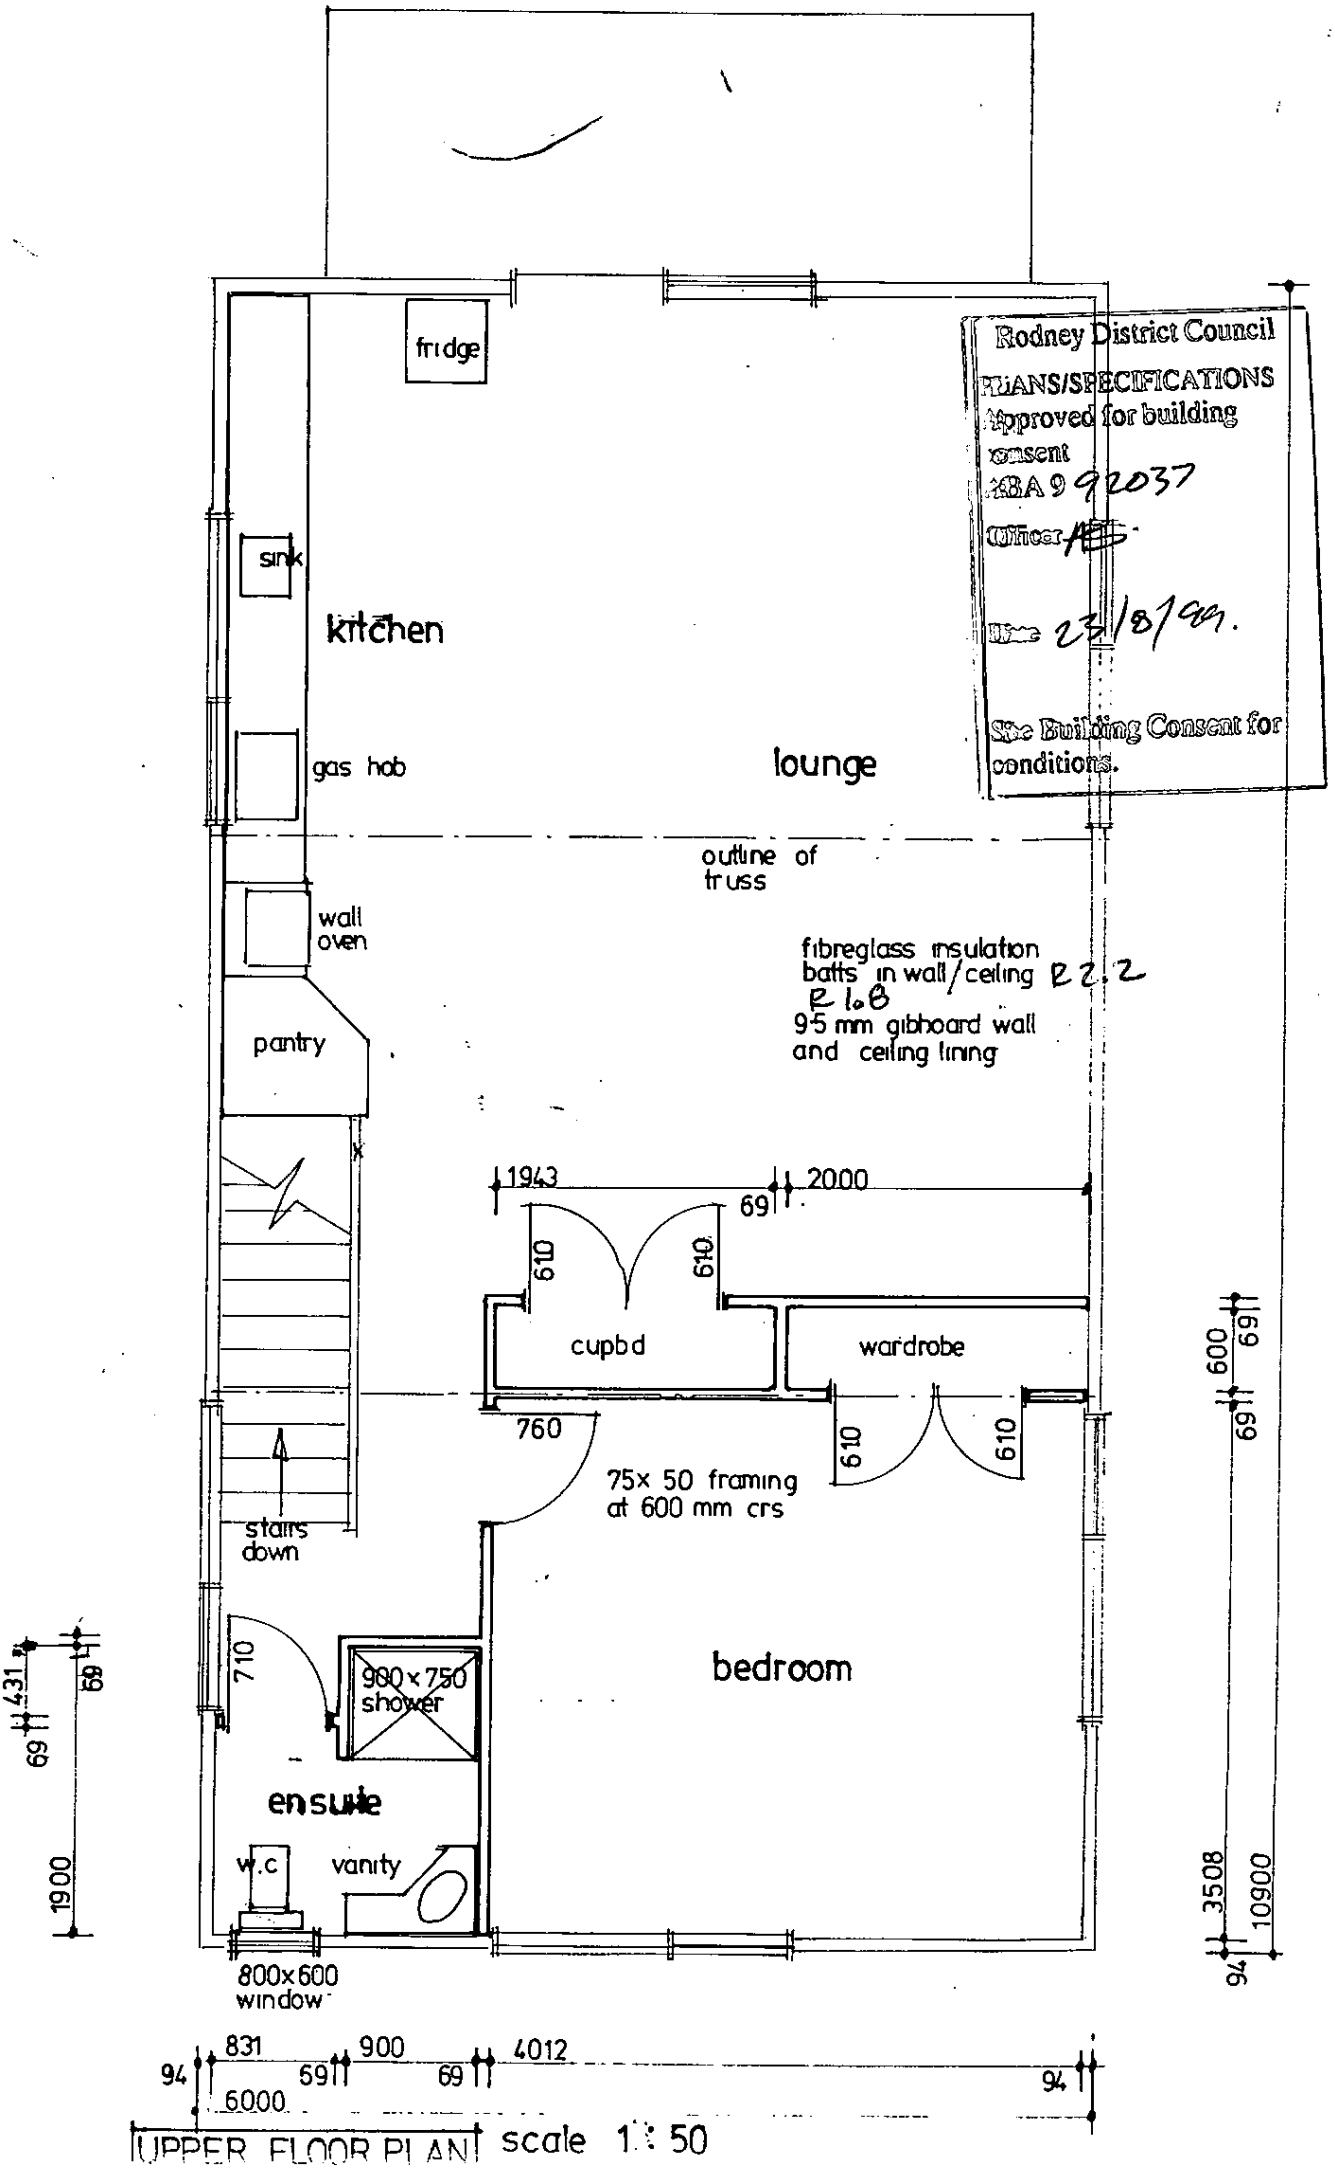



UPPER FLOOR PLAN scale 1:50

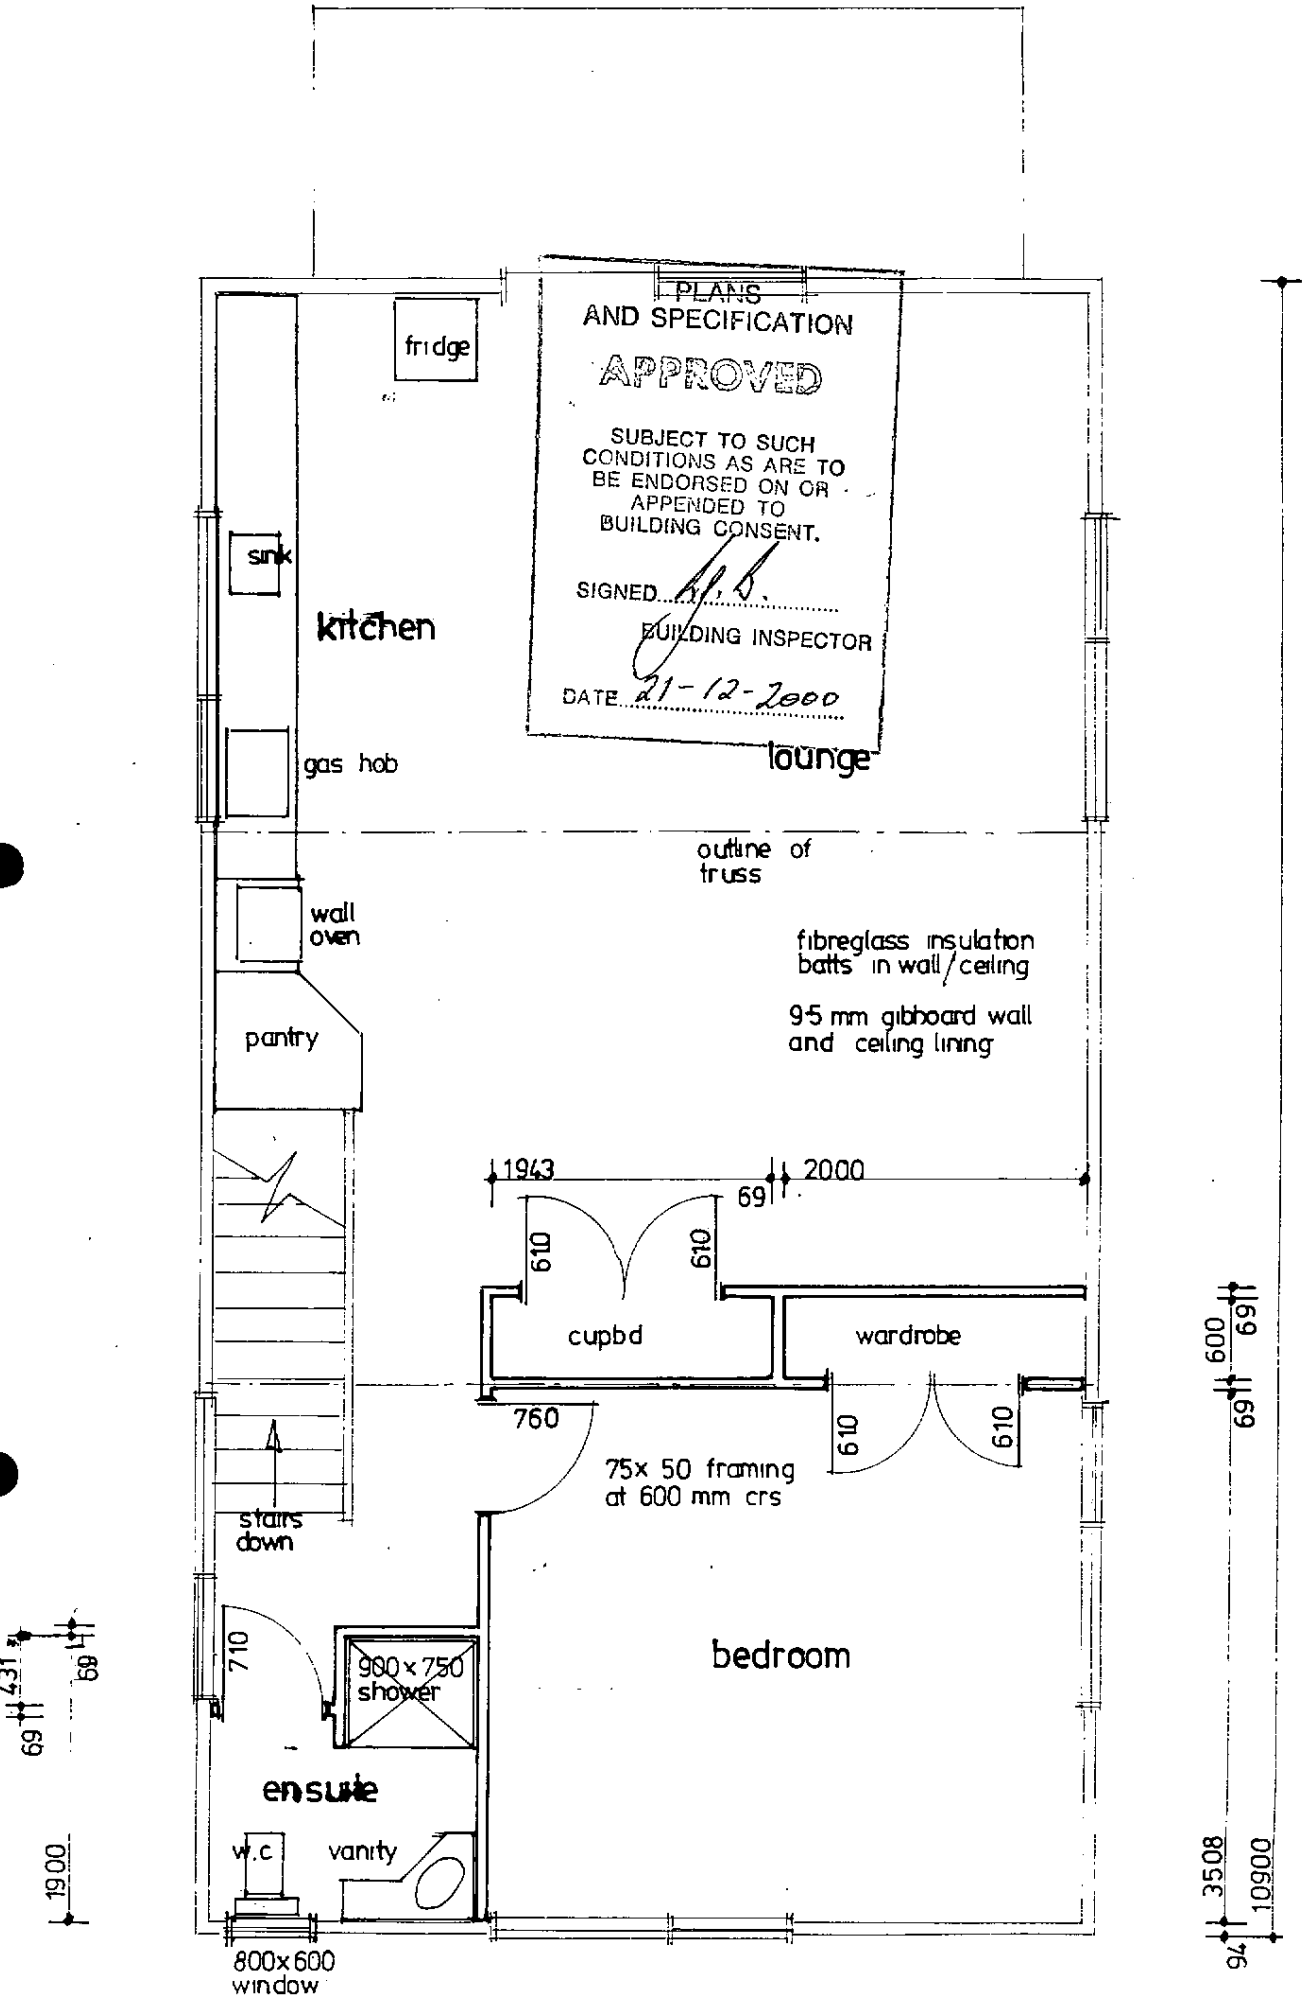


UPPER FLOOR PLAN scale 1:50
(in existing shed)

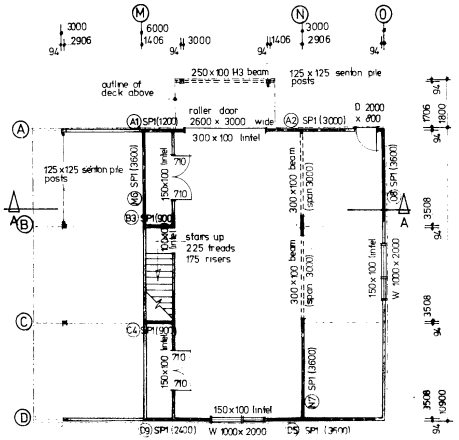

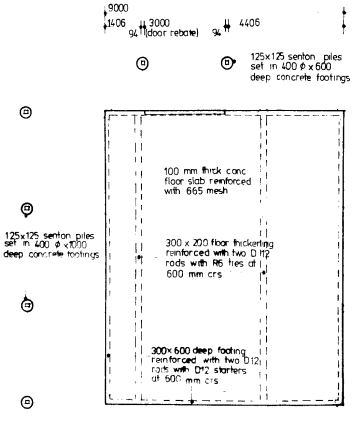


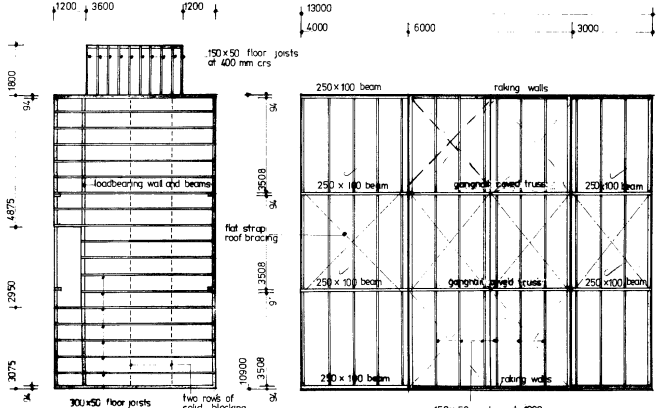


ground floor plan
scale 1 : 100

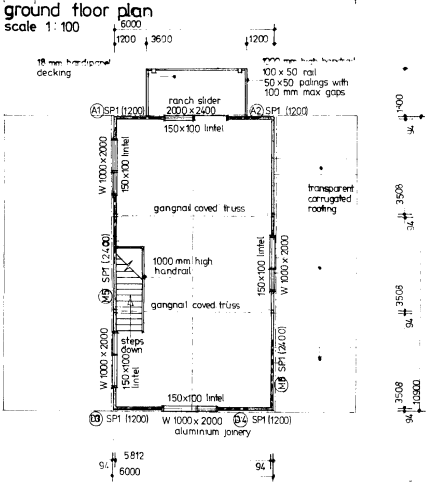

upper floor plan
scale 1 : 100

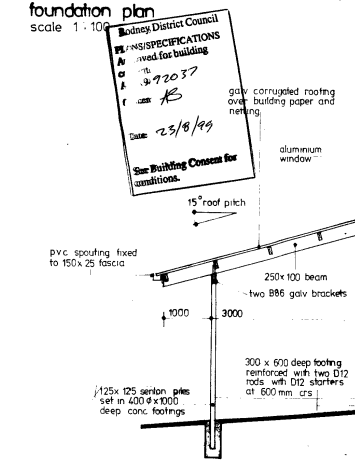

Rodney District Council
PLANS/SPECIFICATIONS
Approved for building
Consent #92037
Date: 23/8/99
Subject to Building Consent for conditions.

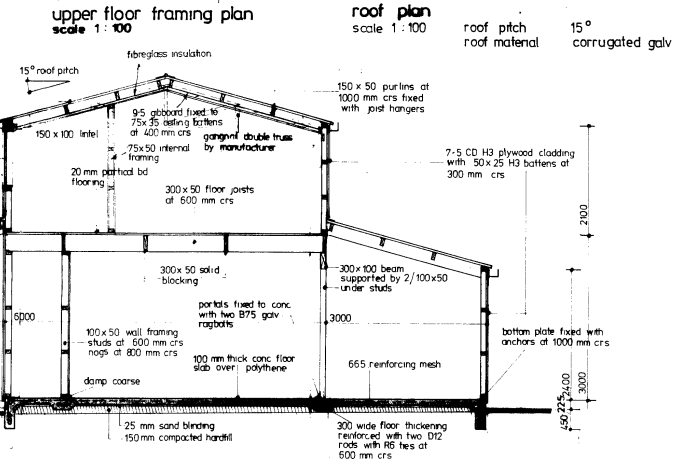

roof plan
scale 1 : 100

roof pitch 15°
roof material corrugated galv iron

cross section A-A
scale 1 : 50


ground floor area	130 m²
upper floor area	65 m²
total	195 m²

Puhoi Design
architectural draughting
27 Saleyards rd Puhoi
phone (09)4220636
mobile (025)2215475


PROPOSED SHED-WORKSHOP AT REMIGER RD PUHOI FOR R NICKLIN

ground and upper floor plan, foundation, subfloor, roof plan, cross section


drawn D.W. PAPPRILL | scale 1:100, 50 | sheet 1
date JULY 1998 | ref

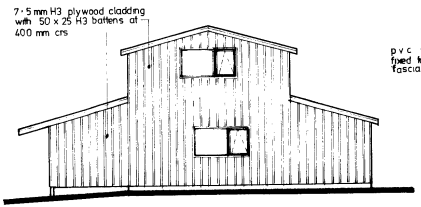


south elevation
scale 1:100

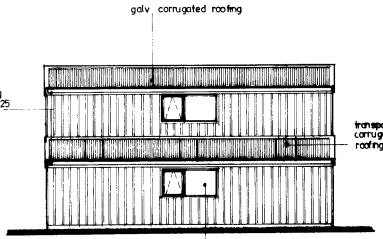

east elevation
scale 1:100

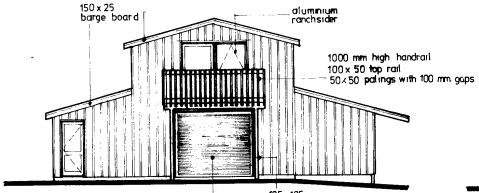

north elevation
scale 1:100

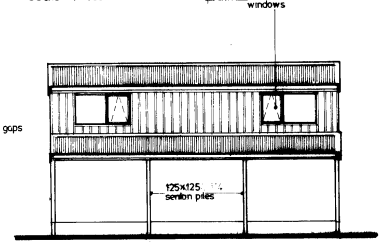

west elevation
scale 1:100


Rodney District Council
PLANS/SPECIFICATIONS
Approved for building consent
ABA 9 72037
Officer [illegible]
Date 23/8/89
See Building Consent for conditions.

Puhoi Design
architectural draughting
27 Saleyards rd Puhoi
phone (09)4220636
mobile (025)2215475

PROPOSED SHED-WORKSHOP AT REMIGER RD PUHOI FOR R NICKLIN

elevations	drawn D W PAPPILL	scale 1:100	sheet 2
	date JULY 1998	ref	

PLANS
AND SPECIFICATION
APPROVED
SUBJECT TO SUCH CONDITIONS AS ARE TO BE ENDORSED ON OR APPENDED TO BUILDING CONSENT.
SIGNED ..... BUILDING INSPECTOR
DATE 21-12-2000

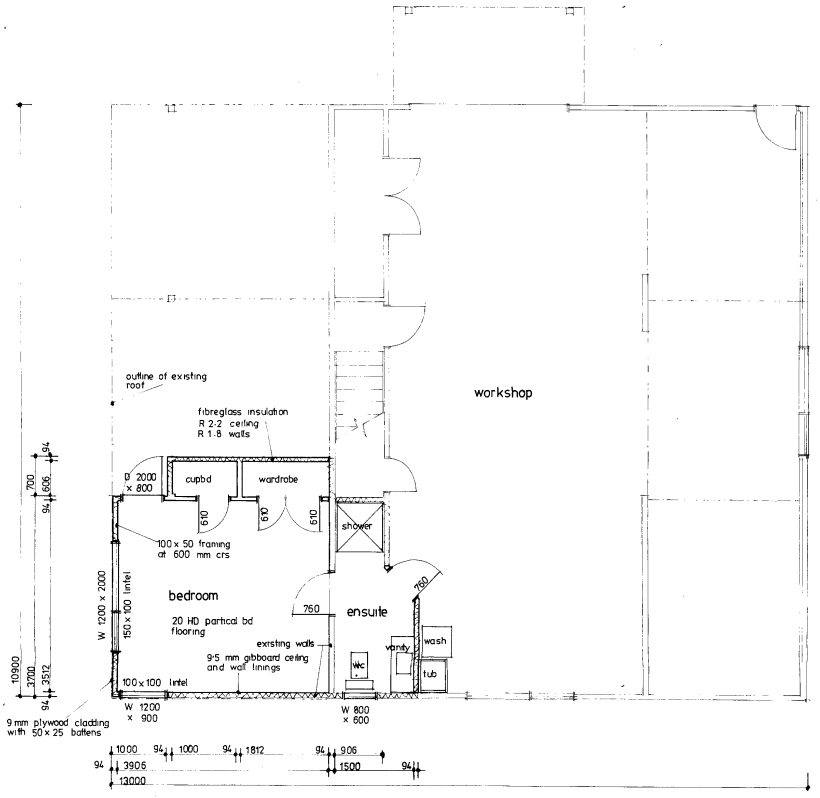

ground floor plan
(alteration in existing shed)
scale 1:50