Title Plan - LT 541977

Survey Number	LT 541977
Surveyor Reference	40320 Nicklin (stage 1)
Surveyor	Bradley Mark Mowat
Survey Firm	Cato Bolam Consultants Ltd (Orewa)
Surveyor Declaration	

Survey Details

Dataset Description	Lots 2, 4, 5 & 6 Being Subdivision of Lot 8 DP 208981 & Land Covenant over Allot 32 Puhoi Parish		
Status	Initiated		
Land District	North Auckland	**Survey Class**	Class B
Submitted Date		**Survey Approval Date**	
		Deposit Date	

Territorial Authorities

Auckland Council

Comprised In

RT NA2100/21 Ltd
RT NA137A/506 Ltd
RT NA757/204 Ltd
RT NA31C/965

Created Parcels

Parcels	Parcel Intent	Area	RT Reference
Lot 2 Deposited Plan 541977	Fee Simple Title	1.1120 Ha	911732
Area B Deposited Plan 541977	Easement		
Area C Deposited Plan 541977	Easement		
Area D Deposited Plan 541977	Easement		
Area EC Deposited Plan 541977	Easement		
Area NA Deposited Plan 541977	Easement		
Area P Deposited Plan 541977	Easement		
Area Q Deposited Plan 541977	Easement		
Area U Deposited Plan 541977	Easement		
Area V Deposited Plan 541977	Easement		
Area X Deposited Plan 541977	Easement		
Area E Deposited Plan 541977	Easement		
Area EG Deposited Plan 541977	Easement		
Area I Deposited Plan 541977	Easement		
Area J Deposited Plan 541977	Easement		
Area K Deposited Plan 541977	Easement		
Area L Deposited Plan 541977	Easement		
Area M Deposited Plan 541977	Easement		
Area CW Deposited Plan 541977	Easement		
Area CX Deposited Plan 541977	Covenant - Land		

Title Plan - LT 541977

Created Parcels

Parcels	Parcel Intent	Area	RT Reference
Lot 4 Deposited Plan 541977	Fee Simple Title	1.0010 Ha	911733
Lot 5 Deposited Plan 541977	Fee Simple Title	1.0000 Ha	911734
Lot 6 Deposited Plan 541977	Fee Simple Title	54.3132 Ha	911735
Area F Deposited Plan 541977	Easement		
Area G Deposited Plan 541977	Easement		
Area H Deposited Plan 541977	Easement		
Area EA Deposited Plan 541977	Easement		
Area EB Deposited Plan 541977	Easement		
Area ED Deposited Plan 541977	Easement		
Area EF Deposited Plan 541977	Easement		
Area EH Deposited Plan 541977	Easement		
Area N Deposited Plan 541977	Easement		
Area O Deposited Plan 541977	Easement		
Area EI Deposited Plan 541977	Easement		
Area EK Deposited Plan 541977	Easement		
Area CY Deposited Plan 541977	Covenant - Land		
Area CZ Deposited Plan 541977	Covenant - Land		
Area T Deposited Plan 541977	Easement		
Area CU Deposited Plan 541977	Covenant - Land		
Area CO Deposited Plan 541977	Covenant - Land		
Area EJ Deposited Plan 541977	Easement		
Area S Deposited Plan 541977	Easement		
Area EL Deposited Plan 541977	Easement		
Total Area		57.4262 Ha	

Our Ref: 40320

Cato Bolam
creating great places

Land Registration District
North Auckland

Plan Number
DP 541977

Territorial Authority
Auckland Council

TA Reference
SUB60315119
SUB60315119-A

MEMORANDUM OF EASEMENT(S)			
Purpose	Shown	Servient Tenement (Burdened Land)	Dominant Tenement (Benefited Land)
Right of Way, right to convey Electricity & Telecommunications	EA, EB, EC, G, NA, O & U	Lot 6 hereon	Lots 4 & 5 hereon
	ED	Lot 6 hereon	Lot 4 hereon
	EF, EG, EH, EI & N	Lot 5 hereon	Lot 6 hereon
	EJ & EL	Lot 4 hereon	Lot 6 hereon
Right to convey Electricity & Telecommunications	EL & S	Lot 4 hereon	Lot 5 hereon

SCHEDULE OF EXISTING EASEMENT(S) IN GROSS			
Purpose	Shown	Servient Tenement (Burdened Land)	Creating Document
Right to Convey Electricity	C	Lot 6 hereon	Transfer C640690.1
	G, H, I, J & R		Easement Instrument 9236051.4
	E & F	Lot 2 hereon	

SCHEDULE OF EXISTING EASEMENT(S)			
Purpose	Shown	Servient Tenement (Burdened Land)	Creating Document
Right of Way & telecommunications right	B, C & D	Lot 6 hereon	Easement Certificates D460766.5 & D611644.6
Electricity right	Q, T, U & V	Lot 6 hereon	Easement Certificate D460766.5
Telecommunications right	K, NA, & Q	Lot 6 hereon	Easement Certificate D460766.5
	I, L, M & N	Lot 5 hereon	Easement Certificate D460766.5
Transmit Electricity	O, P, T, U, V & X	Lot 6 hereon	Easement Instrument 6170820.9
Transmit Telecommunications	K, NA. O, P & X	Lot 6 hereon	Easement Instrument 6170820.9
	I, L, M & N	Lot 5 hereon	Easement Instrument 6170820.9


Proposed Covenants

Area CU is to be subject to a Land Covenant to protect the native bush within.

Areas CO, CX, CY & CZ are to be subject to Land Covenants to protect the riparian planting within.

Amalgamation Covenant


The owner of Lot 6 hereon, Allotments 32 & 35 & Part Allotments 30 & 31 (RT NA2100/21 Ltd), Allotment 54A Parish of Puhoi (RT NA31C/965), Lot 1 DP 179794 (RT NA105B/748) and Part Allotment 36 Parish of Puhoi (RT NA757/204 Ltd) shall not without the consent of the Council, transfer, lease or otherwise dispose of any of those parcels of land or any part thereof, except in conjunction with the other or others.

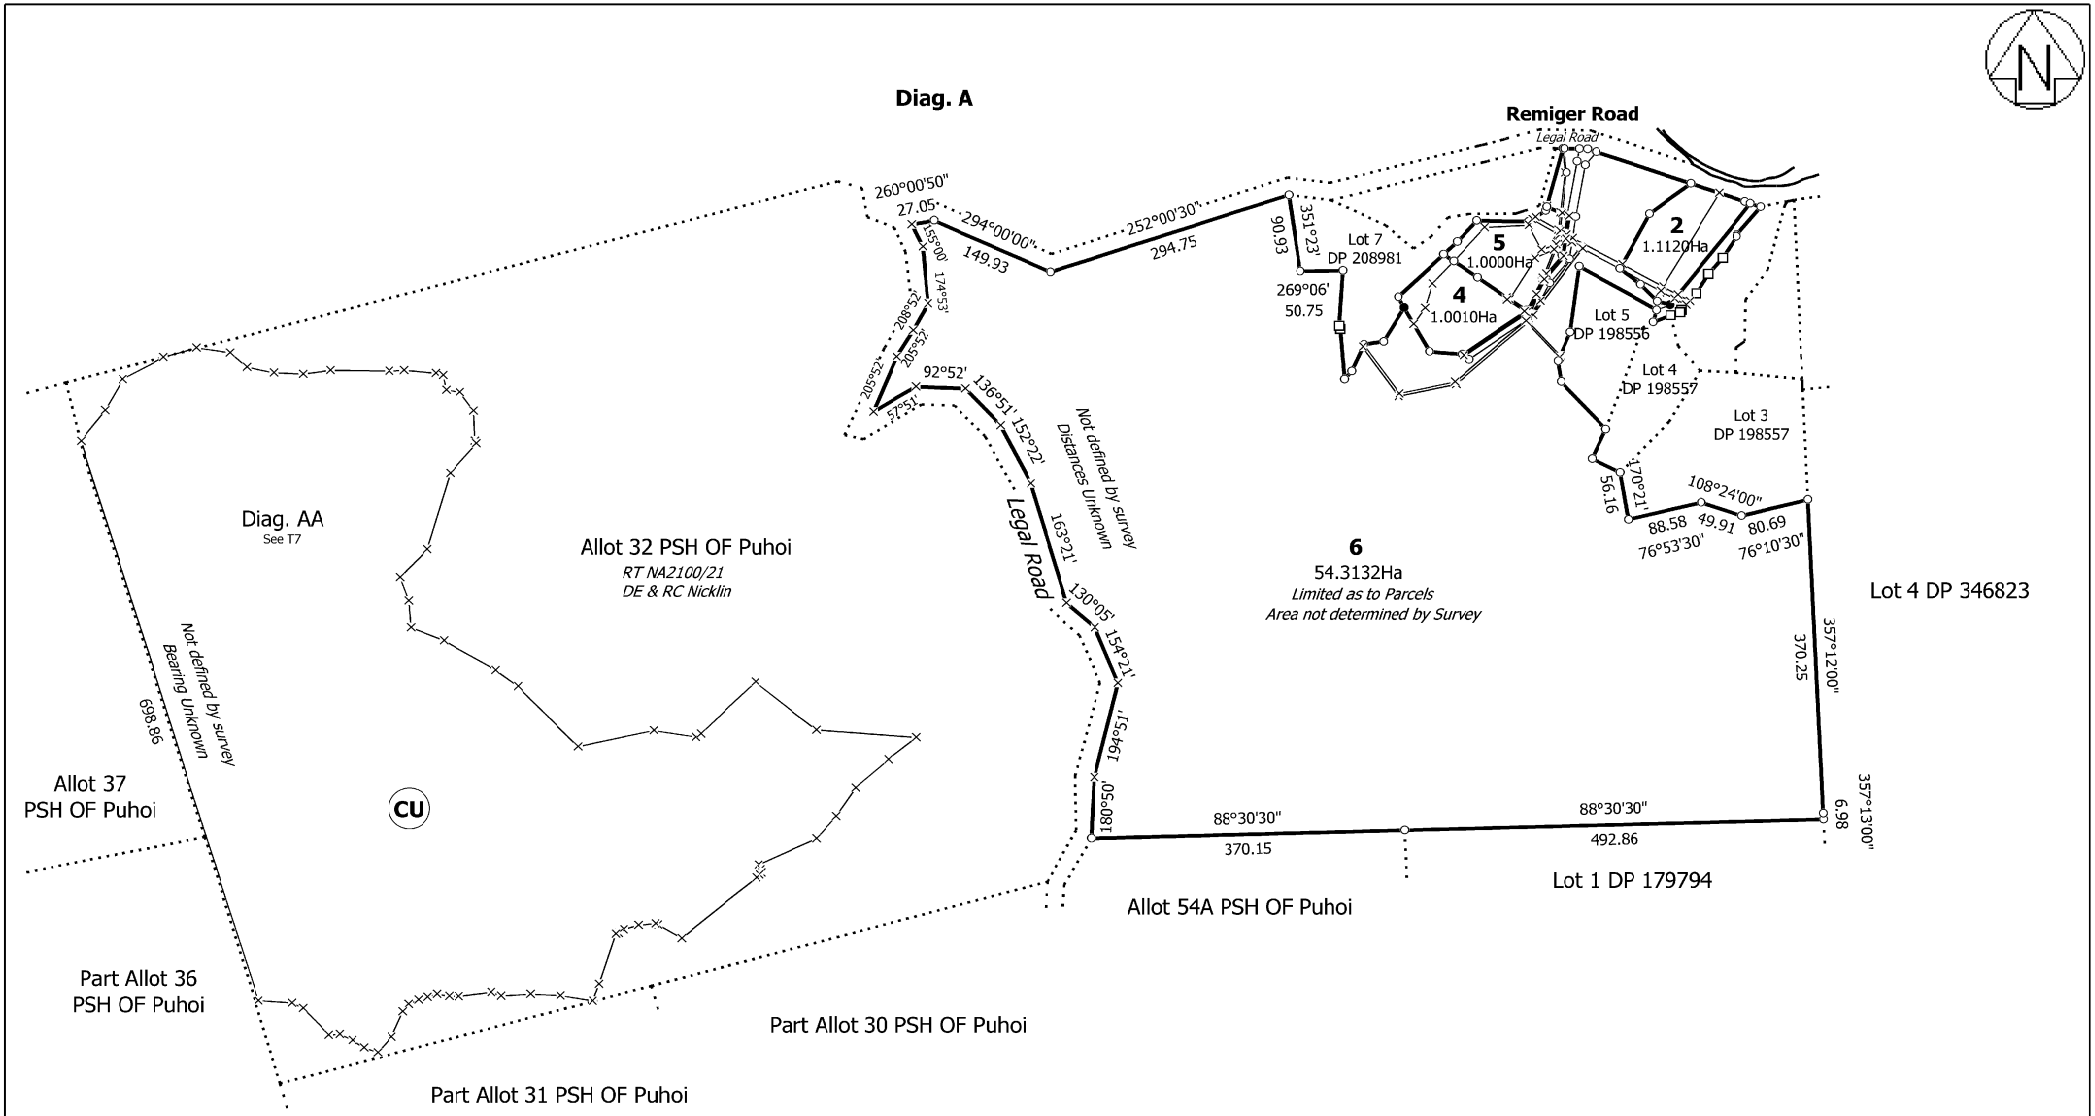


SUB 60315119
CBC File 40320 JC

T 1/7

Land District: North Auckland Digitally Generated Plan Generated on: 21/05/2020 12:27am Page 5 of 11	Lots 2, 4, 5 & 6 Being Subdivision of Lot 8 DP 208981 & Land Covenant over Allot 32 Puhoi Parish	Surveyor: Bradley Mark Mcwat Firm: Cato Bolam Consultants Ltd (Orewa)	Title Plan LT 541977 DRAFT

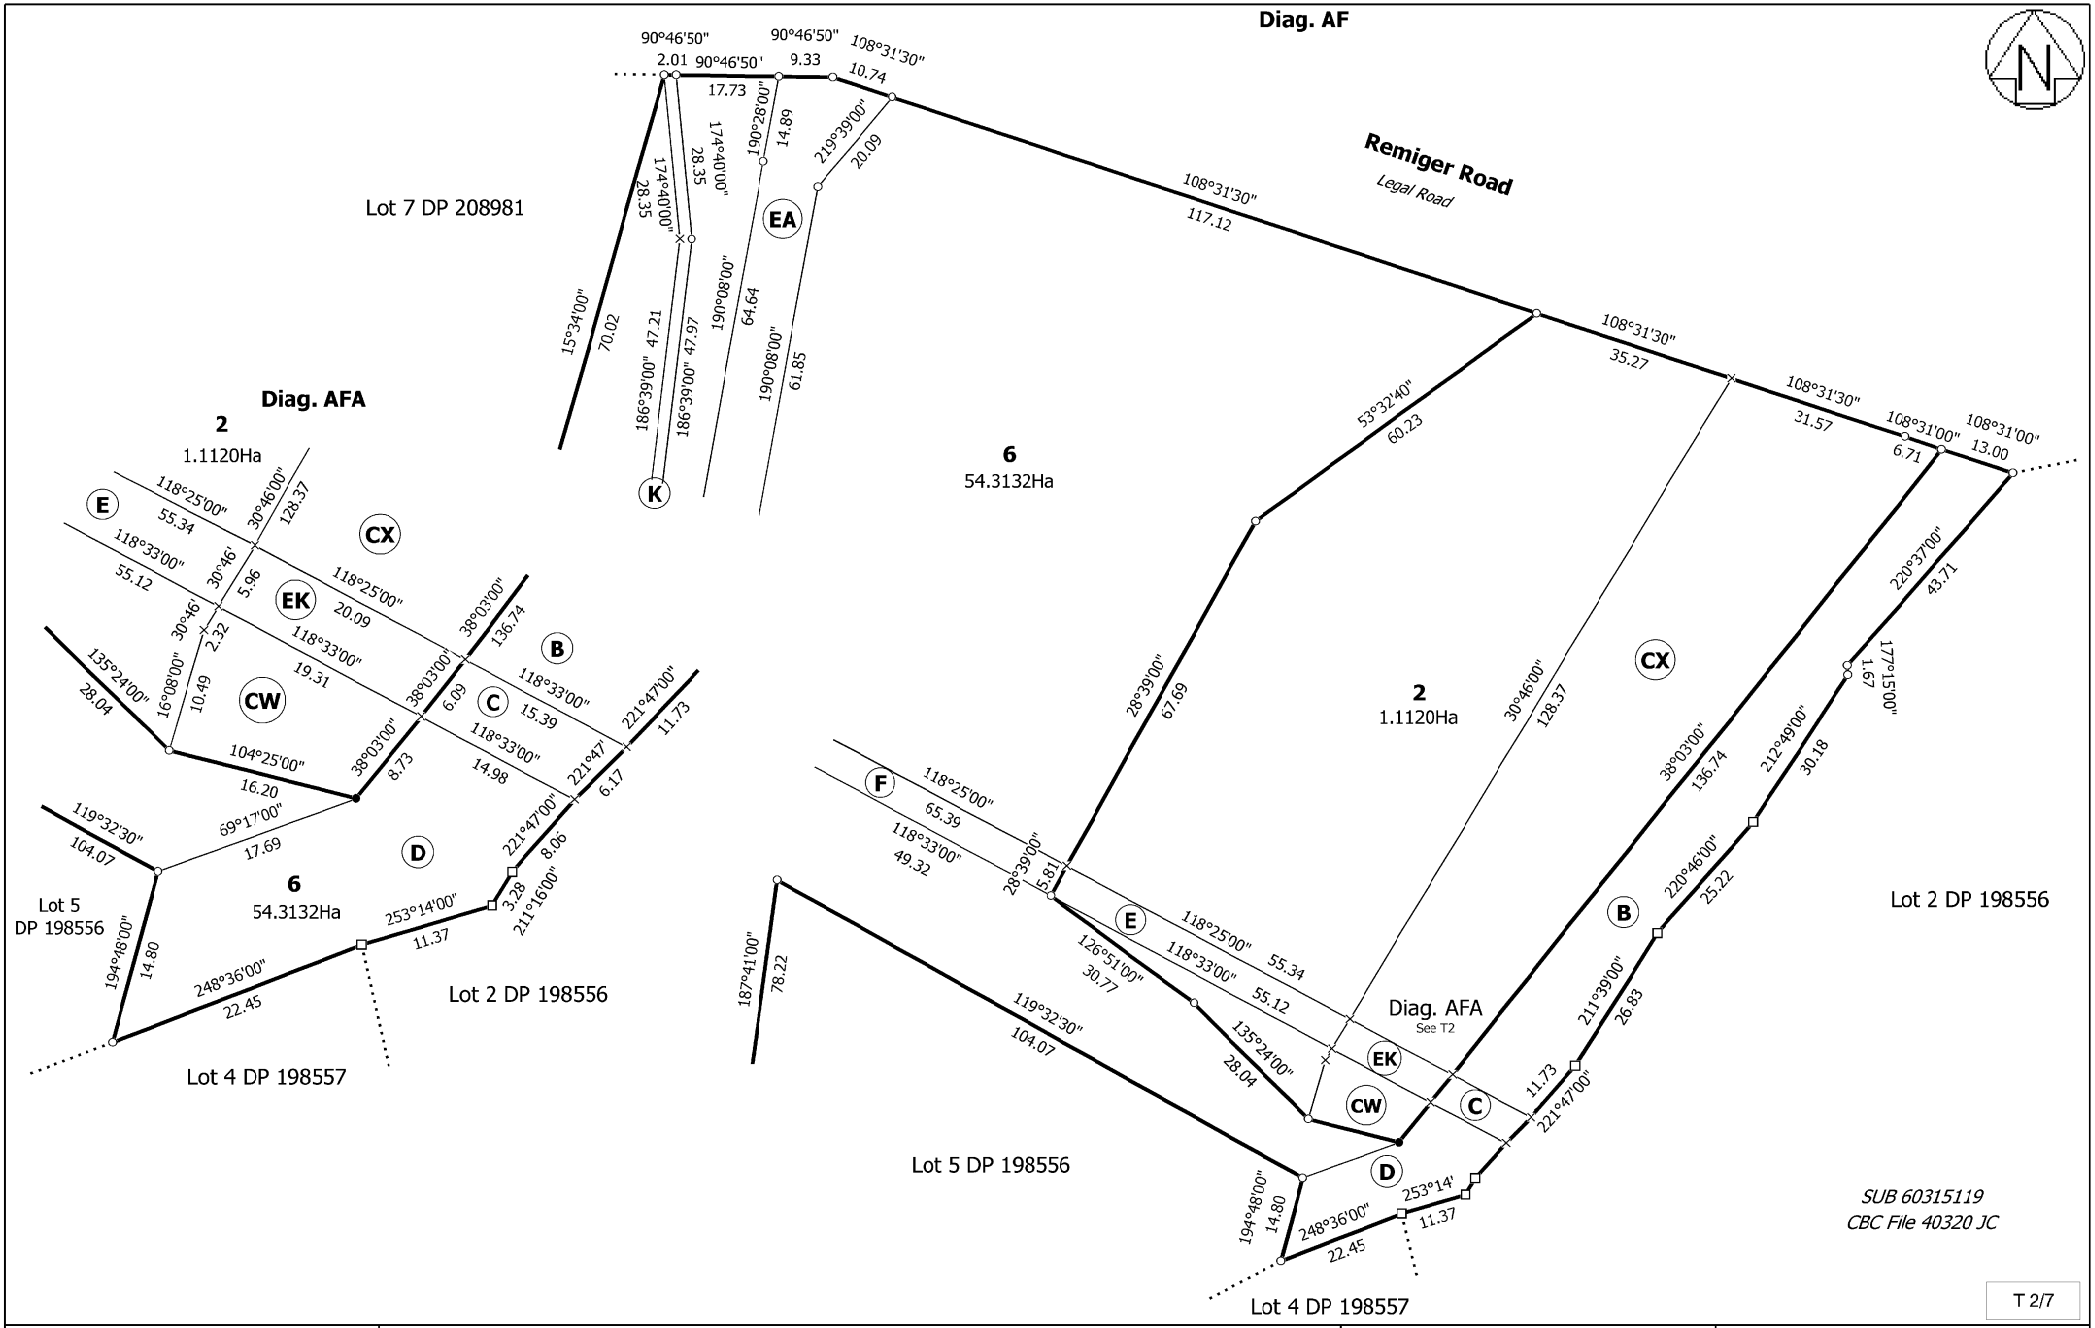


Land District: North Auckland Digitally Generated Plan Generated on: 21/05/2020 12:27am Page 6 of 11	Lots 2, 4, 5 & 6 Being Subdivision of Lot 8 DP 208981 & Land Covenant over Allot 32 Puhoi Parish	Surveyor: Bradley Mark Mcwat Firm: Cato Bolam Consultants Ltd (Orewa)	Title Plan LT 541977 DRAFT

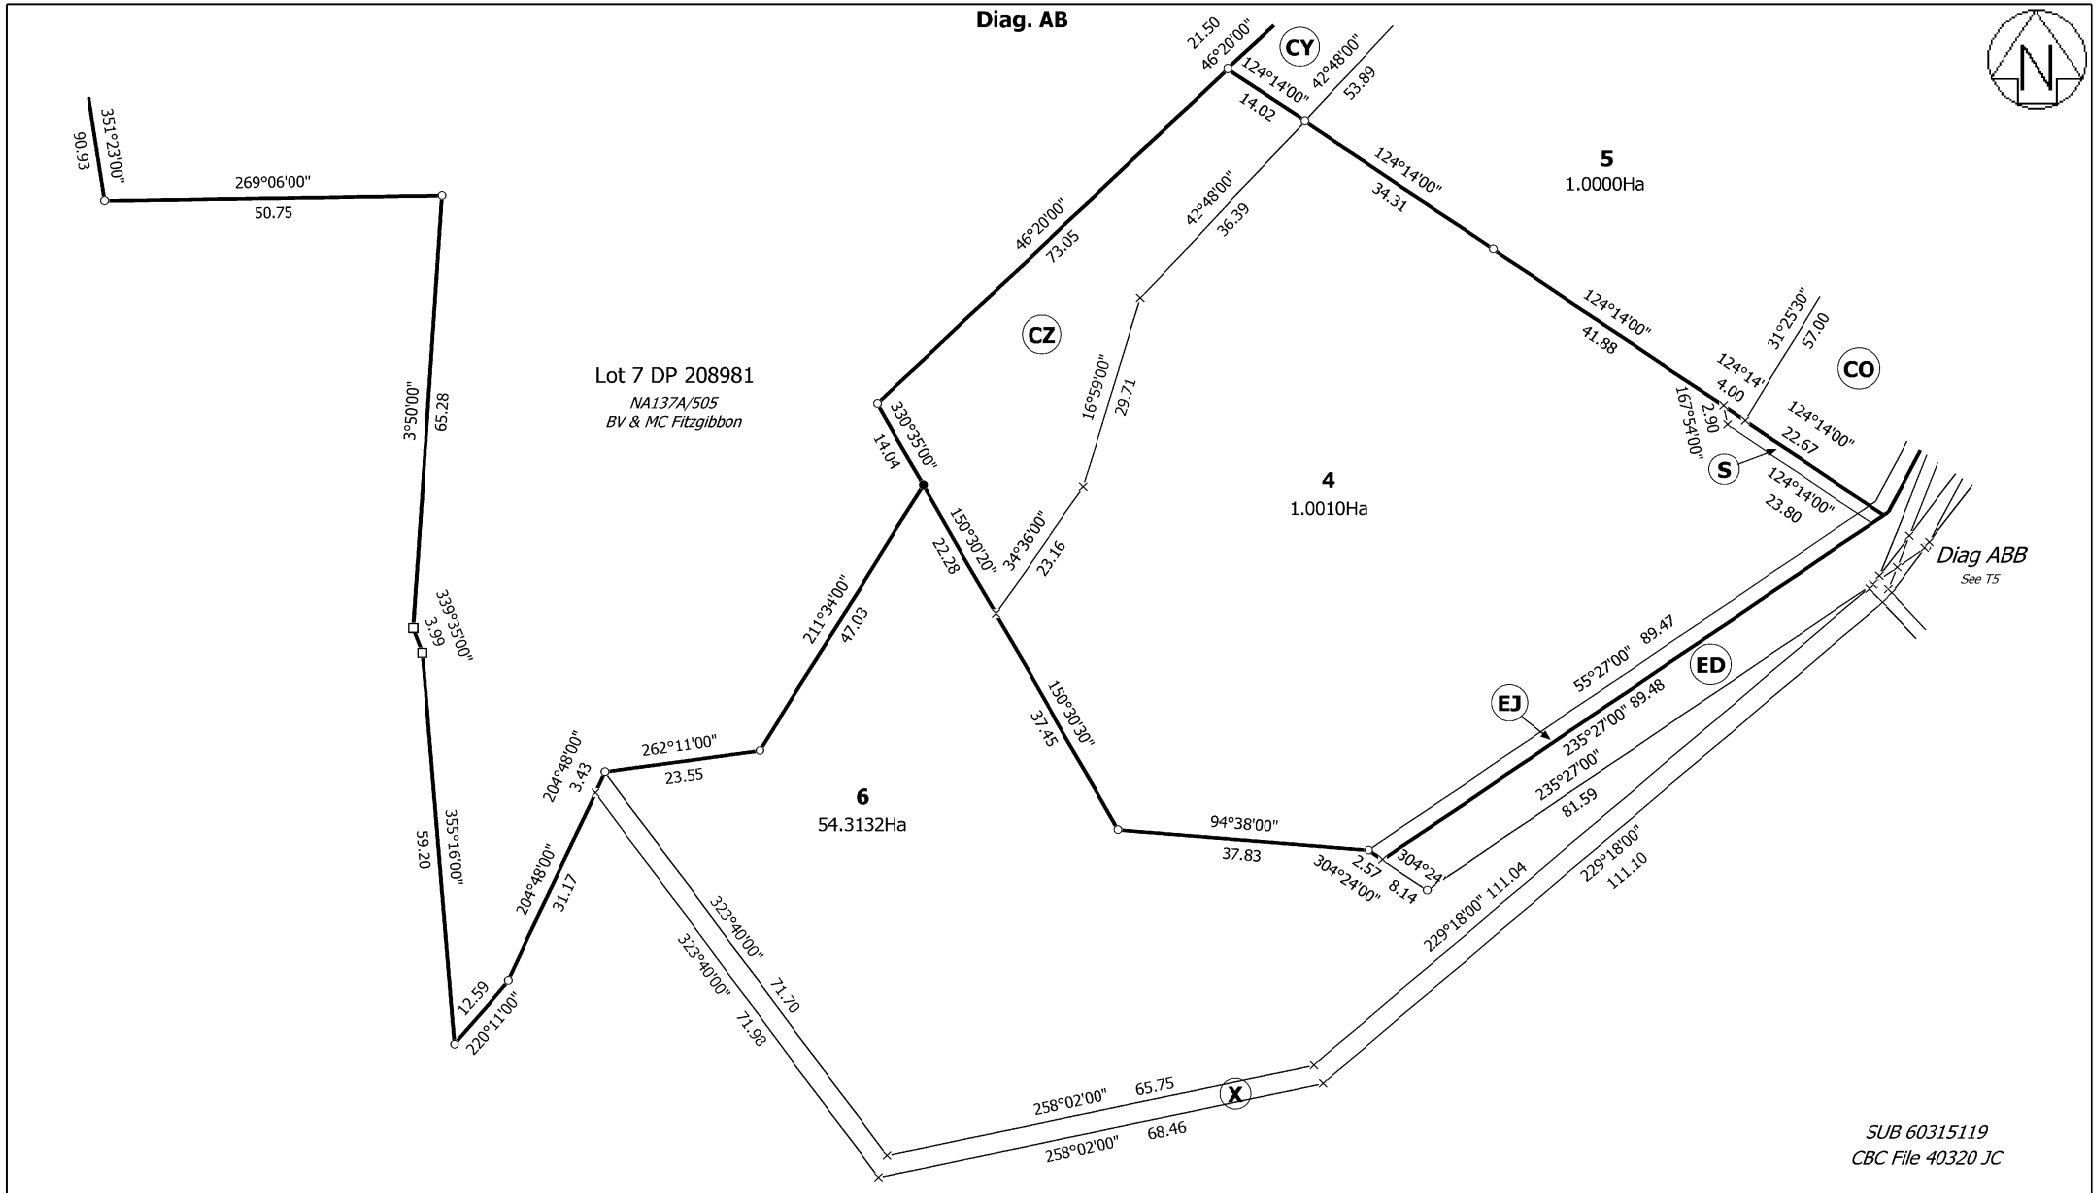

SUB 60315119
CBC File 40320 JC

T 3/7


Land District: North Auckland Digitally Generated Plan Generated on: 21/05/2020 12:27am Page 7 of 11	Lots 2, 4, 5 & 6 Being Subdivision of Lot 8 DP 208981 & Land Covenant over Allot 32 Puhoi Parish	Surveyor: Bradley Mark Mcwat Firm: Cato Bolam Consultants Ltd (Orewa)	Title Plan LT 541977 DRAFT

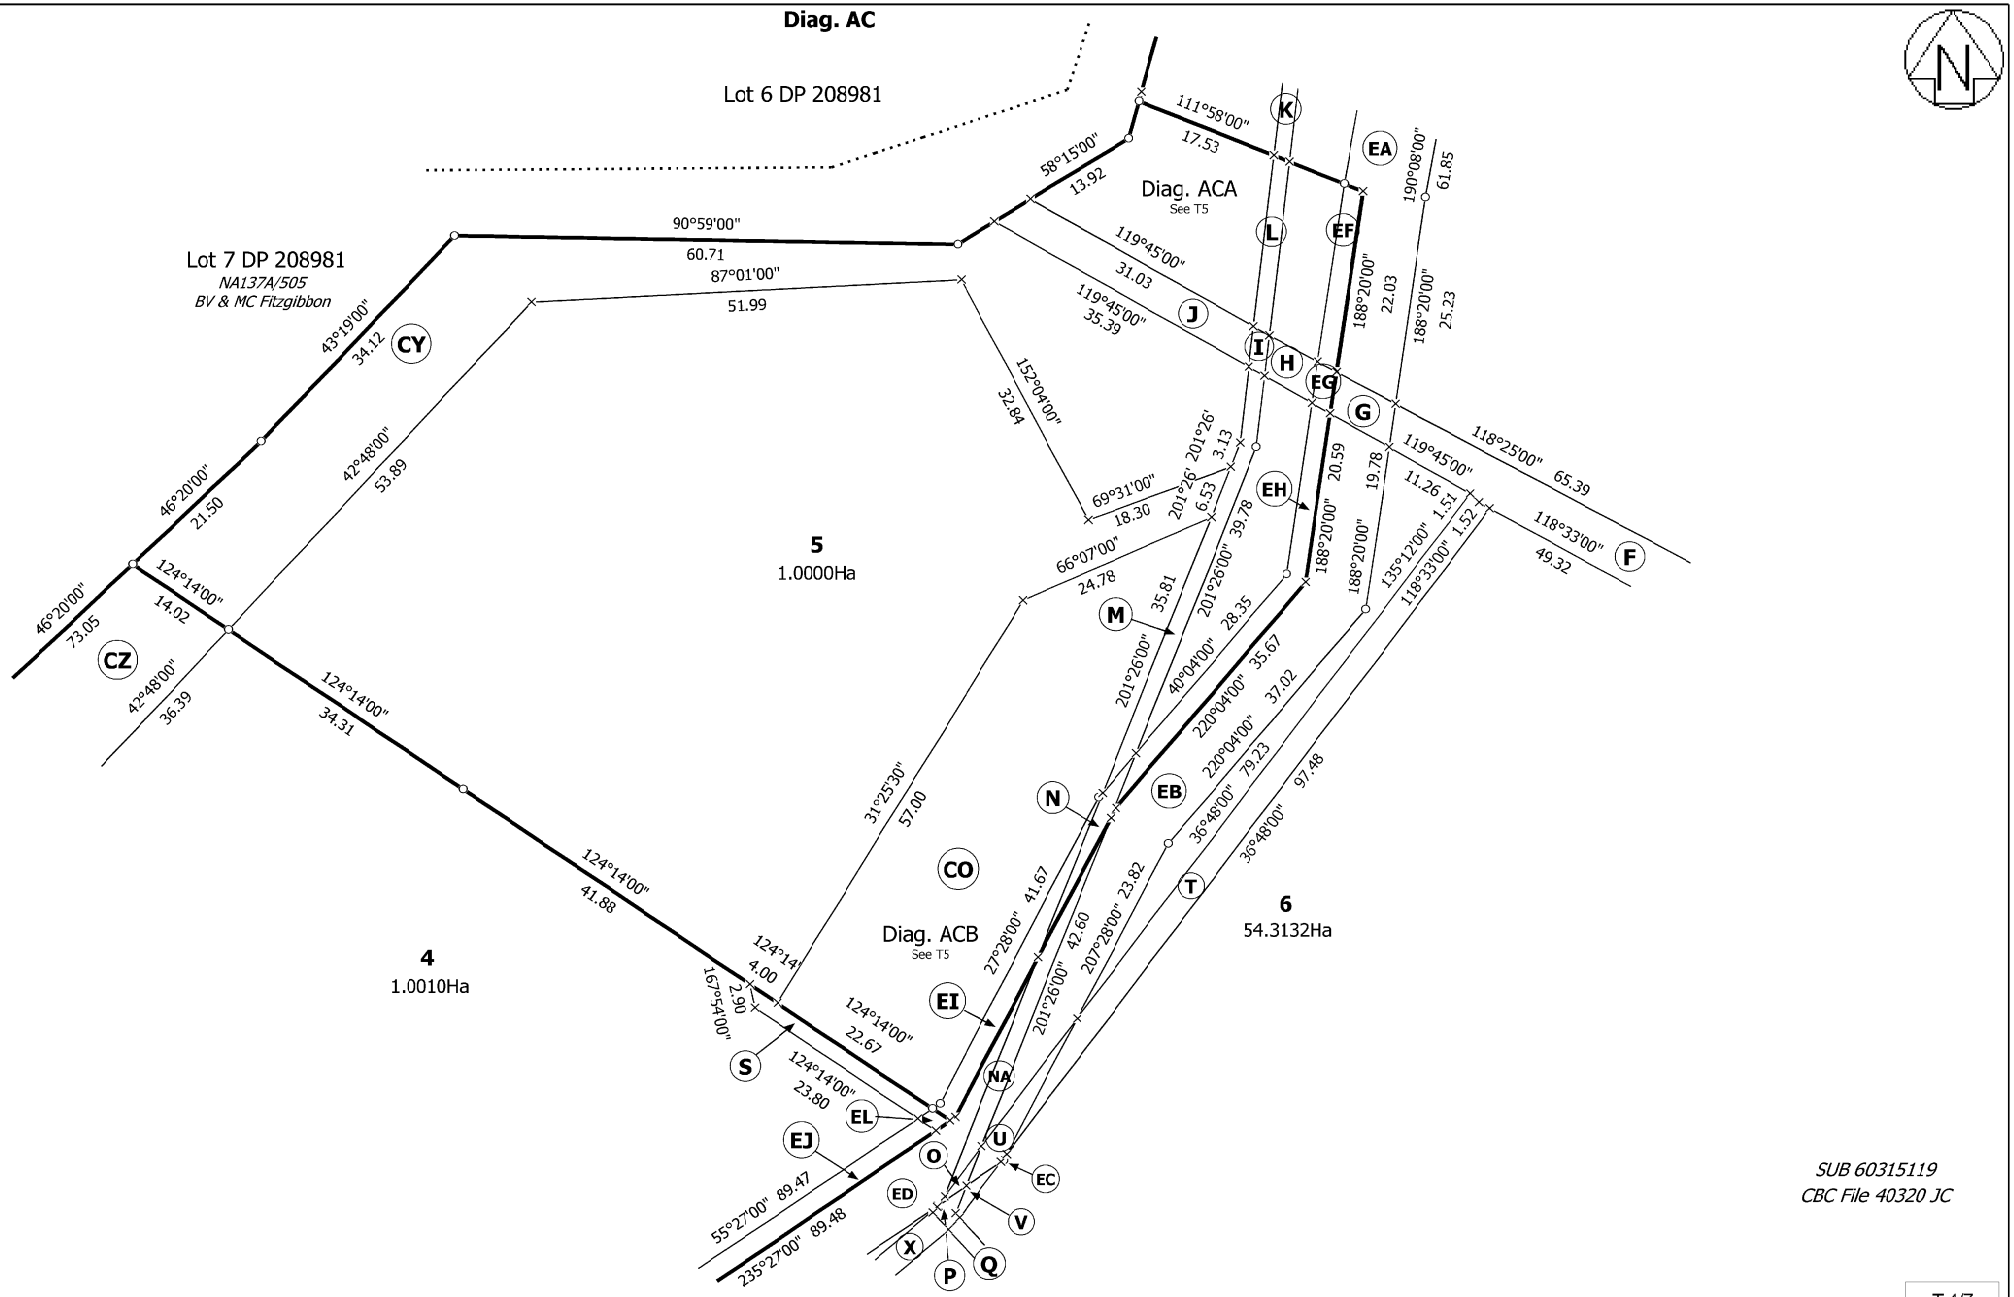


SUB 60315119
CBC File 40320 JC

T 4/7

Land District: North Auckland Digitally Generated Plan Generated on: 21/05/2020 12:27am Page 8 of 11	Lots 2, 4, 5 & 6 Being Subdivision of Lot 8 DP 208981 & Land Covenant over Allot 32 Puhoi Parish	Surveyor: Bradley Mark Mcwat Firm: Cato Bolam Consultants Ltd (Orewa)	Title Plan LT 541977 DRAFT

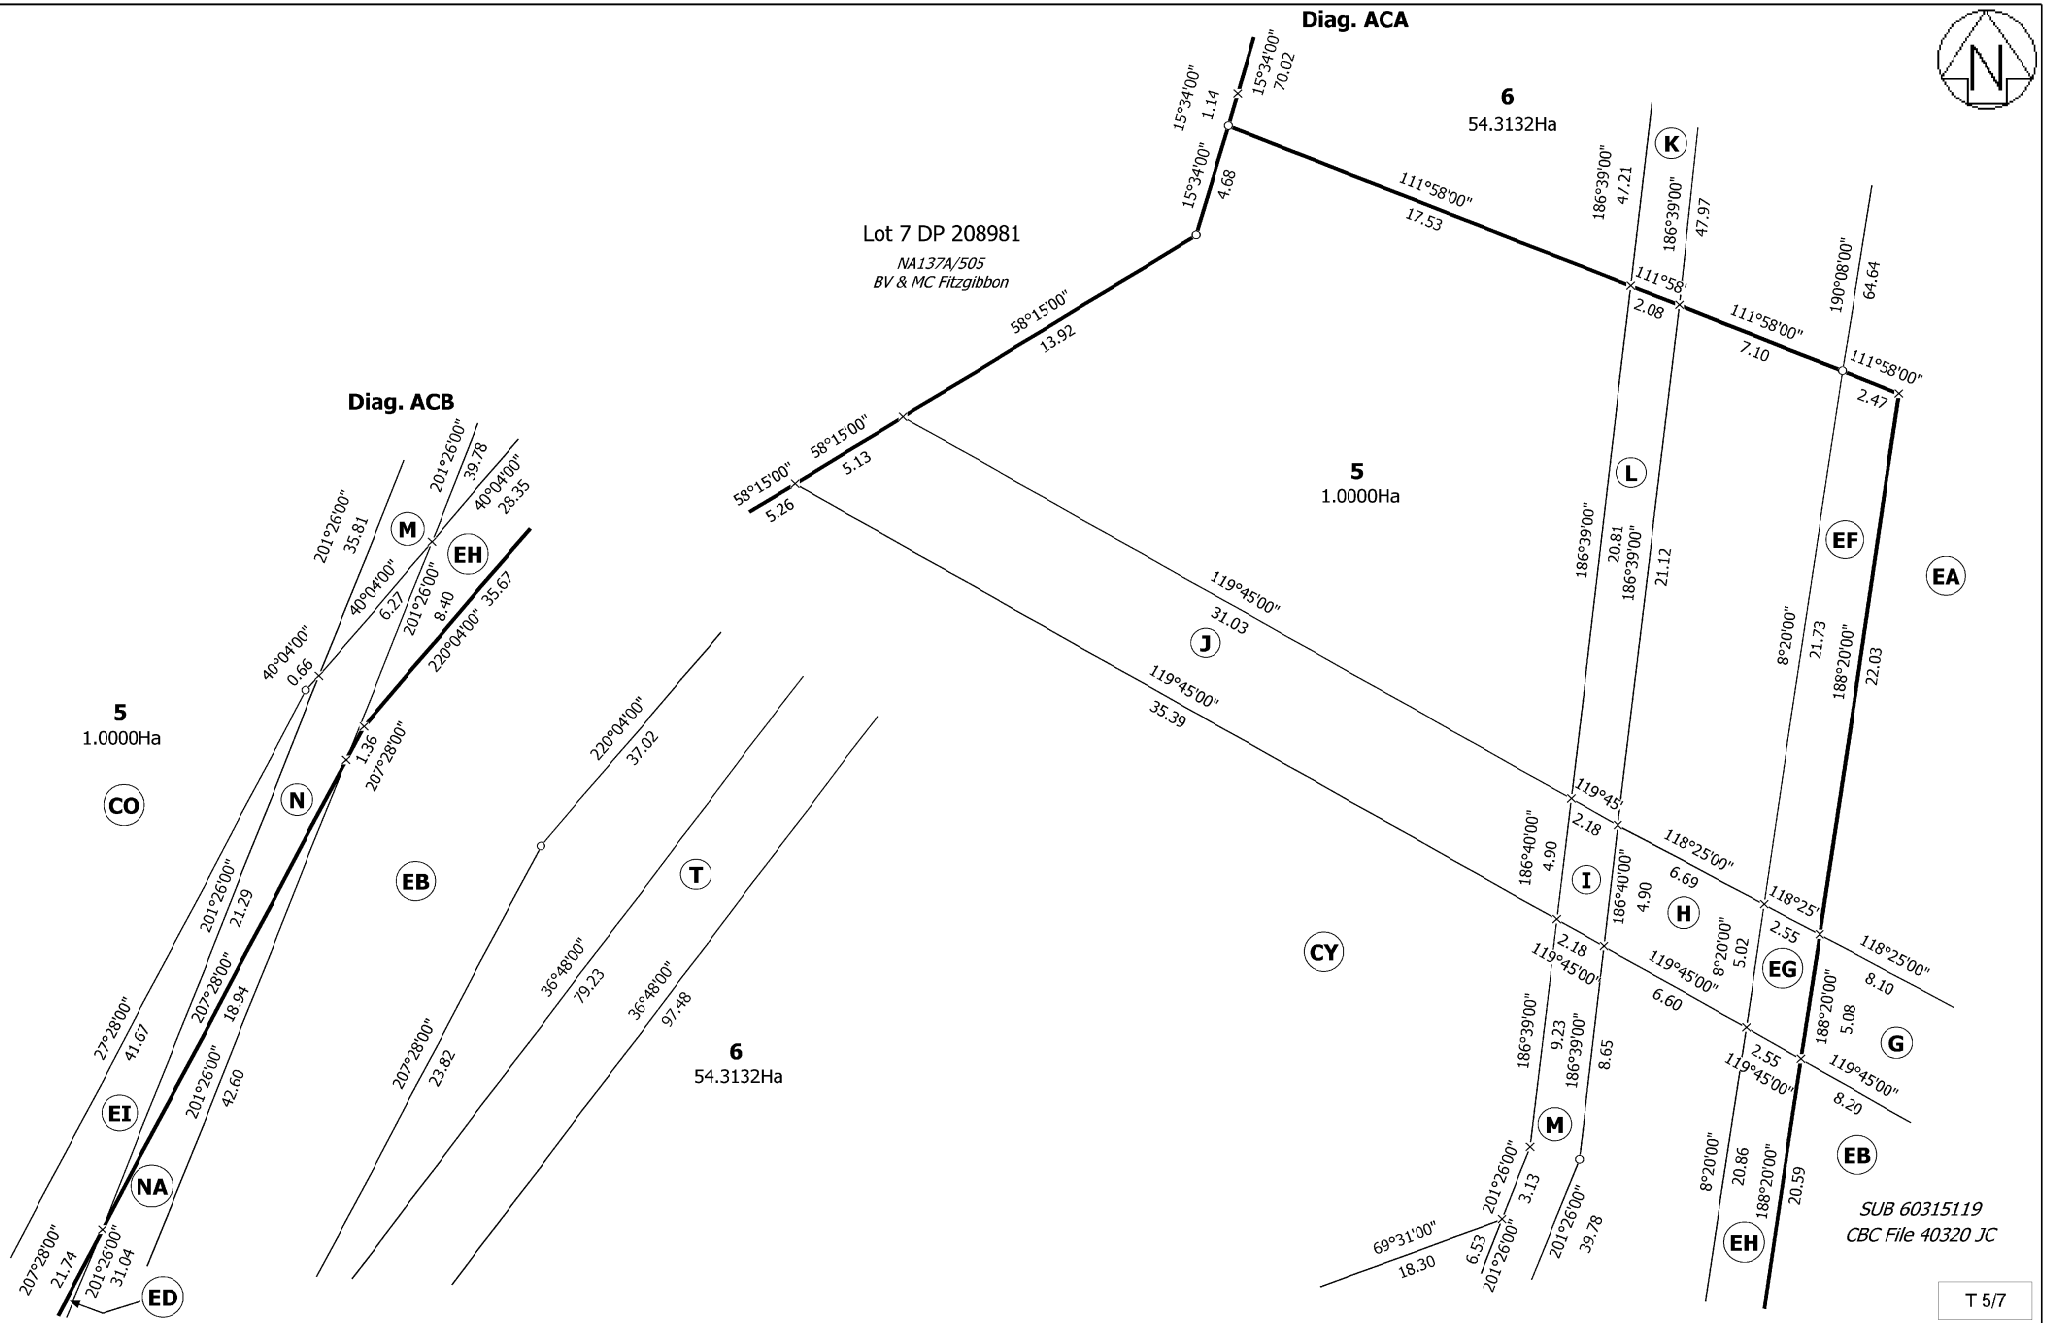


Land District: North Auckland Digitally Generated Plan Generated on: 21/05/2020 12:27am Page 9 of 11	Lots 2, 4, 5 & 6 Being Subdivision of Lot 8 DP 208981 & Land Covenant over Allot 32 Puhoi Parish	Surveyor: Bradley Mark Mcwat Firm: Cato Bolam Consultants Ltd (Orewa)	Title Plan LT 541977 DRAFT

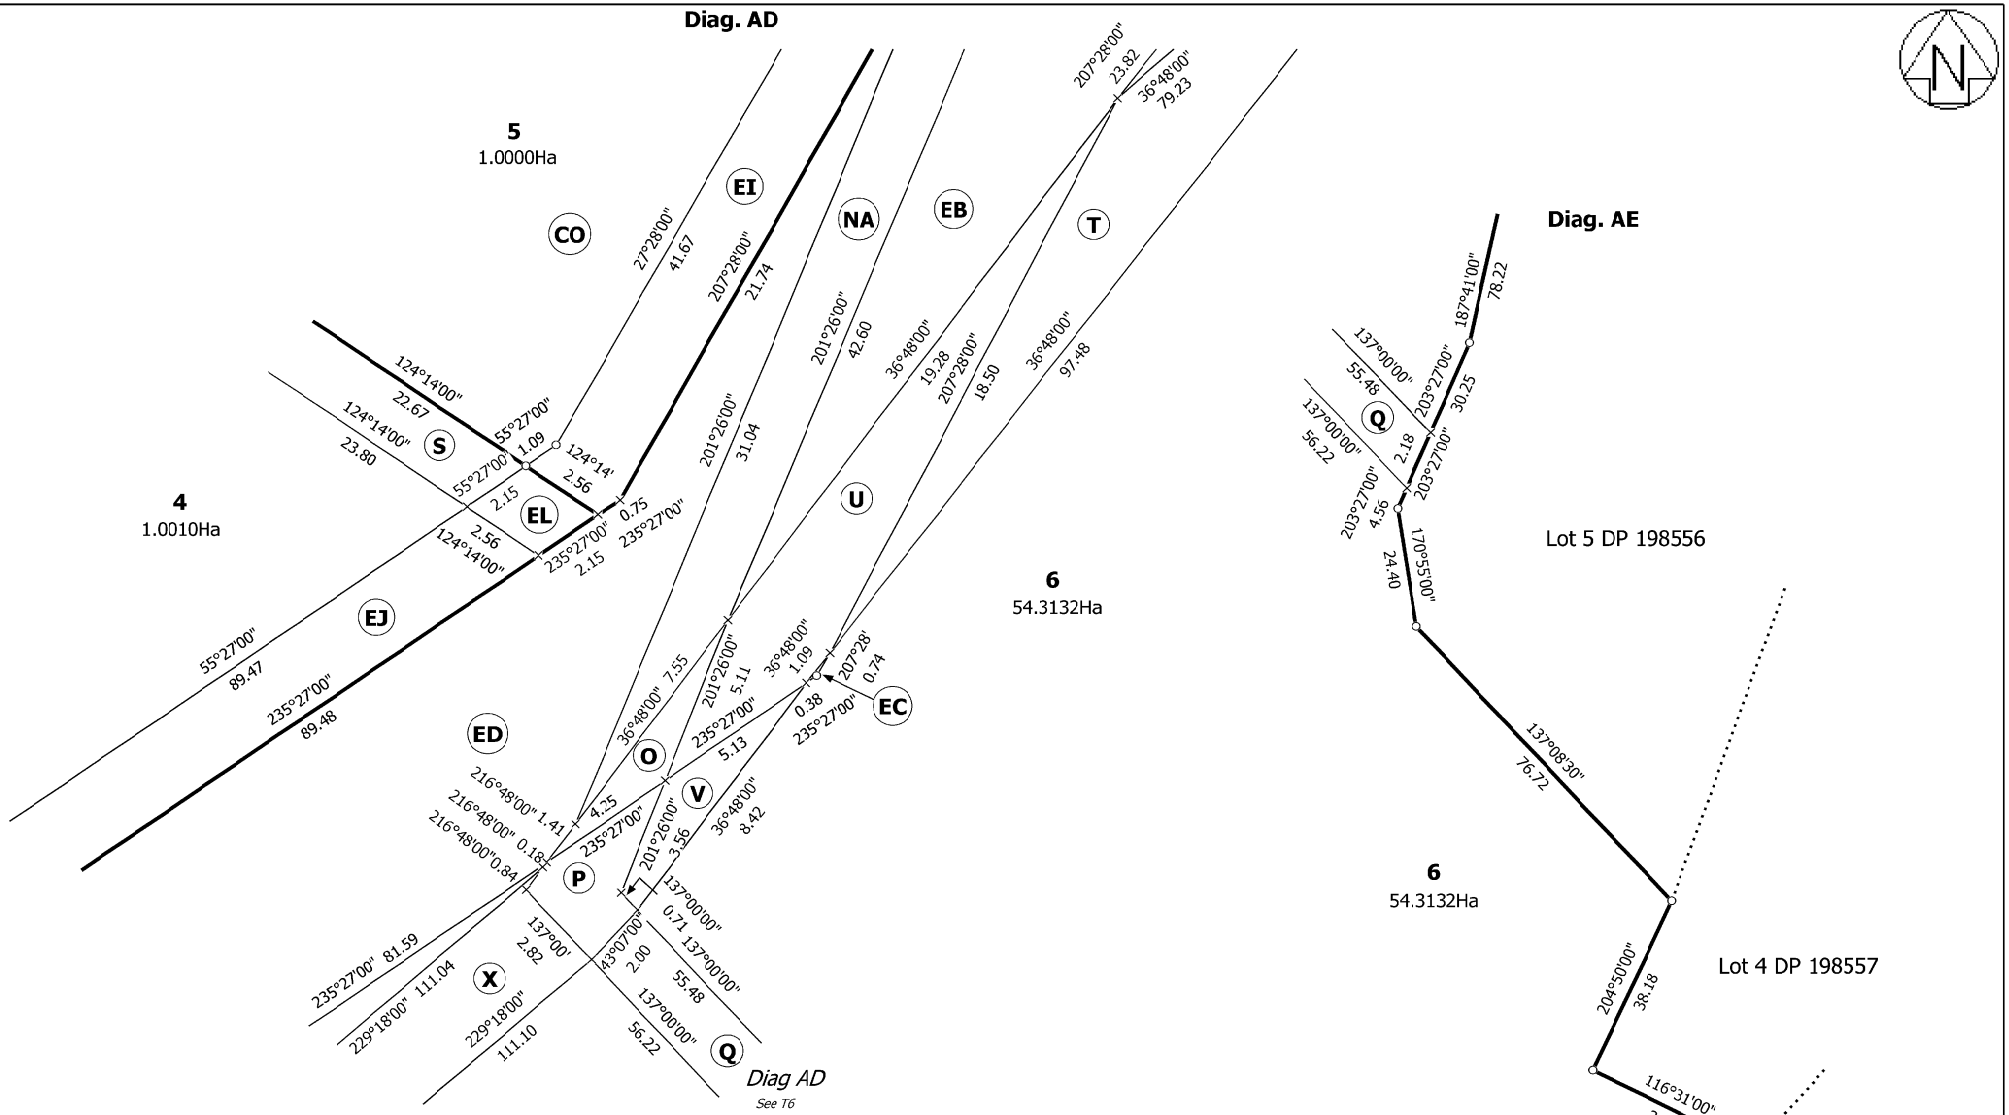


T 6/7

Land District: North Auckland Digitally Generated Plan Generated on: 21/05/2020 12:27am Page 10 of 11	Lots 2, 4, 5 & 6 Being Subdivision of Lot 8 DP 208981 & Land Covenant over Allot 32 Puhoi Parish	Surveyor: Bradley Mark Mcwat Firm: Cato Bolam Consultants Ltd (Orewa)	Title Plan LT 541977 DRAFT

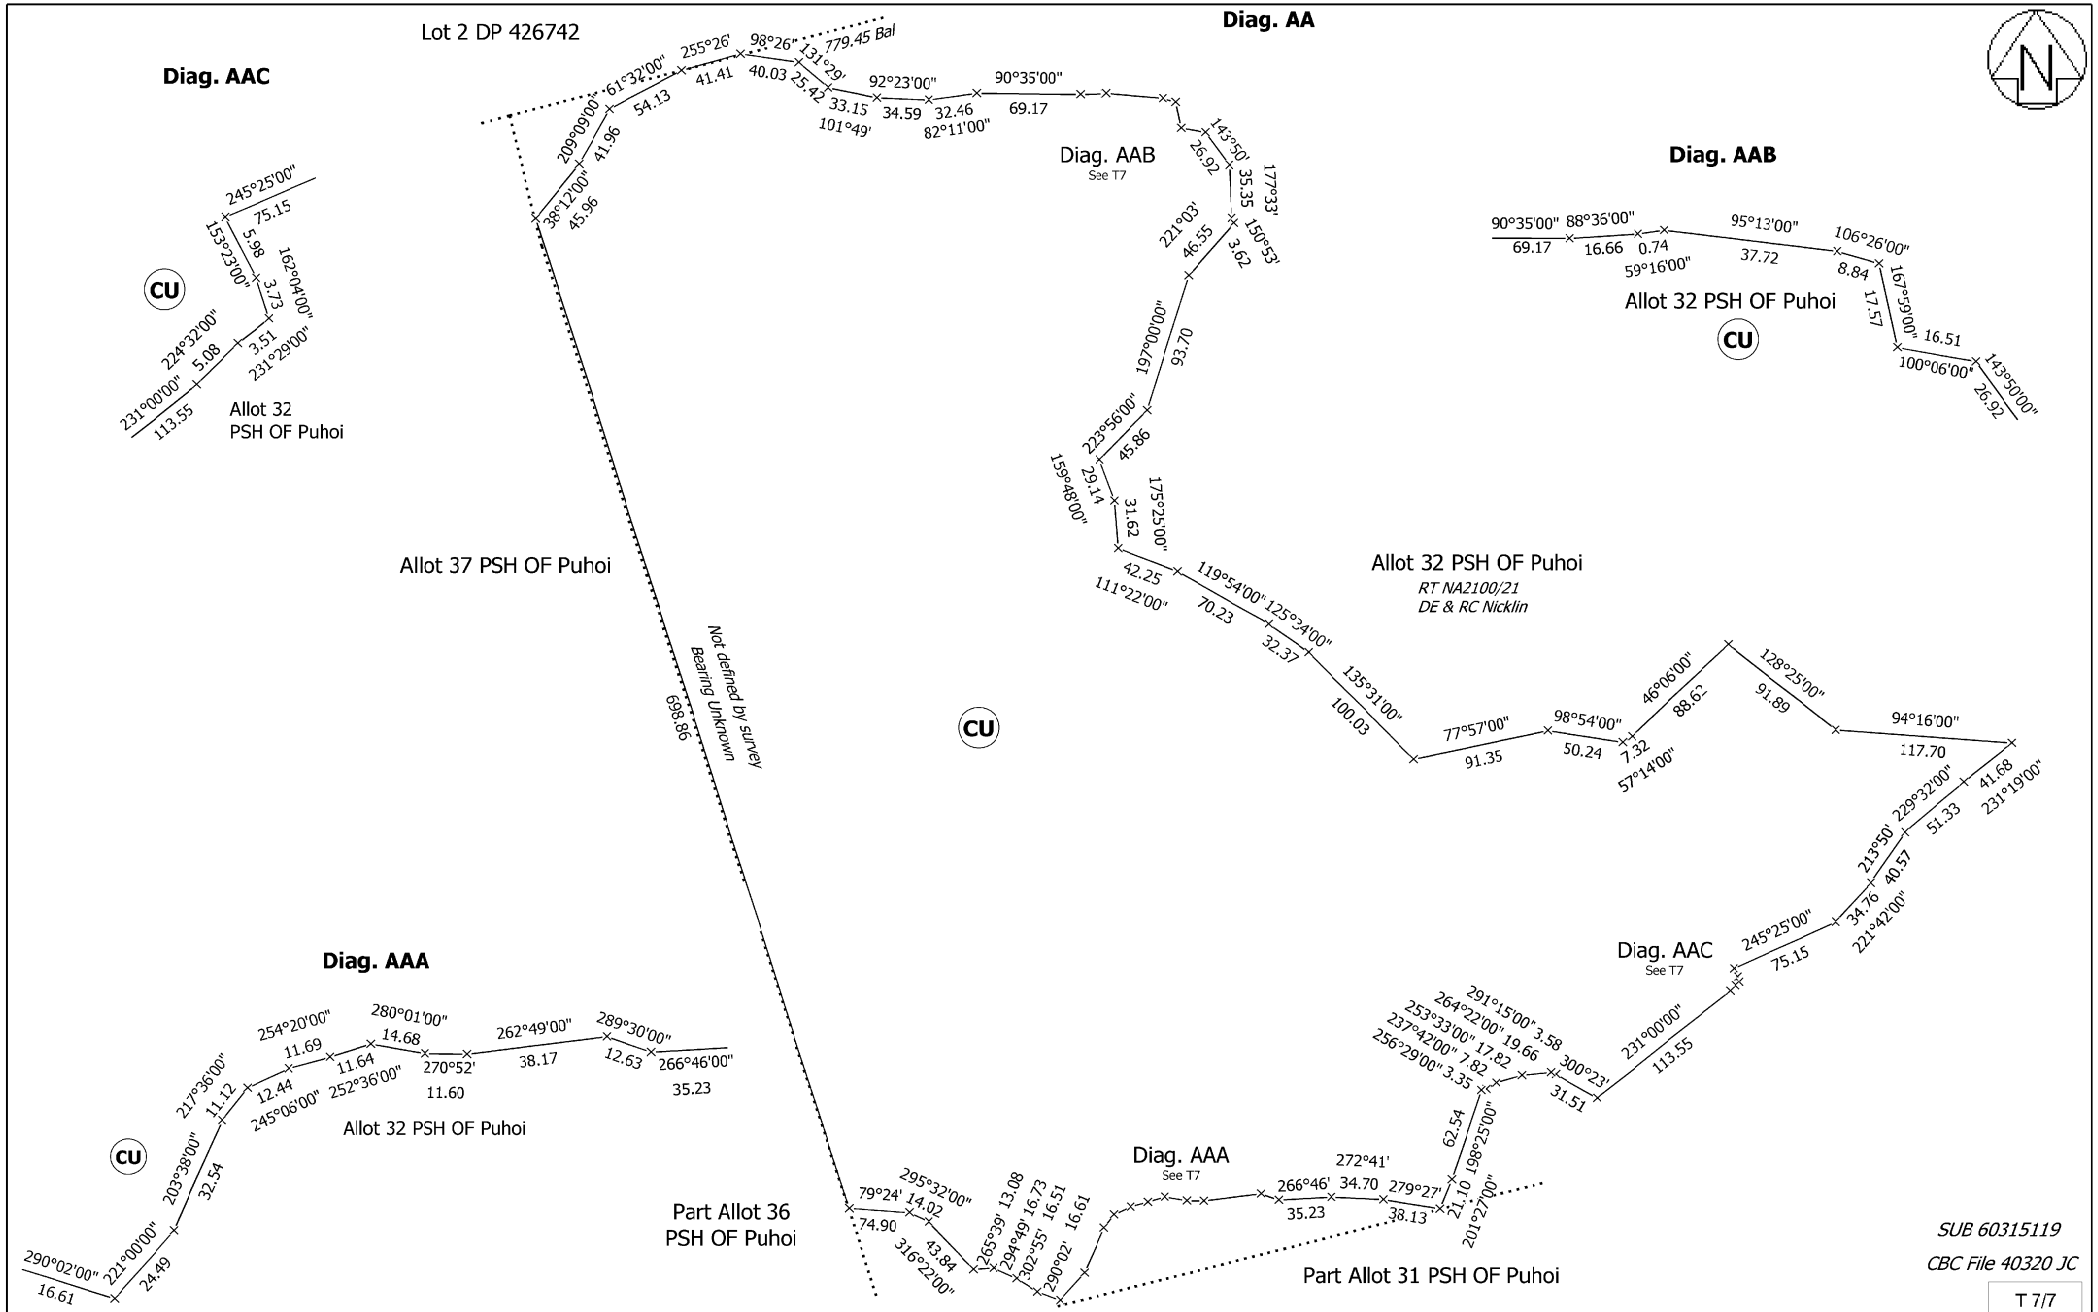

Land District: North Auckland Digitally Generated Plan Generated on: 21/05/2020 12:27am Page 11 of 11	Lots 2, 4, 5 & 6 Being Subdivision of Lot 8 DP 208981 & Land Covenant over Allot 32 Puhoi Parish	Surveyor: Bradley Mark Mcwat Firm: Cato Bolam Consultants Ltd (Orewa)	Title Plan LT 541977 DRAFT

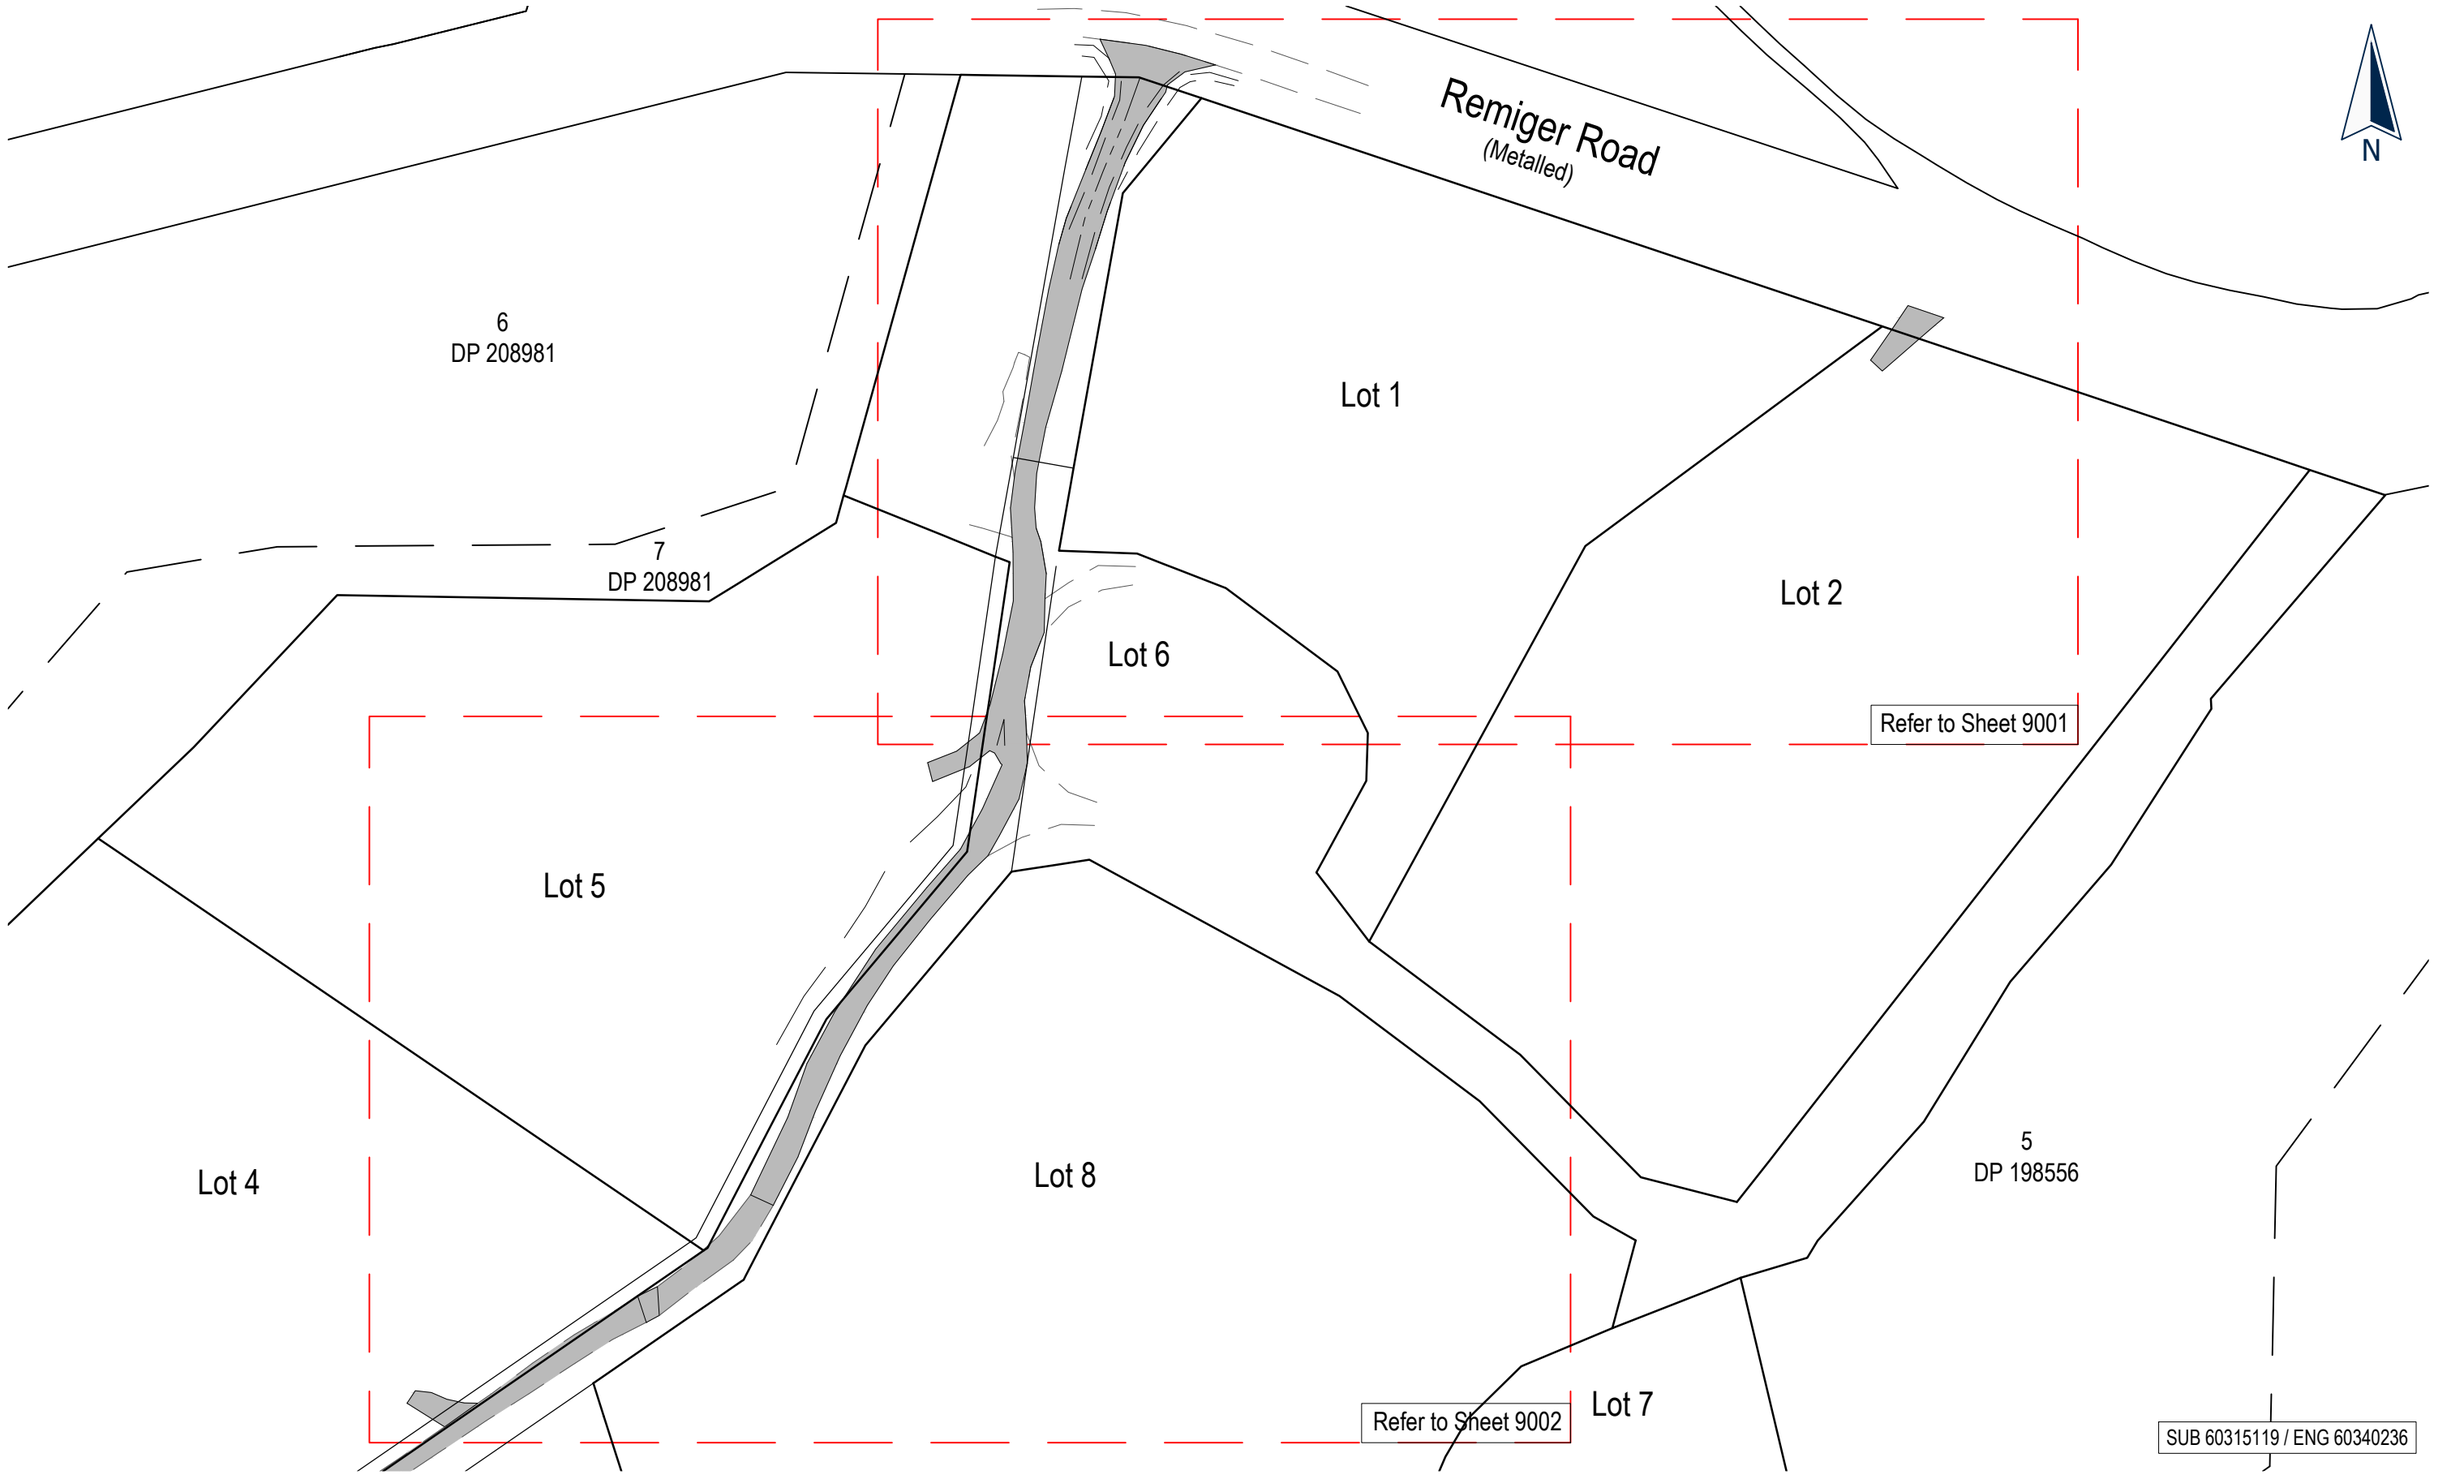

Cato Bolam
creating great places
PLANNERS | SURVEYORS | ENGINEERS
ARCHITECTS | ENVIRONMENTAL

This drawing and design remains the property of, and may not be reproduced or amended without the written permission of Cato Bolam Consultants Ltd. No liability shall be accepted for unauthorised use of this drawing and design.


R.&D. Nicklin
53B Remiger Road
Puhoi

Right of Way As Built Plan
Sheet 1 of 3

No.	REVISION (DESCRIPTIONS)	NAME	DATE
0	Issued for Completion	TL	28/04/2021

FOR COMPLETION

		NAME	DATE
SURVEYED		LD	17/08/2020
DESIGNED			
DRAWN		LD	28/04/2021
DATE	ORIGINAL SCALE	ORIGINAL SIZE	
28/04/2021	1:1000	A3	
DRAWING NO.		REVISION	
40320-DR-SU-9000		0	

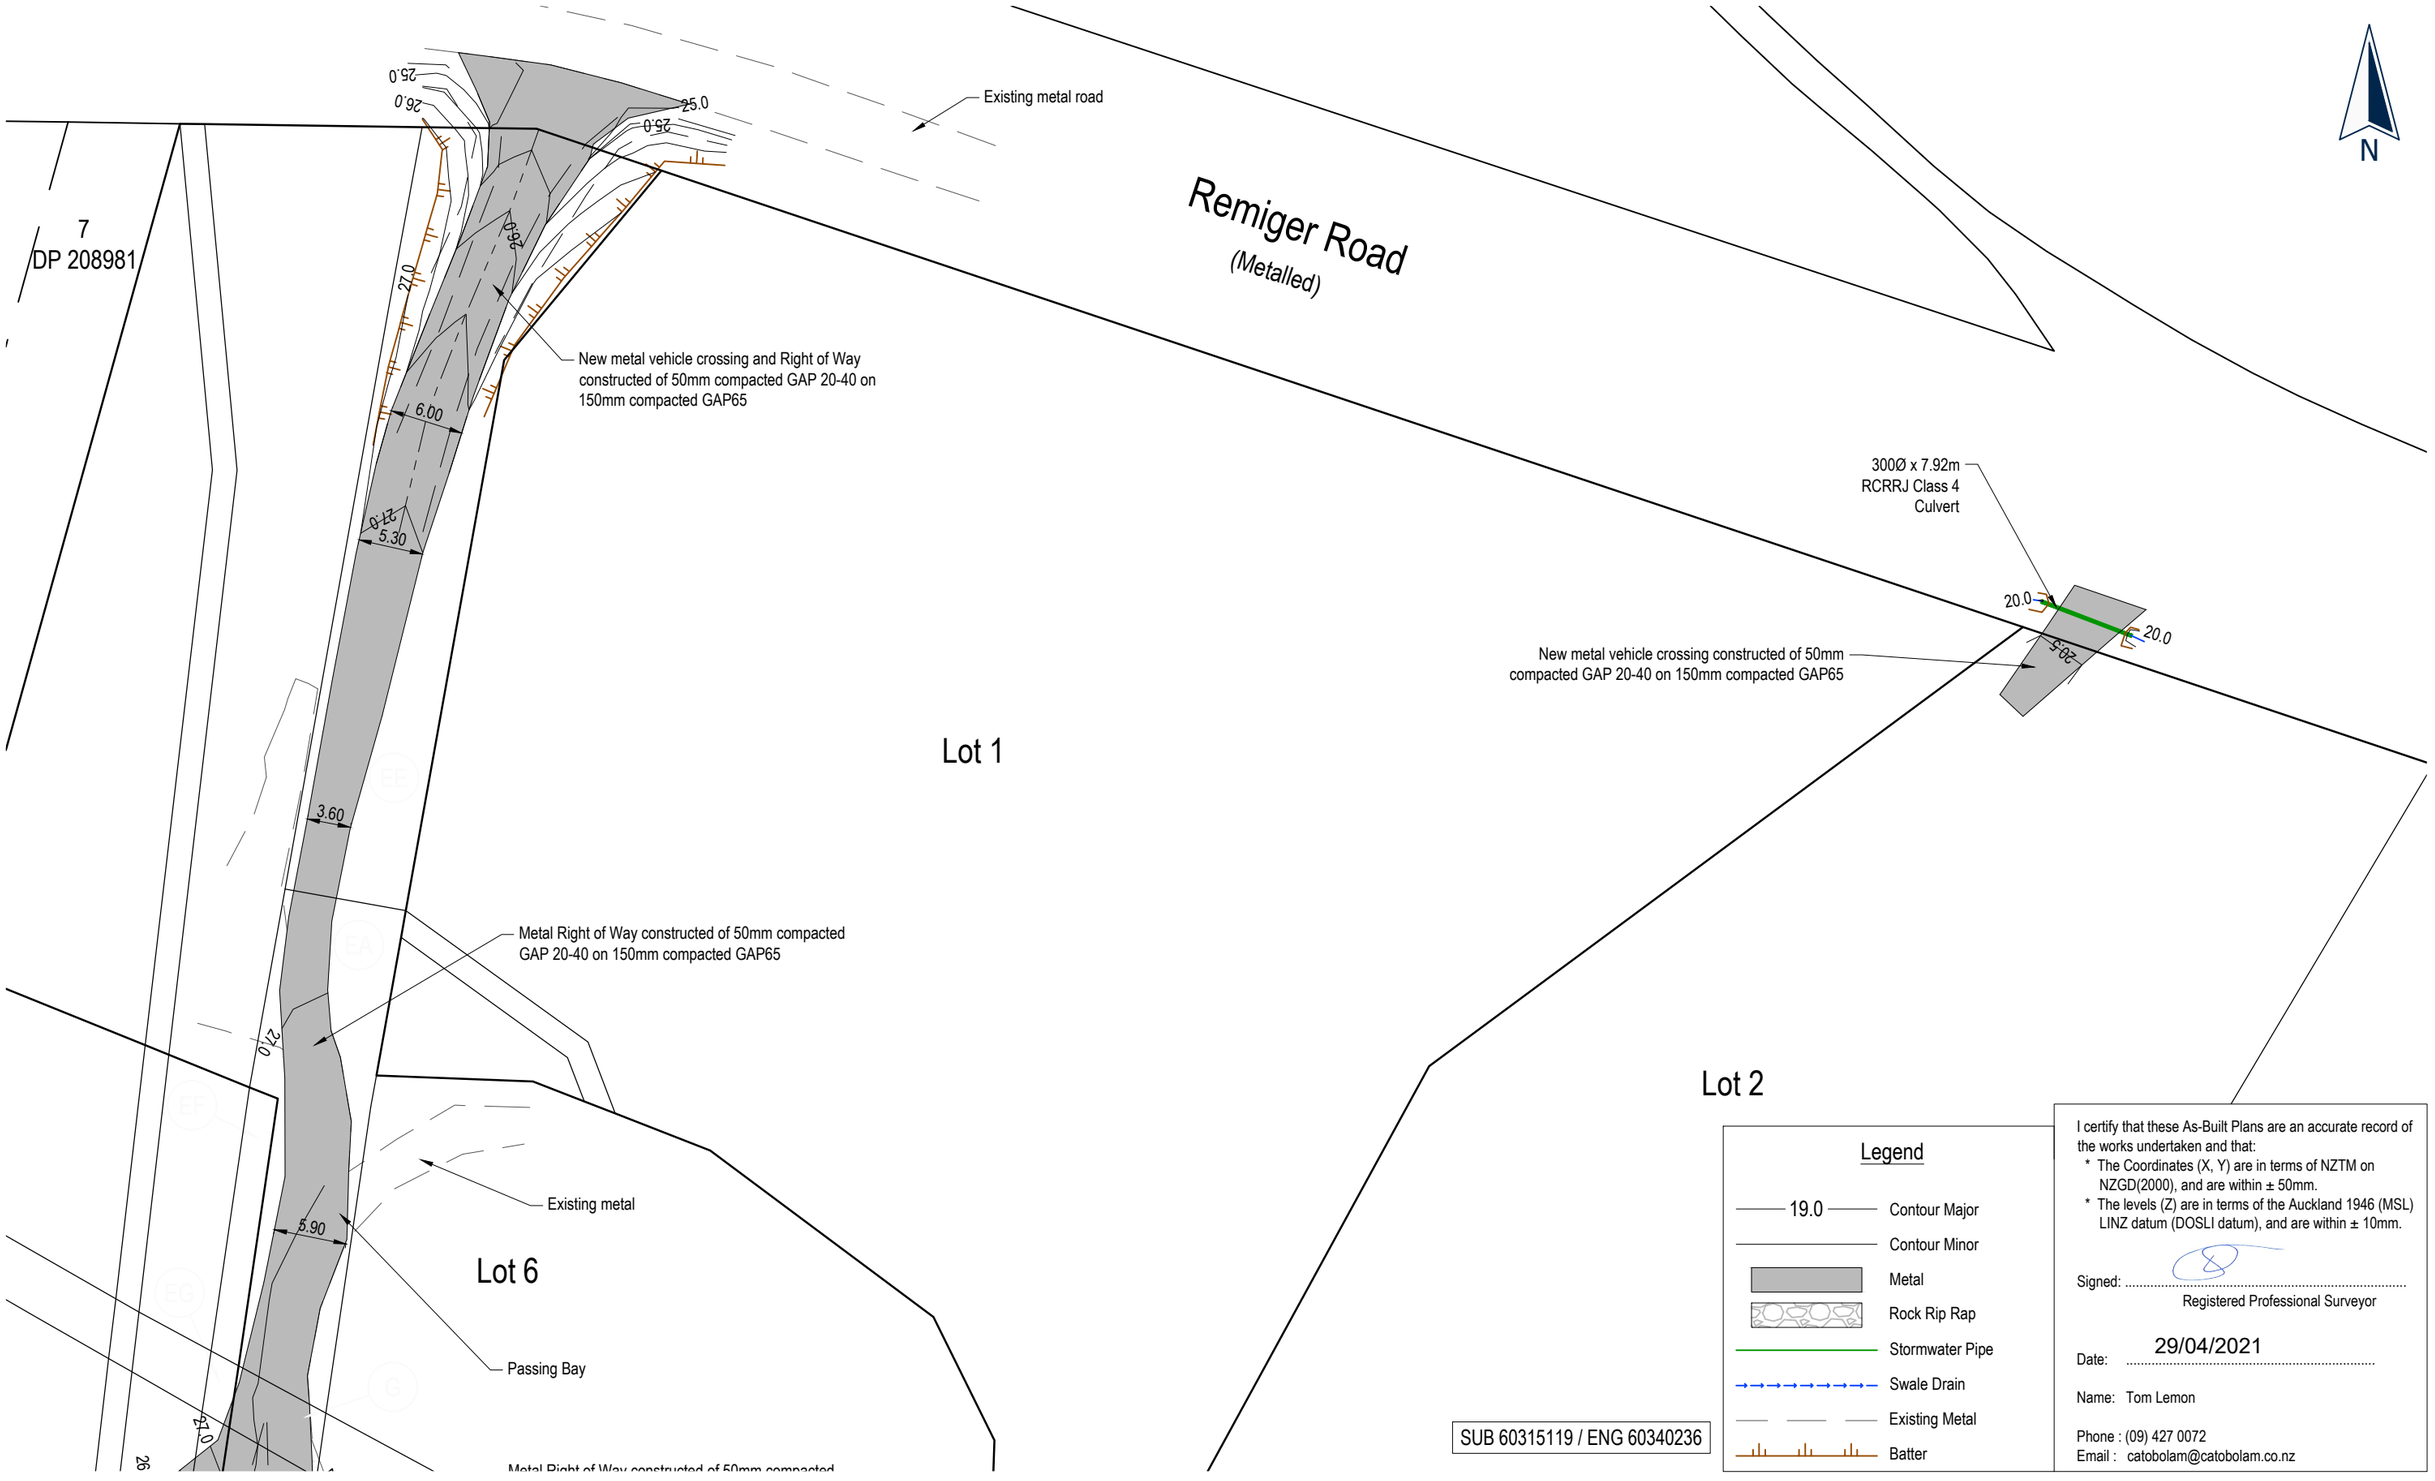

SUB 60315119 / ENG 60340236

Legend

- 19.0 — Contour Major
- Contour Minor
- Metal
- Rock Rip Rap
- Stormwater Pipe
- Swale Drain
- Existing Metal
- Batter

I certify that these As-Built Plans are an accurate record of the works undertaken and that:

* The Coordinates (X, Y) are in terms of NZTM on NZGD(2000), and are within ± 50mm.
* The levels (Z) are in terms of the Auckland 1946 (MSL) LINZ datum (DOSLI datum), and are within ± 10mm.

Signed: .....
Registered Professional Surveyor

Date: 29/04/2021

Name: Tom Lemon

Phone : (09) 427 0072
Email : catobolam@catobolam.co.nz

Cato Bolam
creating great places
PLANNERS | SURVEYORS | ENGINEERS
ARCHITECTS | ENVIRONMENTAL

The contours on this plan have been derived from the spot levels shown. Any ground levels used in critical design locations should be checked against the spot levels and confirmed by further survey if necessary.

This drawing and design remains the property of, and may not be reproduced or amended without the written permission of Cato Bolam Consultants Ltd. No liability shall be accepted for unauthorised use of this drawing and design.


R. & D. Nicklin
53B Remiger Road
Puhoi

Right of Way As Built Plan
Sheet 2 of 3

No.	REVISION (DESCRIPTIONS)	NAME	DATE
0	Issued for Completion	TL	28/04/2021

FOR COMPLETION

		NAME	DATE
SURVEYED		LD	17/08/2020
DESIGNED			
DRAWN		LD	28/04/2021
DATE	ORIGINAL SCALE	ORIGINAL SIZE	
28/04/2021	1:500	A3	
DRAWING NO.		REVISION	
40320-DR-SU-9001		0	

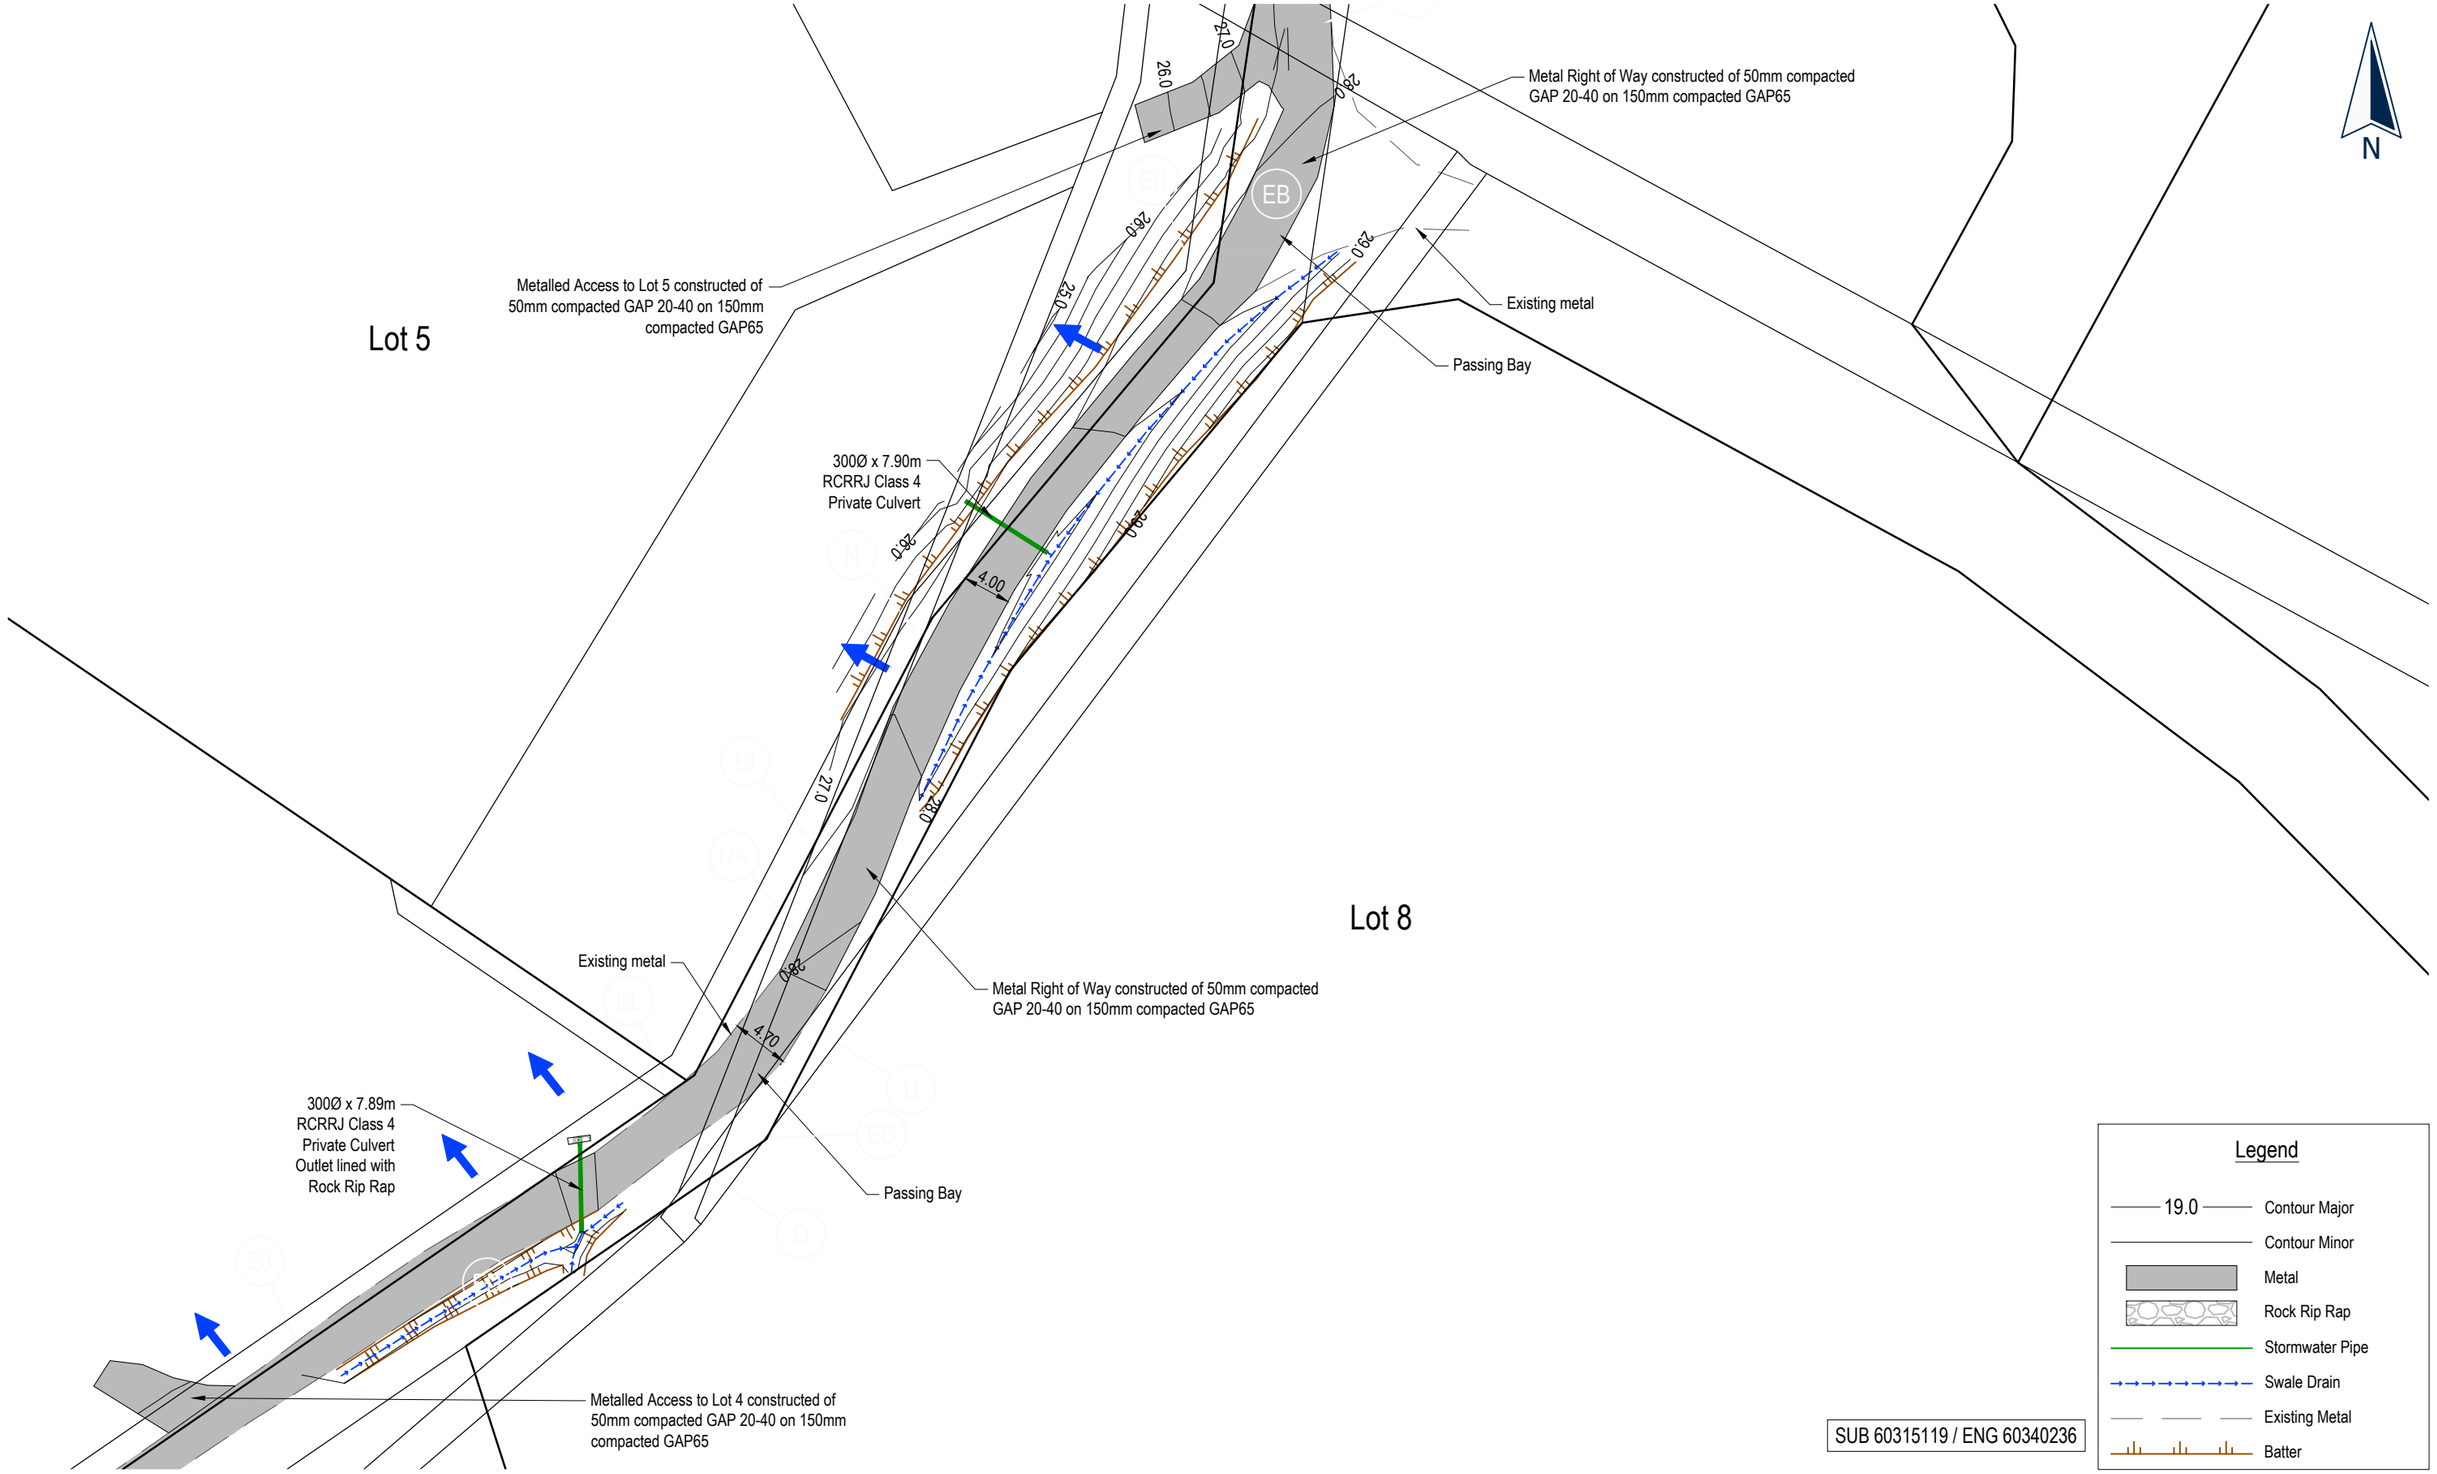

SUB 60315119 / ENG 60340236

Cato Bolam
creating great places
PLANNERS | SURVEYORS | ENGINEERS
ARCHITECTS | ENVIRONMENTAL

This drawing and design remains the property of, and may not be reproduced or amended without the written permission of Cato Bolam Consultants Ltd. No liability shall be accepted for unauthorised use of this drawing and design.

R.&D. Nicklin
53B Remiger Road
Puhoi

Right of Way As Built Plan
Sheet 3 of 3

No.	REVISION (DESCRIPTIONS)	NAME	DATE
0	Issued for Completion	TL	28/04/2021

FOR COMPLETION

	NAME	DATE
SURVEYED	LD	17/08/2020
DESIGNED		
DRAWN	LD	28/04/2021

DATE	ORIGINAL SCALE	ORIGINAL SIZE
28/04/2021	1:500	A3

DRAWING NO. 40320-DR-SU-9002
REVISION 0

EDE0002
EASEMENT DRAWINGS

DRAWING No.	TITLE	REVISION
EDE0002-0000-1	TITLE PAGE AND REVISION HISTORY	1
EDE0002-0001-1	GROUND MOUNTED DISTRIBUTION EQUIPMENT - SET 1	1
EDE0002-0002-1	GROUND MOUNTED DISTRIBUTION EQUIPMENT - SET 2	1
EDE0002-0003-1	GROUND MOUNTED DISTRIBUTION EQUIPMENT - SET 3	1
EDE0002-0004-1	OVERHEAD EQUIPMENT	1
EDE0002-0005-1	ELECTRICITY AND GAS - IN SITU EQUIPMENT	1
EDE0002-0006-1	GAS - REGULATOR STATION	1

Rev	Amendments	Date	Name
1	FIRST ISSUE	20/03/2018	SC
2	ISSUE FOR APPROVAL	18/07/2018	BP

Consultant	VECTOR	File name: EDE0002-0003-1.dwg
Author	SC	
Auth Date	26/02/2018	Consultant project no:
Checked by		
Chk by date		Vector project no:
Approved by		
Appr by date		

© Copyright Vector Limited 2012
All rights reserved, unauthorised reproduction prohibited


EASEMENT DRAWINGS
TITLE PAGE & REVISION HISTORY

STANDARD DRAWING


Reference designation:
Drawing function:
Drawing stamp:
Scale at A3: NTS
Doc type:
Drawing no: EDE0002-0000
Rev: 2
Sheet: 1 of 1

A3 Titleblock Version 4. © Copyright Vector Limited 2012

A. CUBICLE TYPE DISTRIBUTION TRANSFORMER UP TO 500 kVA 11+22kV

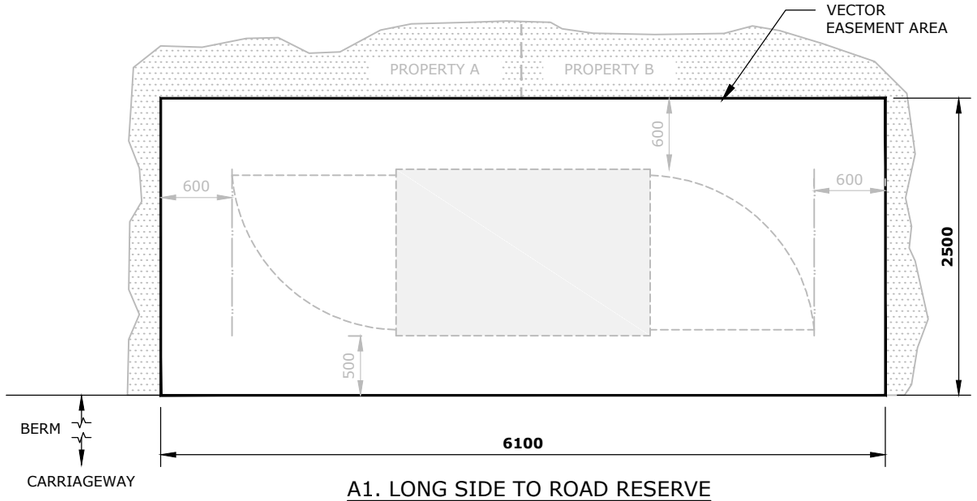


A1. LONG SIDE TO ROAD RESERVE

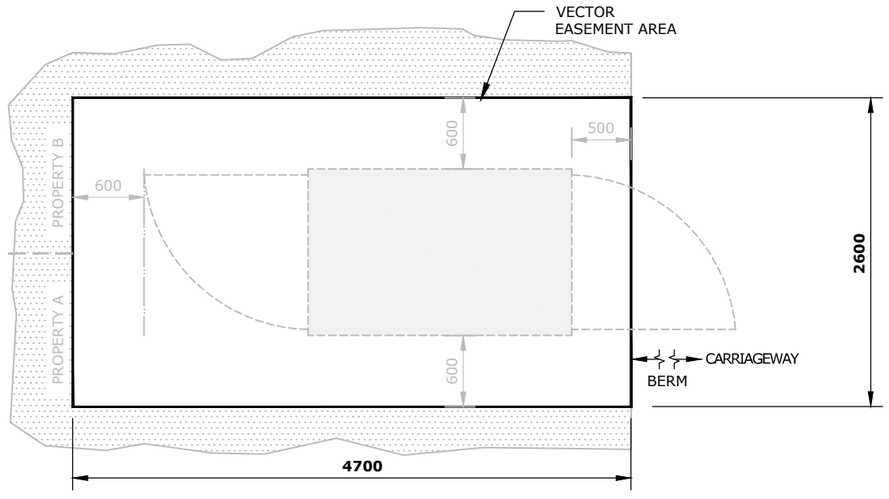


A2. END TO ROAD RESERVE

B. DISTRIBUTION PACKAGE SUBSTATION UP TO 500kVA 11+22kV

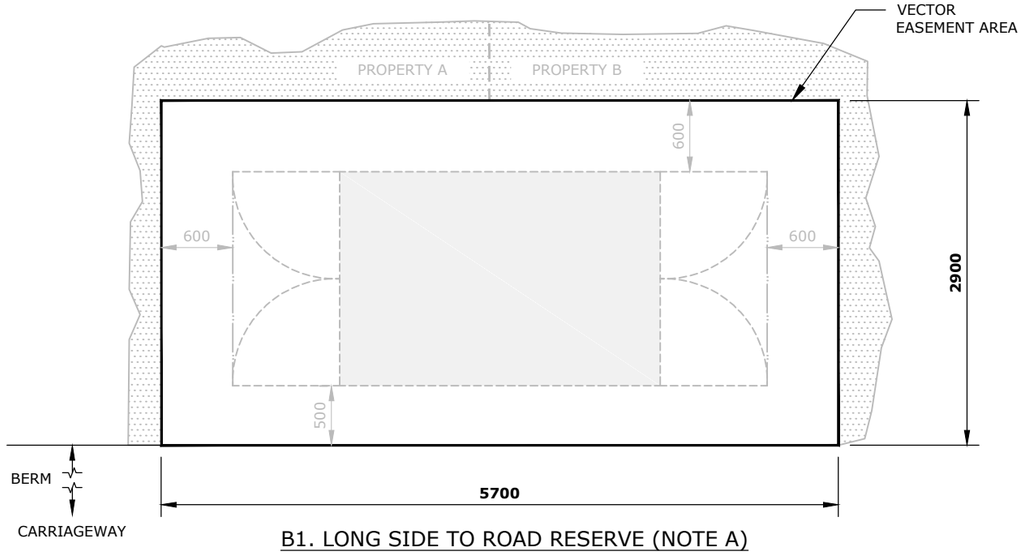

B1. LONG SIDE TO ROAD RESERVE (NOTE A)

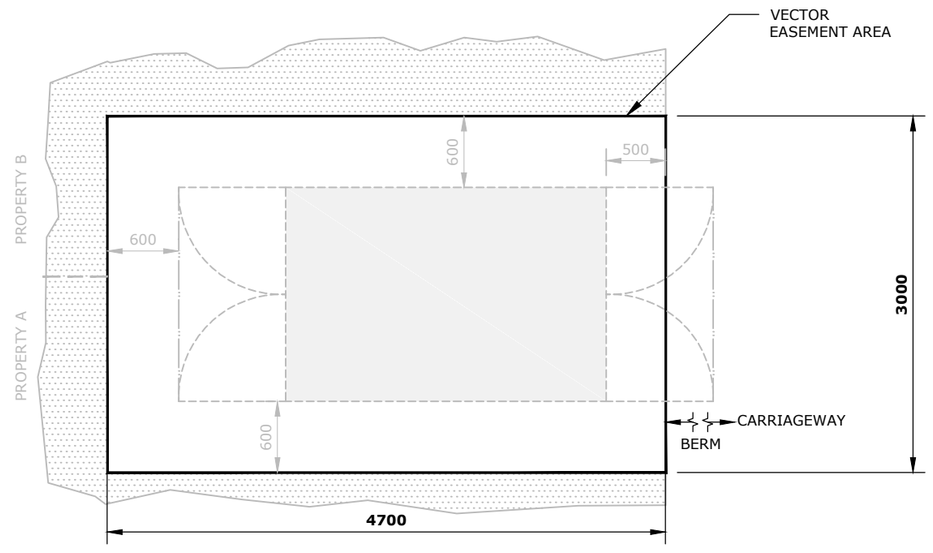

B2. END TO ROAD RESERVE (NOTE A)

NOTES:

A. MAXIMUM EQUIPMENT DIMENSIONS USED TO CREATE EASEMENT AREA

B. EASEMENT AREAS FOR LARGER TRANSFORMERS TO BE ESTABLISHED ON A CASE BY CASE BASIS

Rev	Amendments	Date	Name
1	FIRST ISSUE	20/03/2018	SC
2	ISSUE FOR APPROVAL	18/07/2018	BP

Consultant	VECTOR	File name:	EDE0002-0001-1.dwg
Author	S CONTINI		
Auth Date	18/09/2017	Consultant project no:	
Checked by	H RICHARDS		
Chk by date	18/09/2017	Vector project no:	
Approved by	A PRASAD		
Appr by date	18/09/2017		

© Copyright Vector Limited 2012
All rights reserved, unauthorised reproduction prohibited


EASEMENT DRAWINGS
CUBICLE TYPE DISTRIBUTION TRANSFORMER
AND DISTRIBUTION PACKAGE SUBSTATION

STANDARD DRAWING


Reference designation:			Drawing function:
Drawing stamp:	Scale at A3: NTS		Doc type:
Drawing no: EDE0002-0001		Rev: 2	Sheet: 1 of 1

A3 Titleblock Version 4. © Copyright Vector Limited 2012

C. SWITCHGEAR ADJACENT BERM/CARRIAGEWAY

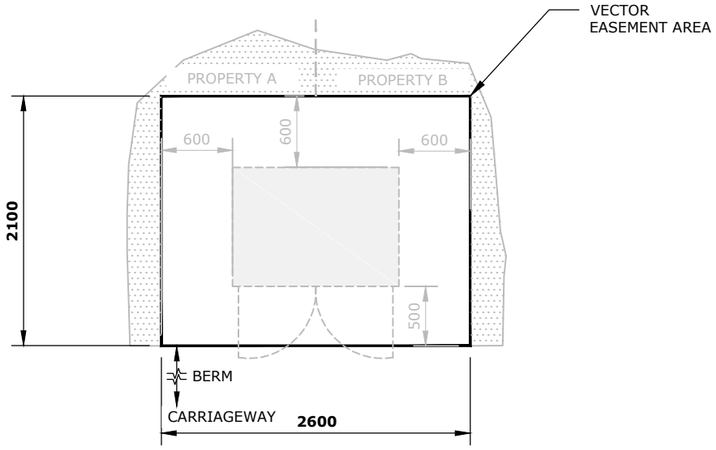


C1. ABB SAFELINK 2 SWITCHGEAR

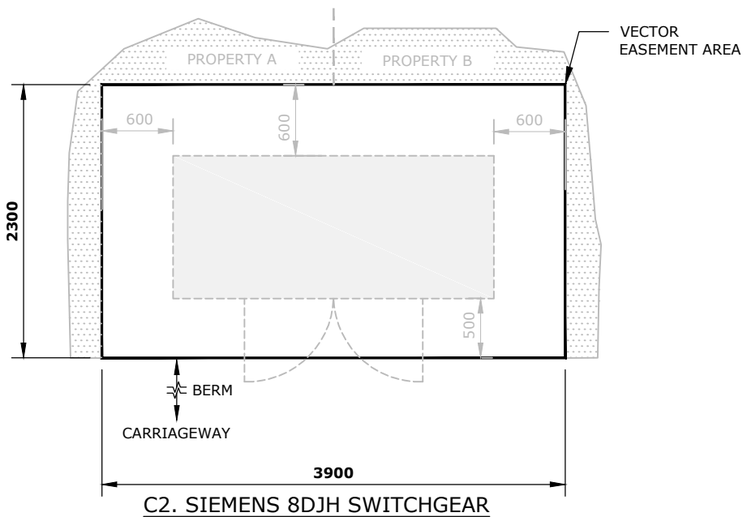


C2. SIEMENS 8DJH SWITCHGEAR

D. SWITCHGEAR WITHIN PRIVATE PROPERTY (NOT ADJACENT BERM/CARRIAGEWAY)

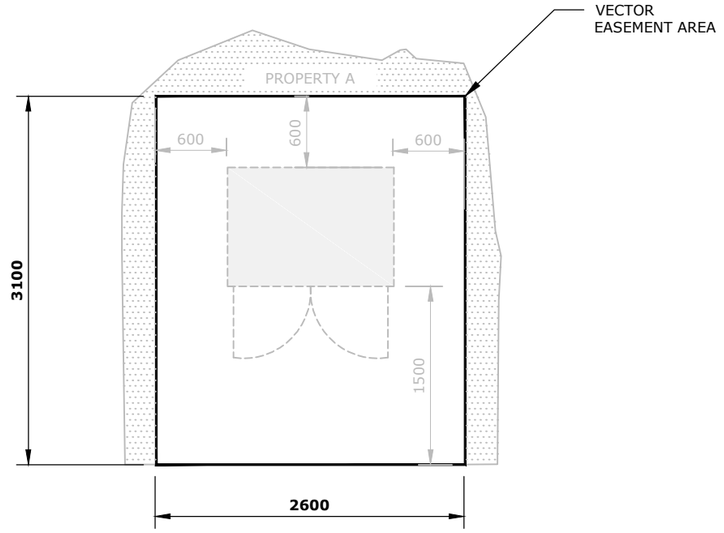

D1. ABB SAFELINK 2 SWITCHGEAR

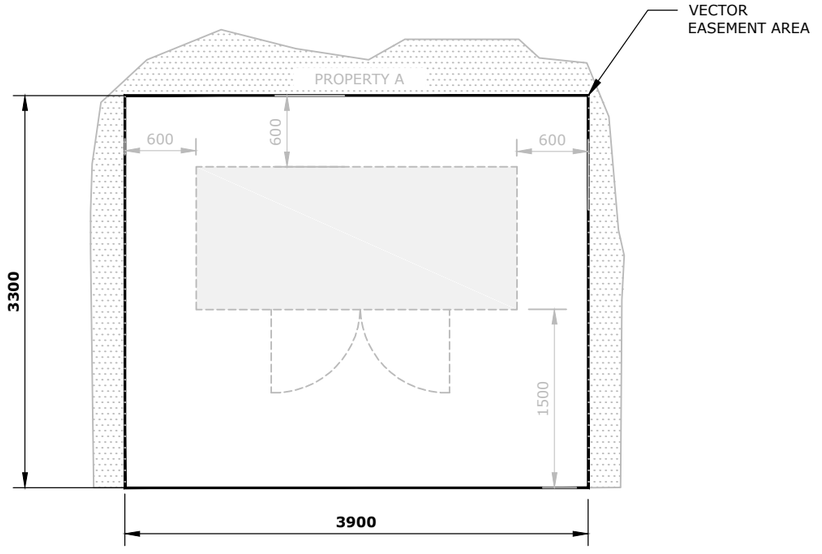

D2. SIEMENS 8DJH SWITCHGEAR

Rev	Amendments	Date	Name
1	FIRST ISSUE	20/03/2018	SC
2	ISSUE FOR APPROVAL	18/07/2018	BP

Consultant	VECTOR	File name: EDE0002-0002-1.dwg
Author	S CONTINI	
Auth Date	18/09/2017	Consultant project no:
Checked by	H RICHARDS	
Chk by date	18/09/2017	Vector project no:
Approved by	A PRASAD	
Appr by date	18/09/2017	

© Copyright Vector Limited 2012
All rights reserved, unauthorised reproduction prohibited

EASEMENT DRAWINGS
SWITCHGEAR ADJACENT BERM/CARRIAGEWAY AND WITHIN PRIVATE PROPERTY

STANDARD DRAWING

Reference designation:

Drawing function:

Drawing stamp:

Scale at A3: NTS

Doc type:


Drawing no: EDE0002-0002

Rev: 2

Sheet: 1 of 1

A3 Titleblock Version 4. © Copyright Vector Limited 2012

E. INDUSTRIAL TYPE DISTRIBUTION TRANSFORMER

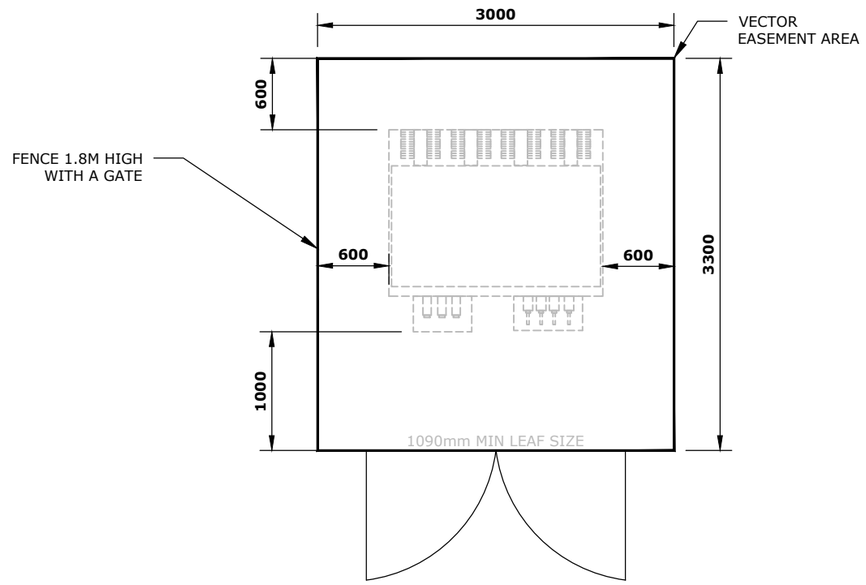

E1. INDUSTRIAL TYPE DISTRIBUTION TRANSFORMER
UP TO 1000kVA, 11+22kV

Rev	Amendments	Date	Name
1	FIRST ISSUE	20/03/2018	SC
2	ISSUE FOR APPROVAL	18/07/2018	BP

Consultant	VECTOR
Author	S CONTINI
Auth Date	18/09/2017
Checked by	H RICHARDS
Chk by date	18/09/2017
Approved by	A PRASAD
Appr by date	18/09/2017

File name: EDE0002-0003-1.dwg
Consultant project no:
Vector project no:

© Copyright Vector Limited 2012
All rights reserved, unauthorised reproduction prohibited


EASEMENT DRAWINGS
INDUSTRIAL TYPE DISTRIBUTION TRANSFORMER

STANDARD DRAWING


Reference designation:
Drawing function:
Drawing stamp:
Scale at A3: NTS
Doc type:
Drawing no: EDE0002-0003
Rev: 2
Sheet: 1 of 1

A3 Titleblock Version 4. © Copyright Vector Limited 2012


F. 11 or 22kV SWITCHGEAR WITH TRANSFORMER COMBINED ON ONE SITE

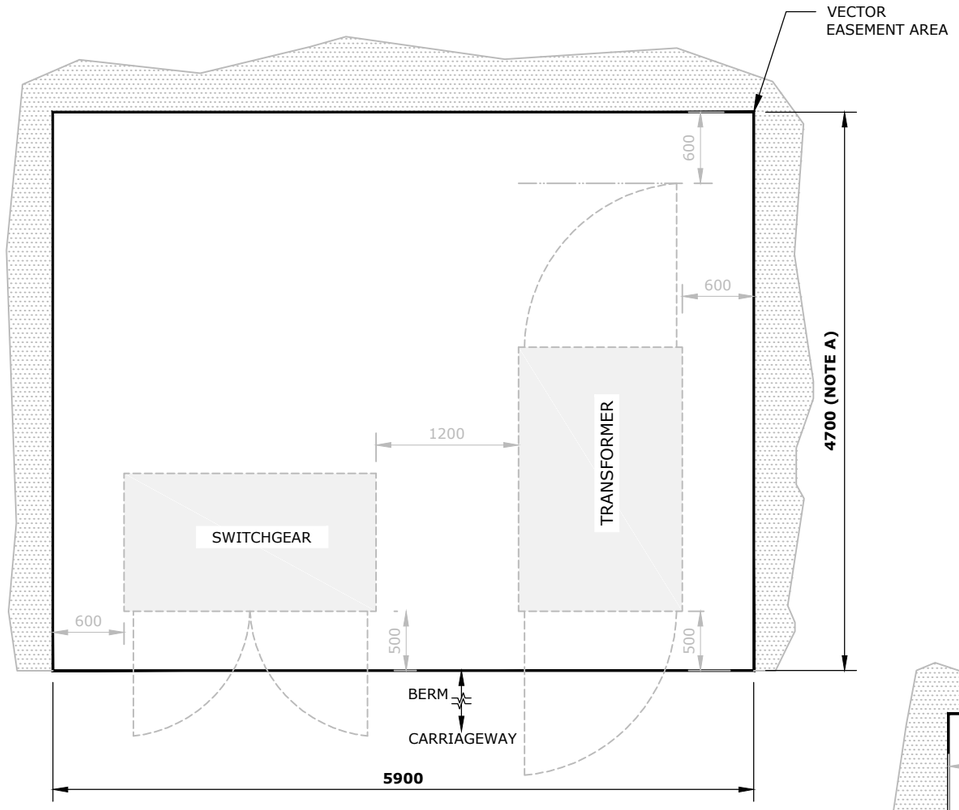

F1. CUBICLE TYPE DISTRIBUTION TRANSFORMER LAYOUT UP TO 500kVA

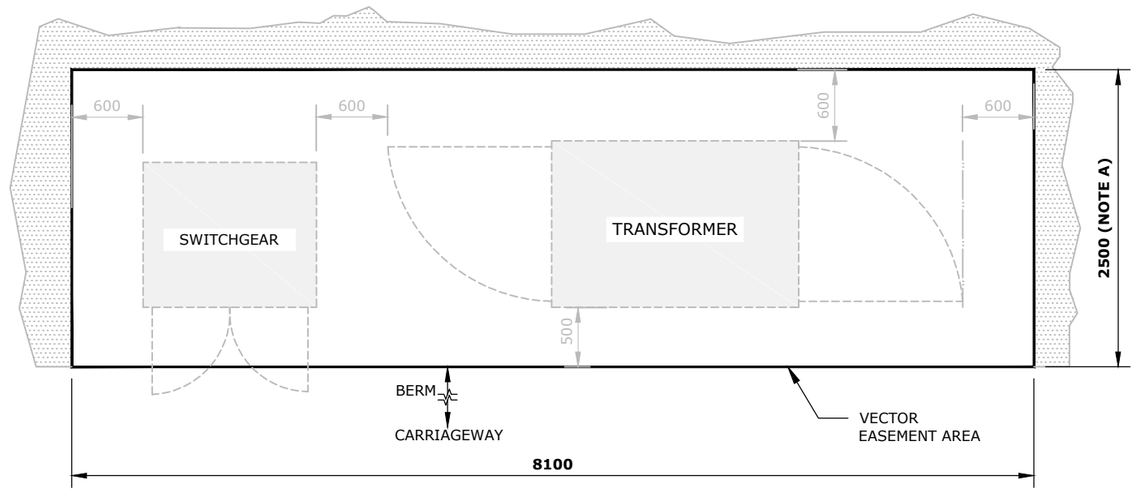

F2. 11KV SWITCHGEAR + CUBICLE TYPE DISTRIBUTION TRANSFORMER UP TO 500kVA

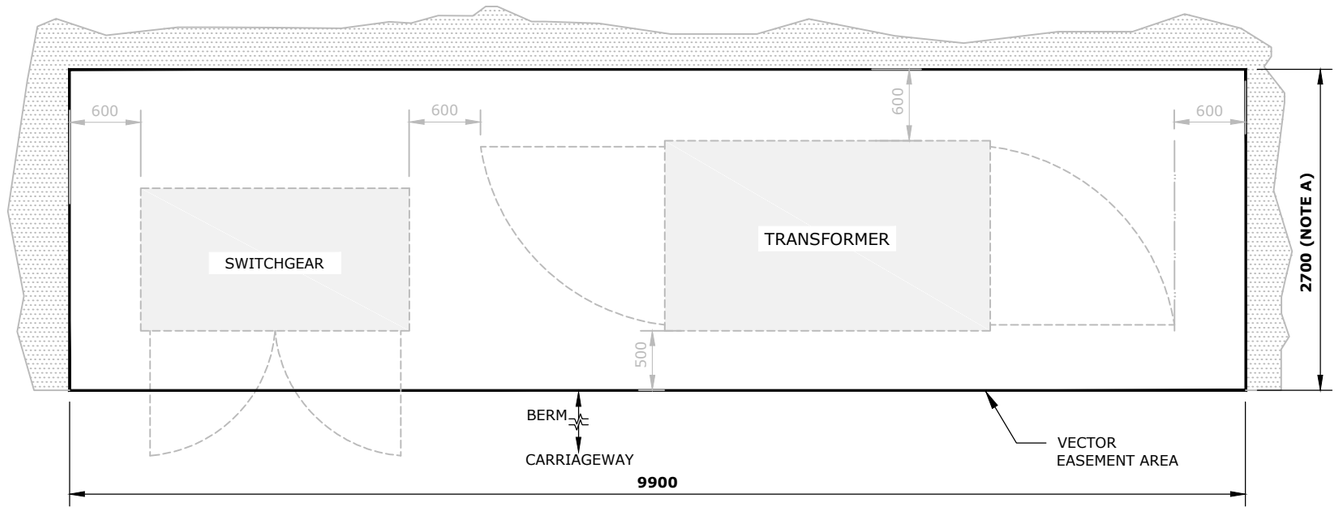

F3. 22KV SWITCHGEAR + CUBICLE TYPE DISTRIBUTION TRANSFORMER UP TO 1500kVA

NOTES:

A. IF LOCATED WITHIN PRIVATE PROPERTY (NOT ADJACENT TO BERM CARRIAGEWAY) ADD 1500mm TO THIS MEASUREMENT

Rev	Amendments	Date	Name
1	FIRST ISSUE	20/03/2018	SC
2	ISSUE FOR APPROVAL	18/07/2018	BP

Consultant	VECTOR	File name: EDE0002-0004-1.dwg
Author	K VERGIS	
Auth Date	20/12/2017	Consultant project no:
Checked by		
Chk by date		Vector project no:
Approved by		
Appr by date		

© Copyright Vector Limited 2012
All rights reserved, unauthorised reproduction prohibited


EASEMENT DRAWINGS
11 or 22kV SWITCHGEAR WITH TRANSFORMER COMBINED ON ONE SITE

STANDARD DRAWING


Reference designation:			Drawing function:
Drawing stamp:	Scale at A3: NTS		Doc type:
Drawing no: EDE0002-0004		Rev: 2	Sheet: 1 of 1

A3 Titleblock Version 4. © Copyright Vector Limited 2012


G. OVERHEAD LINE

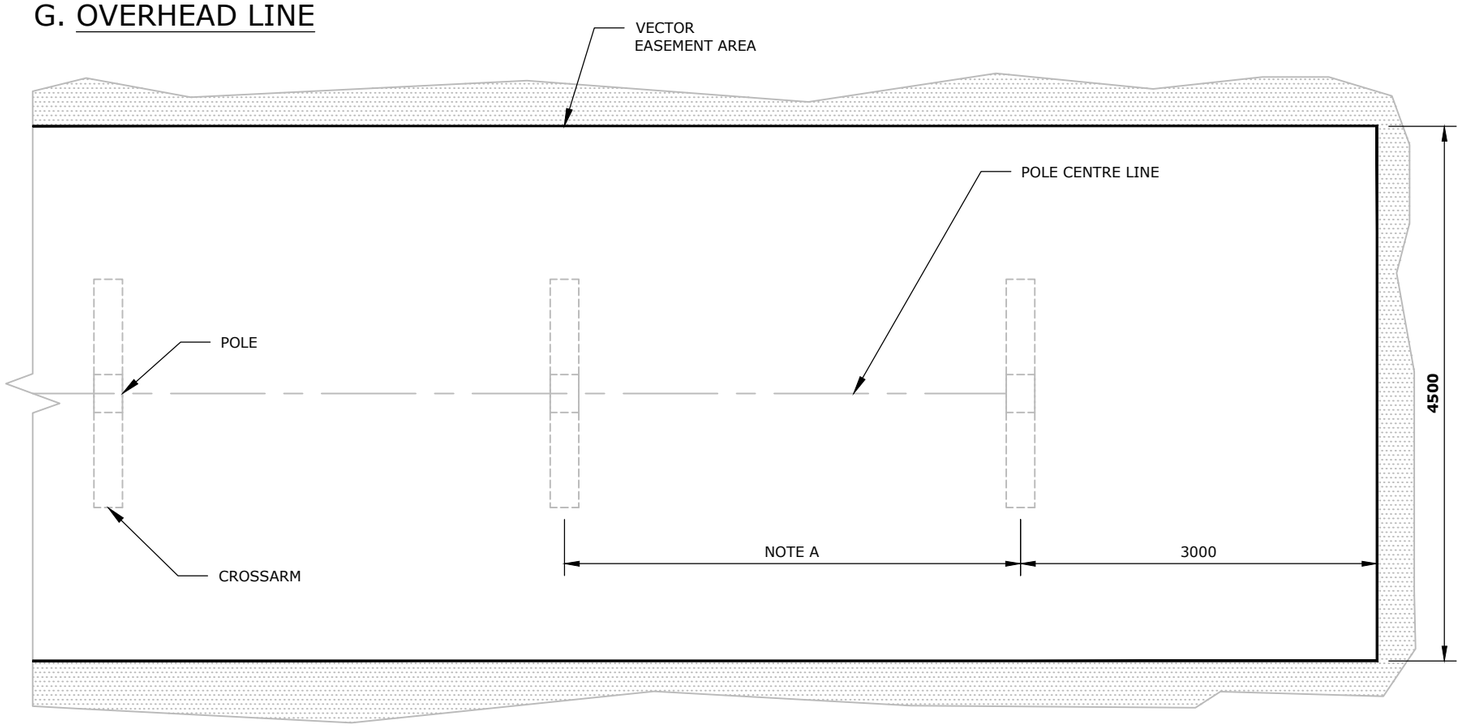

STAY DETAL
PLAN VIEW

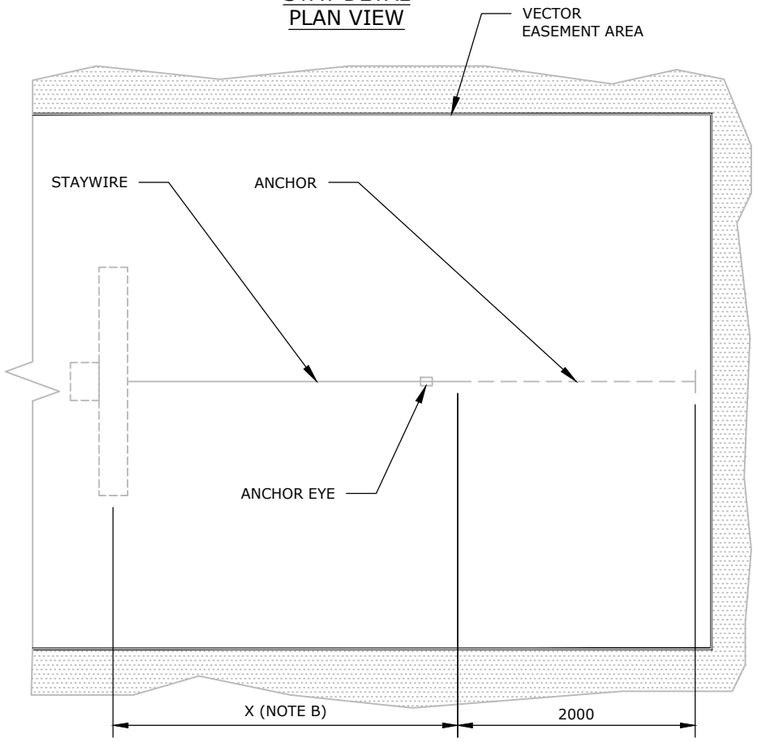

STAY DETAL
ELEVATION

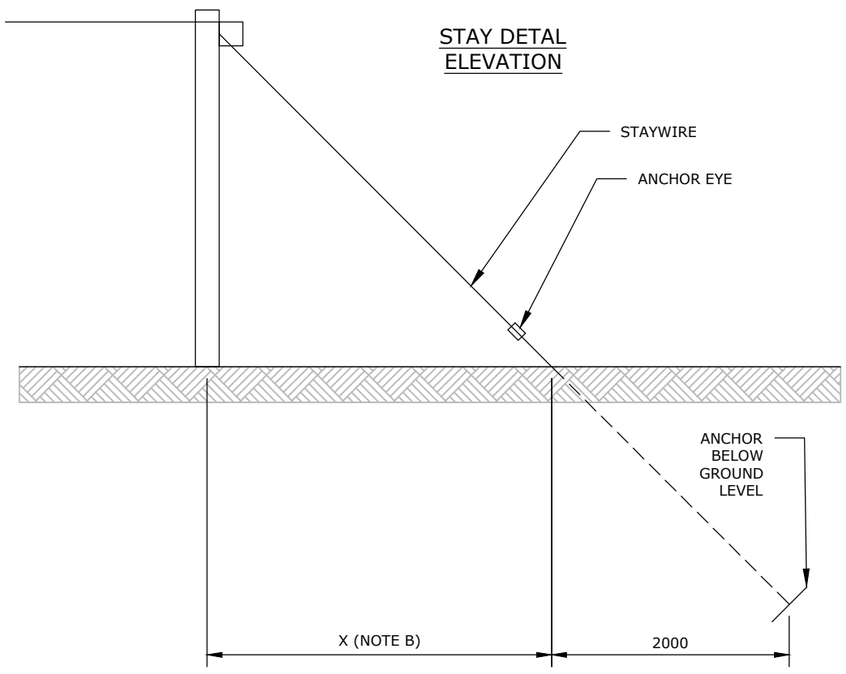

NOTES:

A. EASEMENT AREA REQUIRED FOR A MAXIMUM SPAN LENGTH OF 80m, LONGER SPANS WILL REQUIRE WIDER EASEMENT OVER TO BE CALCULATED
B. DIMENSION 'X' IS DEPENDANT ON POLE HEIGHT AND TO BE SPECIFICALLY DETERMINED.

Rev	Amendments	Date	Name
1	FIRST ISSUE	20/03/2018	SC
2	ISSUE FOR APPROVAL	18/07/2018	BP

Consultant	VECTOR	File name: EDE0002-0005-1.dwg
Author	K VERGIS	
Auth Date	20/12/2017	Consultant project no:
Checked by		
Chk by date		Vector project no:
Approved by		
Appr by date		

© Copyright Vector Limited 2012
All rights reserved, unauthorised reproduction prohibited

EASEMENT DRAWINGS
OVERHEAD EQUIPMENT


STANDARD DRAWING

Reference designation:			Drawing function:
Drawing stamp:	Scale at A3: NTS		Doc type:
Drawing no: EDE0002-0005		Rev: 2	Sheet: 1 of 1


A3 Titleblock Version 4. © Copyright Vector Limited 2012

H. UNDERGROUND CABLE


SINGLE CABLE

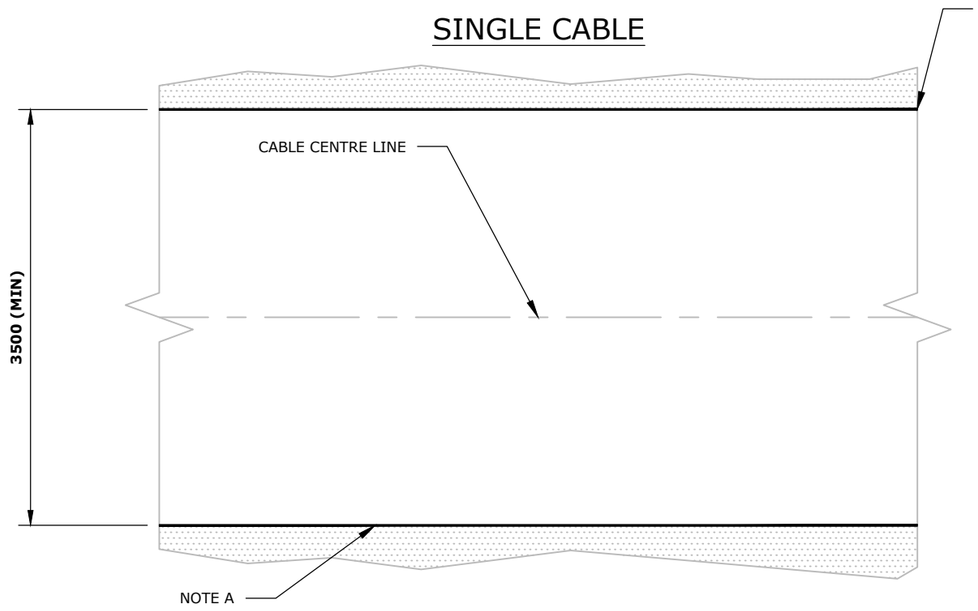


MULTIPLE CABLES/DUCTS

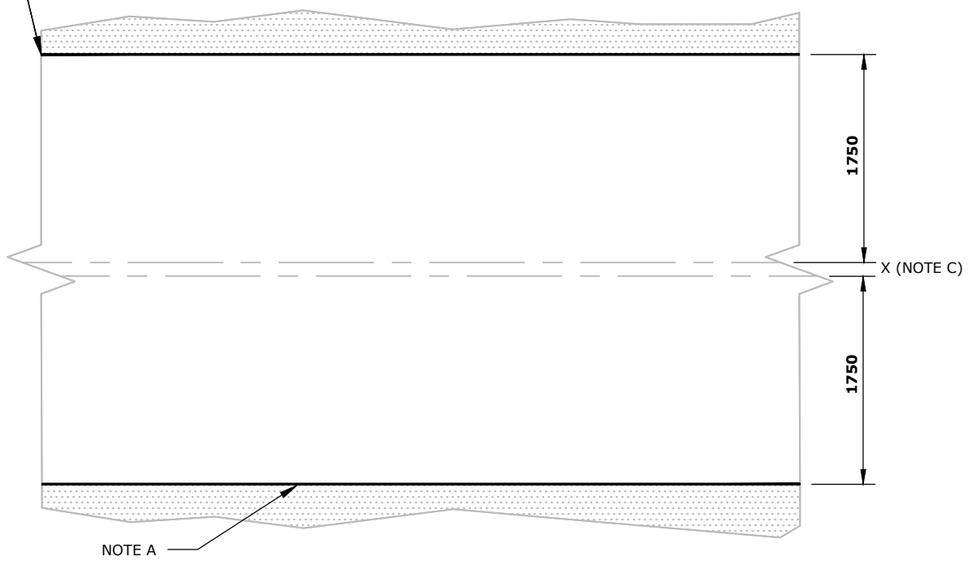

PILLAR/PIT

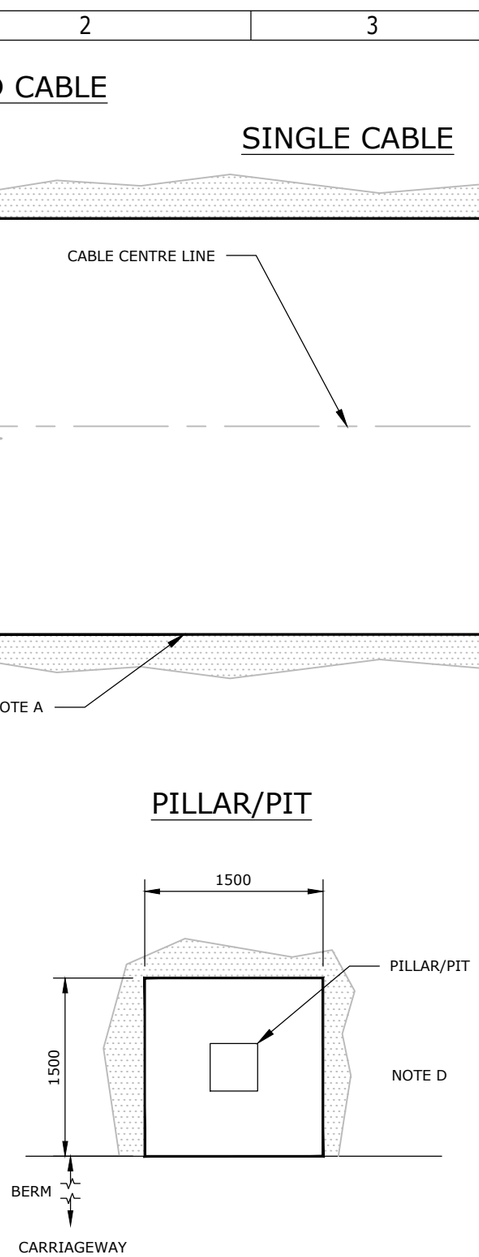

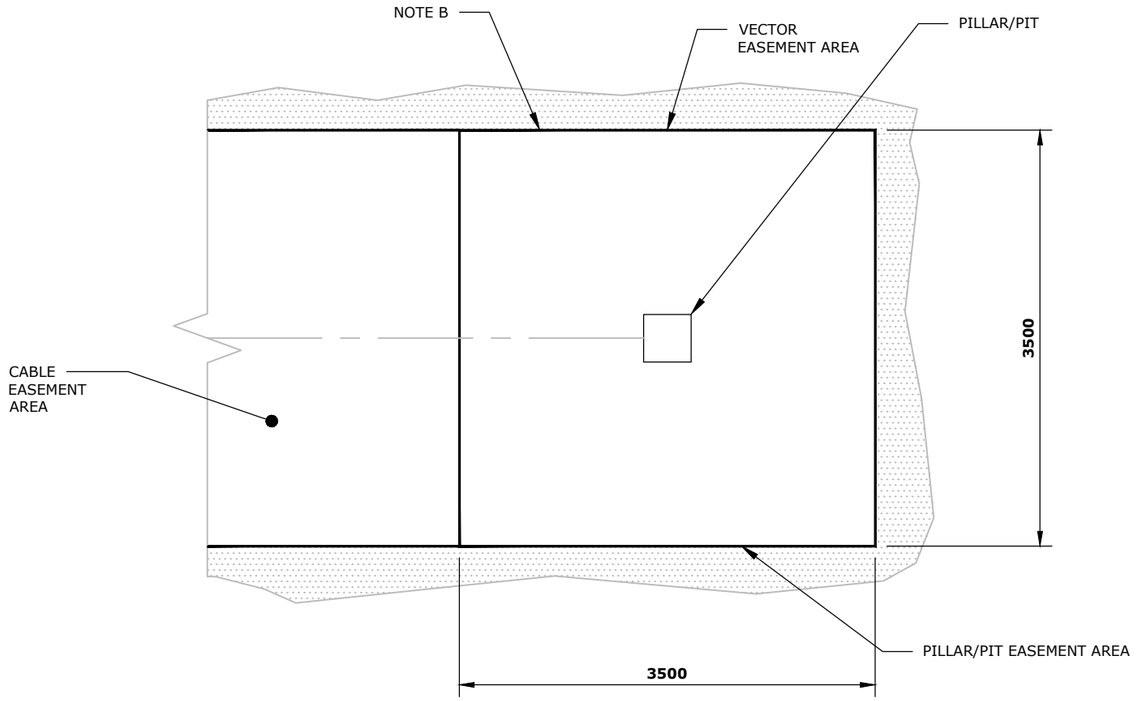

NOTES:

A. IF INSTALLED IN RIGHT OF WAY, EASEMENT REQUIRED OVER ENTIRE RIGHT OF WAY WIDTH
B. IF NOT INSTALLED BESIDE A CARRIAGEWAY/BERM AND ADJACENT TO A CABLE, A 3.5m x 3.5m AREA REQUIRED
C. DISTANCE X DETERMINED BY OUTER MEASUREMENT OF CABLES/DUCTS
D. IF A PILLAR/PIT IS INSTALLED WITHIN A ROW THEN NO ADDITIONAL EASEMENT AREA IS REQUIRED OVER ADJACENT LOTS

Rev	Amendments	Date	Name
1	FIRST ISSUE	20/03/2018	SC
2	ISSUE FOR APPROVAL	18/07/2018	BP

Consultant	VECTOR
Author	K VERGIS
Auth Date	20/12/2017
Checked by	
Chk by date	
Approved by	
Appr by date	

File name: EDE0002-0006-1.dwg
Consultant project no:
Vector project no:

© Copyright Vector Limited 2012
All rights reserved, unauthorised reproduction prohibited

EASEMENT DRAWINGS
ELECTRICITY - IN SITU EQUIPMENT


STANDARD DRAWING

Reference designation:
Drawing function:
Drawing stamp:
Scale at A3: NTS
Doc type:
Drawing no: EDE0002-0006
Rev: 2
Sheet: 1 of 1


A3 Titleblock Version 4. © Copyright Vector Limited 2012

I. GAS MAIN


SINGLE PIPELINE

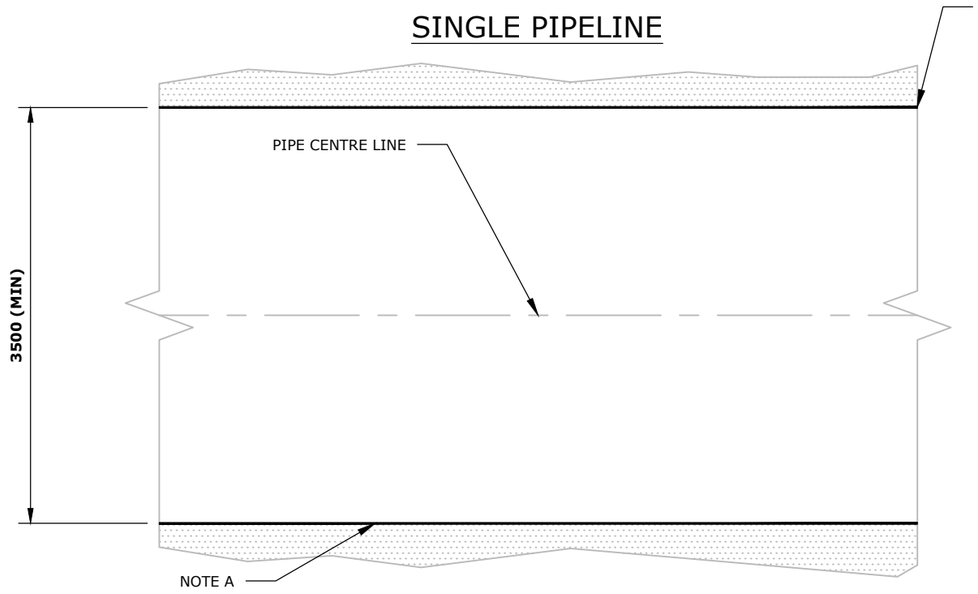

MULTIPLE PIPELINES

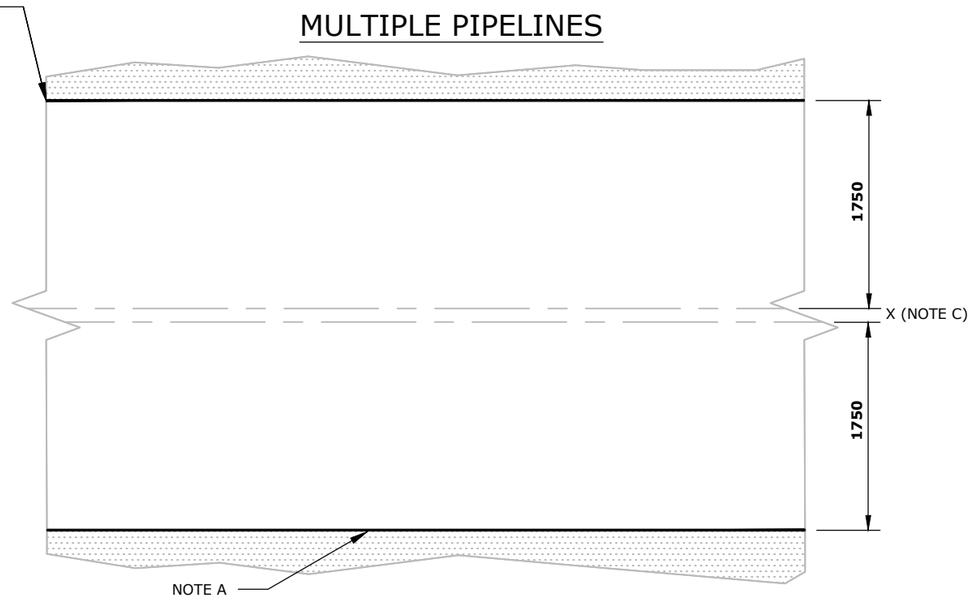

J. GAS REGULATOR STATION

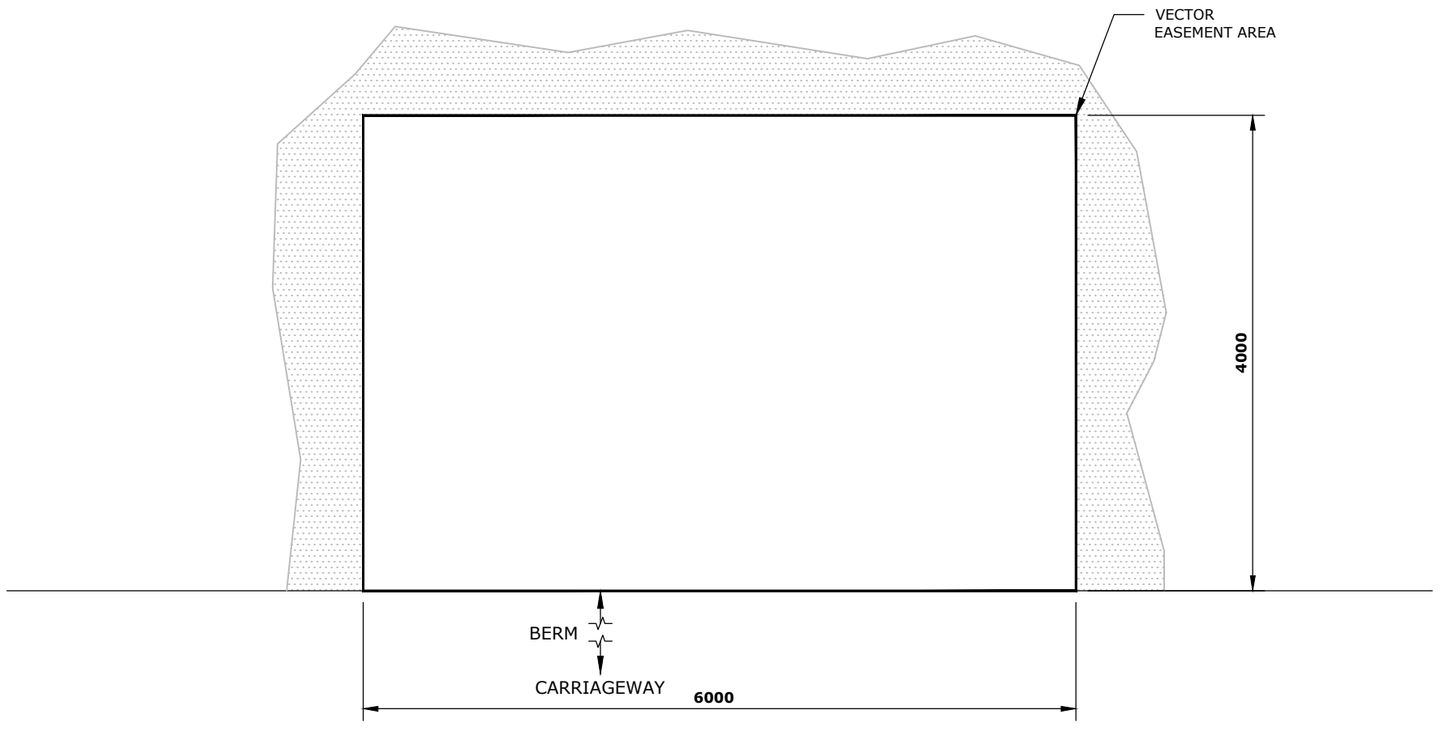

NOTES:

A. IF INSTALLED IN RIGHT OF WAY, EASEMENT REQUIRED OVER ENTIRE RIGHT OF WAY WIDTH
B. IF NOT INSTALLED BESIDE A CARRIAGEWAY/BERM AND ADJACENT TO A CABLE, A 3.5m x 3.5m AREA REQUIRED
C. DISTANCE X DETERMINED BY OUTER MEASUREMENT OF CABLES/DUCTS

Rev	Amendments	Date	Name
1	FIRST ISSUE	20/03/2018	SC
2	ISSUE FOR APPROVAL	18/07/2018	BP

Consultant	VECTOR
Author	K VERGIS
Auth Date	20/12/2017
Checked by	
Chk by date	
Approved by	
Appr by date	

File name: EDE0002-0007-1.dwg
Consultant project no:
Vector project no:

© Copyright Vector Limited 2012
All rights reserved, unauthorised reproduction prohibited

EASEMENT DRAWINGS
GAS MAIN AND REGULATOR STATION

STANDARD DRAWING

Reference designation:
Drawing function:
Drawing stamp:
Scale at A3: NTS
Doc type:
Drawing no: EDE0002-0007
Rev: 2
Sheet: 1 of 1

A3 Titleblock Version 4. © Copyright Vector Limited 2012

Legend:

- HV Overhead Conductors
- LV Overhead Conductors
- HV Switch
- Transformers
- Poles
- Service Pillar/Pit

Remiger Road Stewardship Area

Remiger Bush Scenic Reserve

Remiger Road

Pole 109326
N8420P

Pole 12881
N2015

Pole 109325
F9132

Pole 109324

Pole 46229

Pole 47944

Pole 46230
TB794

Pole 109322
7266

Pole 109323

Pole 109321

Pole 109334



Install single phase 100A isolation fuse on pole #46229 to facilitate supply for customers 2x new single phase 60A supplies

Upgrade existing LV crossarms on pole #109324 to 2.4m two-way termination crossarms and split LV conductors

Relocate point of supply fusing for woolshed from pole #109323 to pole #109324

Install new single phase 100A isolation fuse on pole #109324 to facilitate supply for customers 2x new single phase 60A supplies





Upgrade existing 15kVA transformer to a single phase 30kVA pole mount transformer on existing 11m pole #46230

Install new DDO crossarm and DOF fusing to facilitate isolation for upgraded transformer

Install new Earthbank for upgraded transformer

Easement areas for new pole equipment 4m x 4m

Rev	Amendments	Date	Name
1	FOR APPROVAL	17/12/20	
1	FINAL	28/01/21	

Consultant		File name:
Author	M PURCELL	
Auth Date	17/12/2020	Consultant project no:
Checked by	S MACER	
Chk by date	17/12/2020	Vector project no:
Approved by		EC-21-NCIP4-084
Appr by date		

vector electrix

TITLE1 : 53B Remiger Road, Puhoi
TITLE2 : New Supplies
TITLE3 :

SUBSTATION

Reference designation:

Drawing function:

Drawing stamp: FINAL

Scale at A3:

Doc type:

Drawing no: NUMBER

Rev: 1

Sheet: 1 of 1