Auckland Council

SUB60315119-A

Approved Resource Consent Plan

26/10/2023

N

This drawing and design remains the property of, and may not be reproduced or amended without the written permission of Cato Bolam Consultants Ltd. No liability shall be accepted for unauthorised use of this drawing and design.

Auckland Council
Comprised in:

RT NA137A/506Ltd	57.4262ha
RT NA105B/748	24.1140ha
RT NA31C/965	21.6507ha
RT NA757/204Ltd	37.0692ha
RT NA2100/21Ltd	160.87ha
RT NA127B/898	1.1705ha
Total Area	302.3006ha

Areas and measurements are subject to survey.

- Riparian Margin Protection
- Significant Ecological Area
- Proposed Building Area
- Watercourse
- Extent of Flood Plain

Areas (CP)-(CV) (53.07ha) are to be subject to land covenants to protect native bush .

Areas (CO)(CX)-(CZ)(Z) (0.9ha) are to be subject to land covenants to protect riparian planting.

Cato Bolam
creating great places
PLANNERS | SURVEYORS | ENGINEERS
ARCHITECTS | ENVIRONMENTAL

R.C.& D.E. Nicklin
53B Remiger Road
Puhoi

Lots 1 - 8 being
Proposed Subdivision of
Lot 8 DP 208981, Lot 5 DP 198556
Lot 1 DP 179794, Allots 32,35,54A &
Pt Allots 30,31,36 Parish of Puhoi

FOR RESOURCE CONSENT

No.	REVISION (DESCRIPTIONS)	NAME	DATE
C	Lots 3 & 8 adjusted	MG	05/05/2023
D	Lots 3 & 6 adjusted Lots 9 & 10 added	MG	22/06/2023
E	Lot 8 adjusted, OLFPS deleted	MG	25/07/2023
F	Lot 3/6 bdy adjstd, Lots 9 & 10 deleted	MG	11/10/2023
SURVEYED			
DESIGNED			
DRAWN		LS	08/09/2017

DATE	ORIGINAL SCALE	ORIGINAL SIZE
11/10/2023	1:10,000	A3


DRAWING NO.	REVISION
40320-DR-PLN-1200	F

EXISTING EASEMENTS

PURPOSE	SHOWN	BURDENED LAND	CREATED BY
RIGHT OF WAY & TELECOMMUNICATIONS	B C D	LOT 6 HEREON	E.C. D460766.5 E.C. D611644.6
RIGHT TO CONVEY TELECOMMUNICATIONS	K N O W XA Y YA	LOT 6 HEREON	E.C. D460766.5 E.I. 6170820.9
	I L M	LOT 5 HEREON	
	P Q X	LOT 8 HEREON	
	YB	LOT 3 HEREON	
RIGHT TO CONVEY ELECTRICITY	YB	LOT 3 HEREON	
	O S U W XA Y YA	LOT 6 HEREON	
	P Q T V X	LOT 8 HEREON	

EXISTING EASEMENTS IN GROSS

PURPOSE	SHOWN	BURDENED LAND	CREATED BY
RIGHT TO CONVEY ELECTRICITY	C G R	LOT 6 HEREON	E.I. 9236051.4
	E	LOT 2 HEREON	
	F	LOT 1 HEREON	
	H I J Z	LOT 5 HEREON	

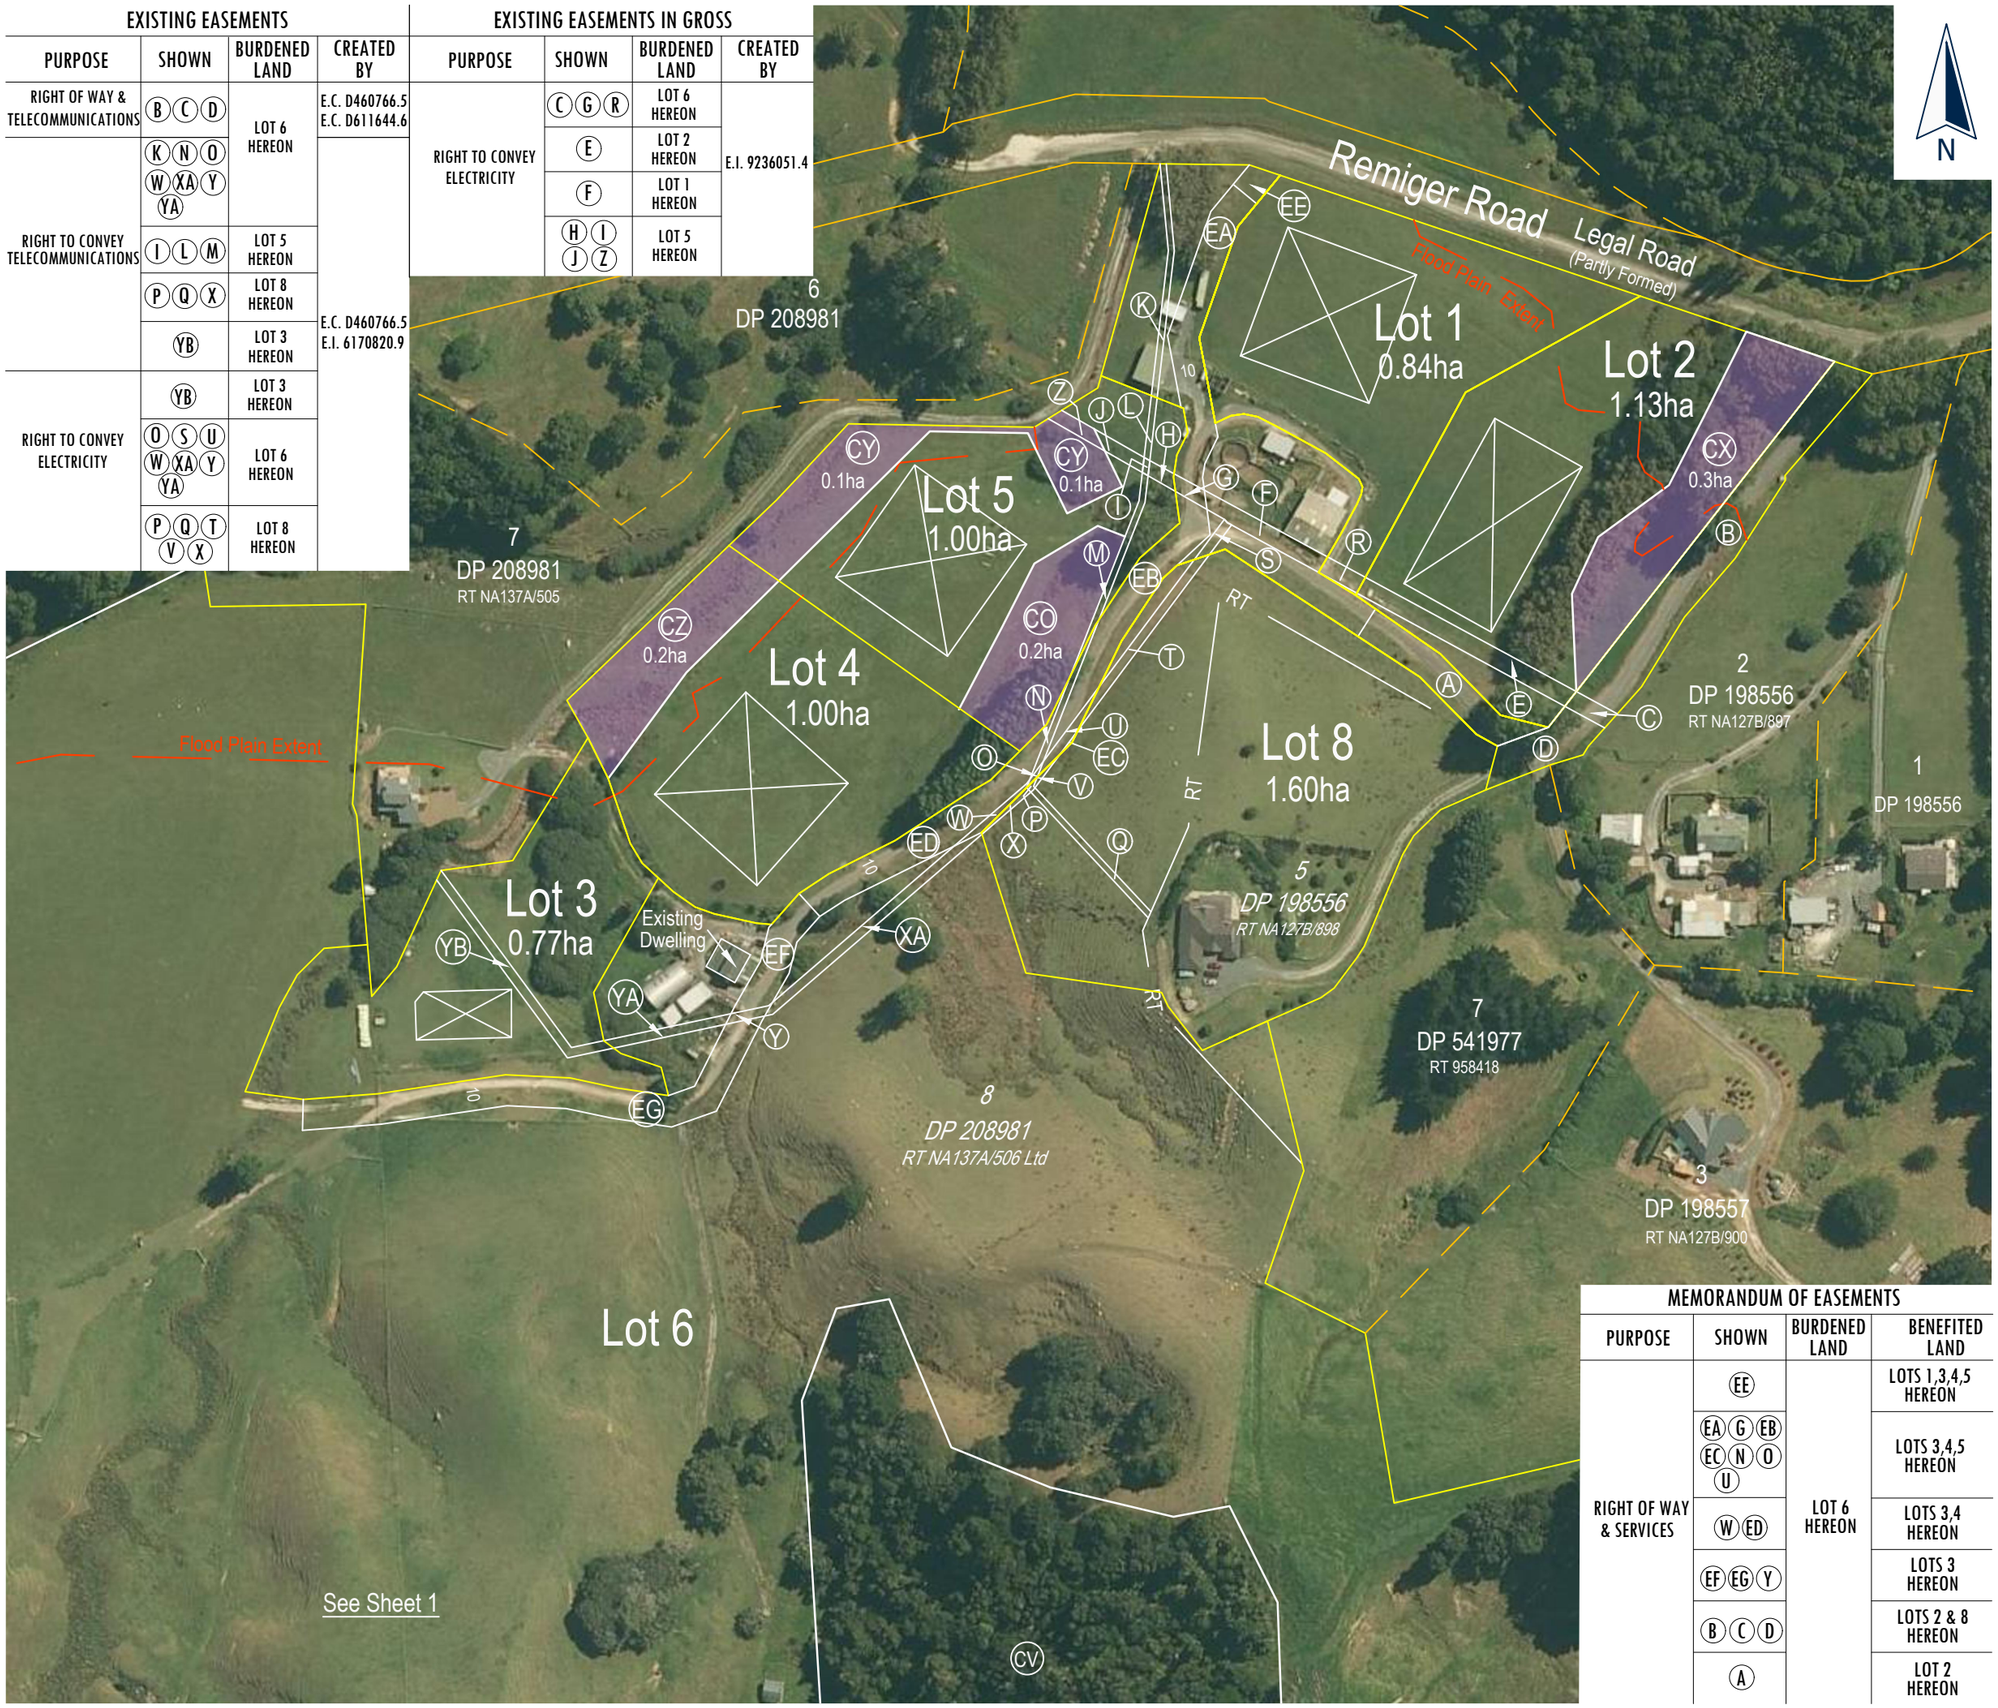

MEMORANDUM OF EASEMENTS

PURPOSE	SHOWN	BURDENED LAND	BENEFITED LAND
RIGHT OF WAY & SERVICES	EE	LOT 6 HEREON	LOTS 1,3,4,5 HEREON
	EA G EB EC N O U		LOTS 3,4,5 HEREON
	W ED		LOTS 3,4 HEREON
	EF EG Y		LOTS 3 HEREON
	B C D		LOTS 2 & 8 HEREON
	A		LOT 2 HEREON

This drawing and design remains the property of, and may not be reproduced or amended without the written permission of Cato Bolam Consultants Ltd. No liability shall be accepted for unauthorised use of this drawing and design.

Auckland Council
Comprised in:

RT NA137A/506Ltd	57.4262ha
RT NA105B/748	24.1140ha
RT NA31C/965	21.6507ha
RT NA757/204Ltd	37.0692ha
RT NA2100/21Ltd	160.87ha
RT NA127B/898	1.1705ha
Total Area	302.3006ha

Areas and measurements are subject to survey.

- Riparian Margin Protection
- Significant Ecological Area
- Proposed Building Area
- Watercourse
- Extent of Flood Plain

Areas (CP)-(CV) (53.07ha) are to be subject to land covenants to protect native bush .

Areas (CO)(CX)-(CZ)(Z) (0.9ha) are to be subject to land covenants to protect riparian planting.

Cato Bolam
creating great places
PLANNERS | SURVEYORS | ENGINEERS
ARCHITECTS | ENVIRONMENTAL

R.C.& D.E. Nicklin
53B Remiger Road
Puhoi

Lots 1 - 8 being
Proposed Subdivision of
Lot 8 DP 208981, Lot 5 DP 198556
Lot 1 DP 179794, Allots 32,35,54A &
Pt Allots 30,31,36 Parish of Puhoi

FOR RESOURCE CONSENT

No.	REVISION (DESCRIPTIONS)	NAME	DATE
C	Lots 3 & 8 adjusted	MG	05/05/2023
D	Lots 3 & 6 adjusted Lots 9 & 10 added	MG	22/06/2023
E	Lot 8 adjusted OLFP deleted	MG	25/07/2023
F	Lot 3/6 bdy adjstd, Lots 9 & 10 deleted	MG	11/10/2023
SURVEYED			
DESIGNED			
DRAWN		LS	08/09/2017

DATE	ORIGINAL SCALE	ORIGINAL SIZE
11/10/2023	1:2000	A3

DRAWING NO. 40320-DR-PLN-1201
REVISION F