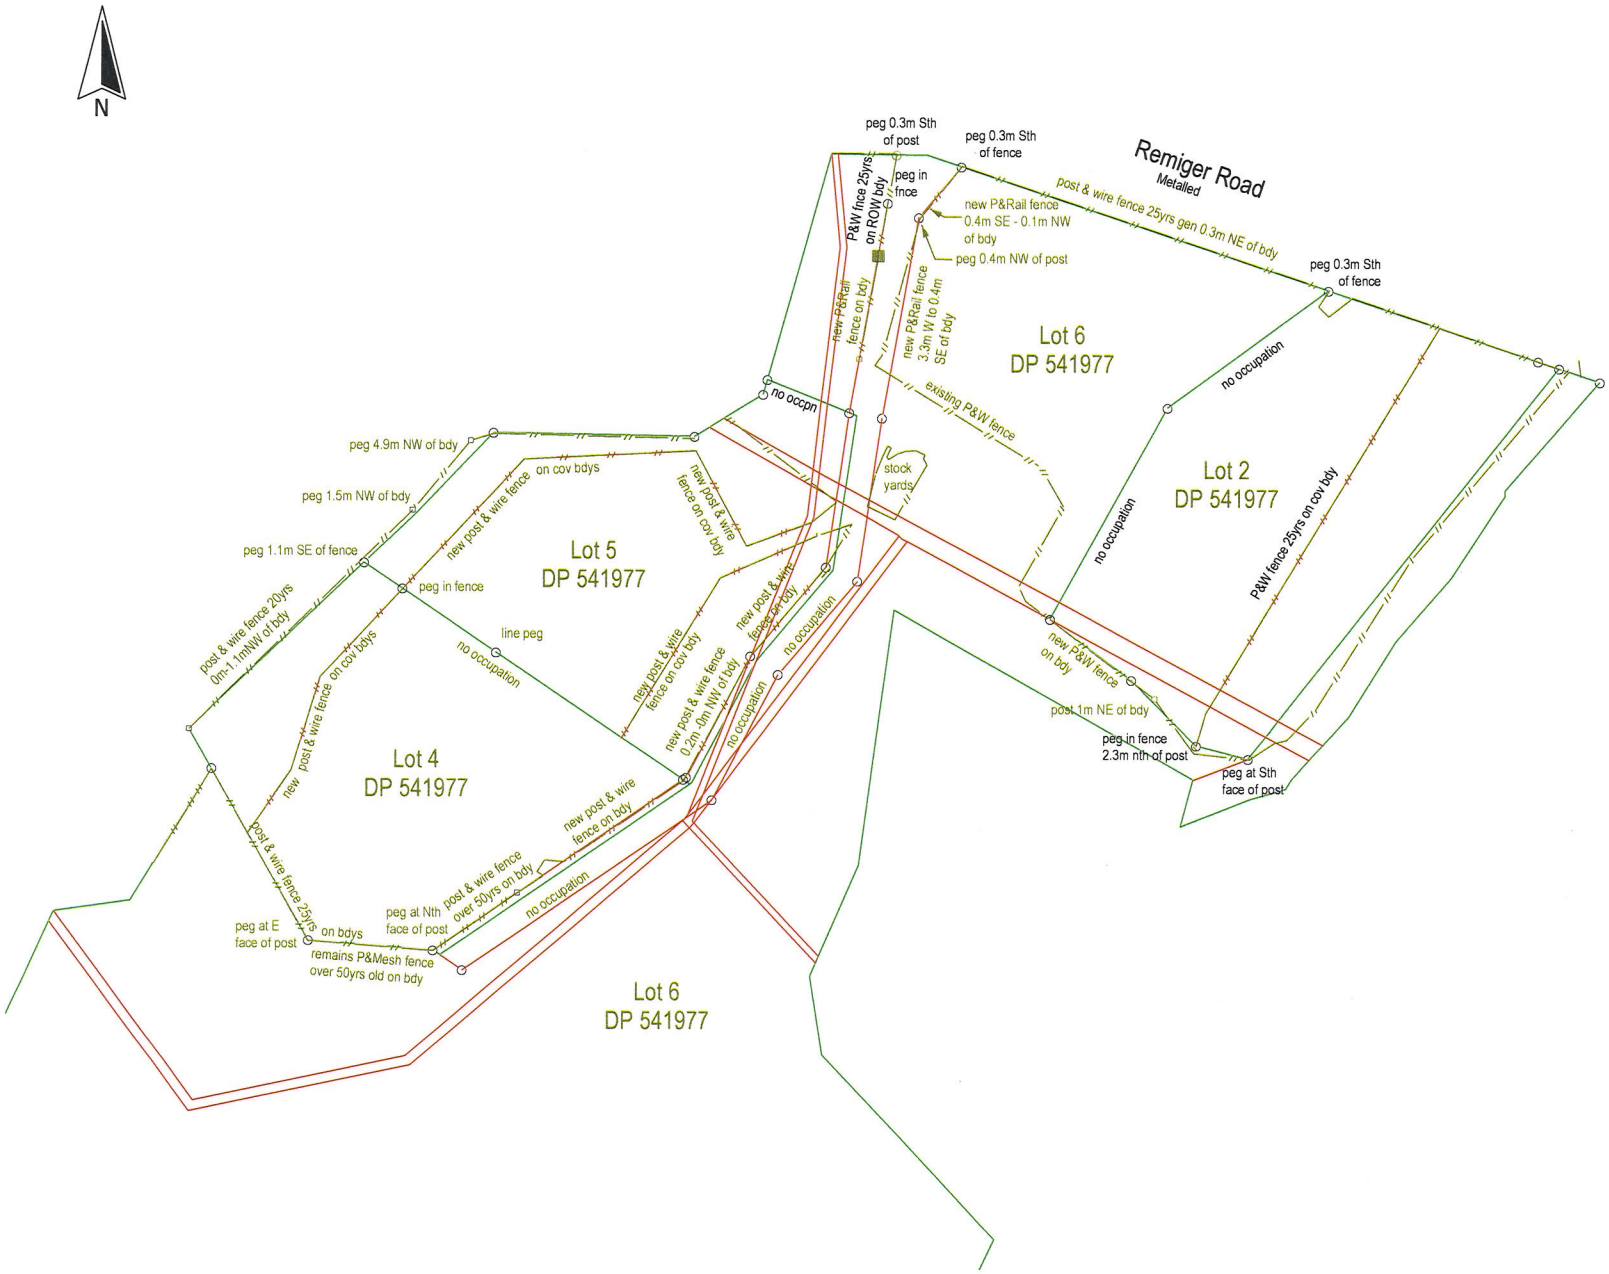


Cato Bolam
creating great places
PLANNERS | SURVEYORS | ENGINEERS
ARCHITECTS | ENVIRONMENTAL

RC & DE Nicklin
Remiger Road
Puhoi

Occupation Diagram

FOR LT DATASET

No.	REVISION (DESCRIPTIONS)	NAME	DATE
A			
SURVEYED		JC & LD	03/2020
DESIGNED			
DRAWN		JC	22/04/2020

DATE	ORIGINAL SCALE	ORIGINAL SIZE
22/04/2020	1:1500	A3

DRAWING NO.	REVISION
40320-DR-SU-LZ03	A

CCAD

Cheryl Pienaar

From: John Clements <JohnC@catobolam.co.nz>
Sent: Friday, 19 June 2020 9:42 AM
To: Cheryl Pienaar
Cc: Frank Lovering; Bruce Angove; Brad Mowat
Subject: [#CBC 40320] SUB60315119 R & D Nicklin, Remiger Road, Puhoi
Attachments: 40320 Occupation Diagram.pdf

Hi Cheryl,

Further to s223 application yesterday, can you also include a roading certificate for Remiger Road where part title limitations are being removed by Lot 2.
The balance Lot 6 will remain limited as to parcels.
A copy of the occupation diagram in attached for you information.

Thanks & Regards,
John Clements.

Cato Bolam
creating great places
PLANNERS | SURVEYORS | ENGINEERS
ARCHITECTS | ENVIRONMENTAL

John Clements
Survey Technician
09 427 0072
johnc@catobolam.co.nz
19 Tamariki Avenue, Orewa
catobolam.co.nz

WARNING This e-mail contains information which is CONFIDENTIAL and that may be subject to PRIVILEGE. If you are not the intended recipient, you must not peruse, use, disseminate, distribute or copy this email or attachments. If you have received this in error, please notify us immediately by return e-mail, facsimile or telephone and delete this e-mail. Thank you