Title Plan - LT 541977

Survey Number	LT 541977
Surveyor Reference	40320 Nicklin (stage 1)
Surveyor	Bradley Mark Mowat
Survey Firm	Cato Bolam Consultants Ltd (Orewa)
Surveyor Declaration	

Survey Details

Dataset Description	Lots 2, 4, 5 & 6 Being Subdivision of Lot 8 DP 208981 & Land Covenant over Allot 32 Puhoi Parish		
Status	Initiated		
Land District	North Auckland	**Survey Class**	Class B
Submitted Date		**Survey Approval Date**	
		Deposit Date	

Territorial Authorities

Auckland Council

Comprised In

RT NA2100/21 Ltd
RT NA137A/506 Ltd
RT NA757/204 Ltd
RT NA31C/965
RT NA105B/748

Created Parcels

Parcels	Parcel Intent	Area	RT Reference
Lot 2 Deposited Plan 541977	Fee Simple Title	1.1120 Ha	911732
Area B Deposited Plan 541977	Easement		
Area C Deposited Plan 541977	Easement		
Area D Deposited Plan 541977	Easement		
Area EC Deposited Plan 541977	Easement		
Area NA Deposited Plan 541977	Easement		
Area P Deposited Plan 541977	Easement		
Area Q Deposited Plan 541977	Easement		
Area U Deposited Plan 541977	Easement		
Area V Deposited Plan 541977	Easement		
Area X Deposited Plan 541977	Easement		
Area E Deposited Plan 541977	Easement		
Area EG Deposited Plan 541977	Easement		
Area I Deposited Plan 541977	Easement		
Area J Deposited Plan 541977	Easement		
Area K Deposited Plan 541977	Easement		
Area L Deposited Plan 541977	Easement		
Area M Deposited Plan 541977	Easement		
Area CW Deposited Plan 541977	Easement		

Title Plan - LT 541977

Created Parcels

Parcels	Parcel Intent	Area	RT Reference
Area CX Deposited Plan 541977	Covenant - Land		
Lot 4 Deposited Plan 541977	Fee Simple Title	1.0010 Ha	911733
Lot 5 Deposited Plan 541977	Fee Simple Title	1.0000 Ha	911734
Lot 6 Deposited Plan 541977	Fee Simple Title	54.3132 Ha	911735
Area F Deposited Plan 541977	Easement		
Area G Deposited Plan 541977	Easement		
Area H Deposited Plan 541977	Easement		
Area EA Deposited Plan 541977	Easement		
Area EB Deposited Plan 541977	Easement		
Area ED Deposited Plan 541977	Easement		
Area EF Deposited Plan 541977	Easement		
Area EH Deposited Plan 541977	Easement		
Area N Deposited Plan 541977	Easement		
Area O Deposited Plan 541977	Easement		
Area EI Deposited Plan 541977	Easement		
Area EK Deposited Plan 541977	Easement		
Area CY Deposited Plan 541977	Covenant - Land		
Area CZ Deposited Plan 541977	Covenant - Land		
Area T Deposited Plan 541977	Easement		
Area CU Deposited Plan 541977	Covenant - Land		
Area CO Deposited Plan 541977	Covenant - Land		
Area EJ Deposited Plan 541977	Easement		
Area S Deposited Plan 541977	Easement		
Area EL Deposited Plan 541977	Easement		
Total Area		57.4262 Ha	

Our Ref: 40320

Cato Bolam
creating great places

Land Registration District	Plan Number
North Auckland	DP 541977
Territorial Authority	**TA Reference**
Auckland Council	SUB60315119 SUB60315119-A

MEMORANDUM OF EASEMENT(S)			
Purpose	Shown	Servient Tenement (Burdened Land)	Dominant Tenement (Benefited Land)
Right of Way, right to convey Electricity & Telecommunications	EA, EB, EC, G, NA, O & U	Lot 6 hereon	Lots 4 & 5 hereon
	ED	Lot 6 hereon	Lot 4 hereon
	EF, EG, EH, EI & N	Lot 5 hereon	Lot 6 hereon
	EJ & EL	Lot 4 hereon	Lot 6 hereon
Right to convey Electricity & Telecommunications	EL & S	Lot 4 hereon	Lot 5 hereon

SCHEDULE OF EXISTING EASEMENT(S) IN GROSS			
Purpose	Shown	Servient Tenement (Burdened Land)	Creating Document
Right to Convey Electricity	C	Lot 6 hereon	Transfer C640690.1
	G, H, I, J & R		Easement Instrument 9236051.4
	E & F	Lot 2 hereon	

SCHEDULE OF EXISTING EASEMENT(S)			
Purpose	Shown	Servient Tenement (Burdened Land)	Creating Document
Right of Way & telecommunications right	B, C & D	Lot 6 hereon	Easement Certificates D460766.5 & D611644.6
Electricity right	Q, T, U & V	Lot 6 hereon	Easement Certificate D460766.5
Telecommunications right	K, NA, & Q	Lot 6 hereon	Easement Certificate D460766.5
	I, L, M & N	Lot 5 hereon	Easement Certificate D460766.5
Transmit Electricity	O, P, T, U, V & X	Lot 6 hereon	Easement Instrument 6170820.9
Transmit Telecommunications	K, NA. O, P & X	Lot 6 hereon	Easement Instrument 6170820.9
	I, L, M & N	Lot 5 hereon	Easement Instrument 6170820.9


Proposed Covenants

Area CU is to be subject to a Land Covenant to protect the native bush within.

Areas CO, CX, CY & CZ are to be subject to Land Covenants to protect the riparian planting within.

Amalgamation Covenant

The owner of Lot 6 hereon, Allotments 32 & 35 & Part Allotments 30 & 31 (RT NA2100/21 Ltd), Allotment 54A Parish of Puhoi (RT NA31C/965), Lot 1 DP 179794 (RT NA105B/748) and Part Allotment 36 Parish of Puhoi (RT NA757/204 Ltd) shall not without the consent of the Council, transfer, lease or otherwise dispose of any of those parcels of land or any part thereof, except in conjunction with the other or others.

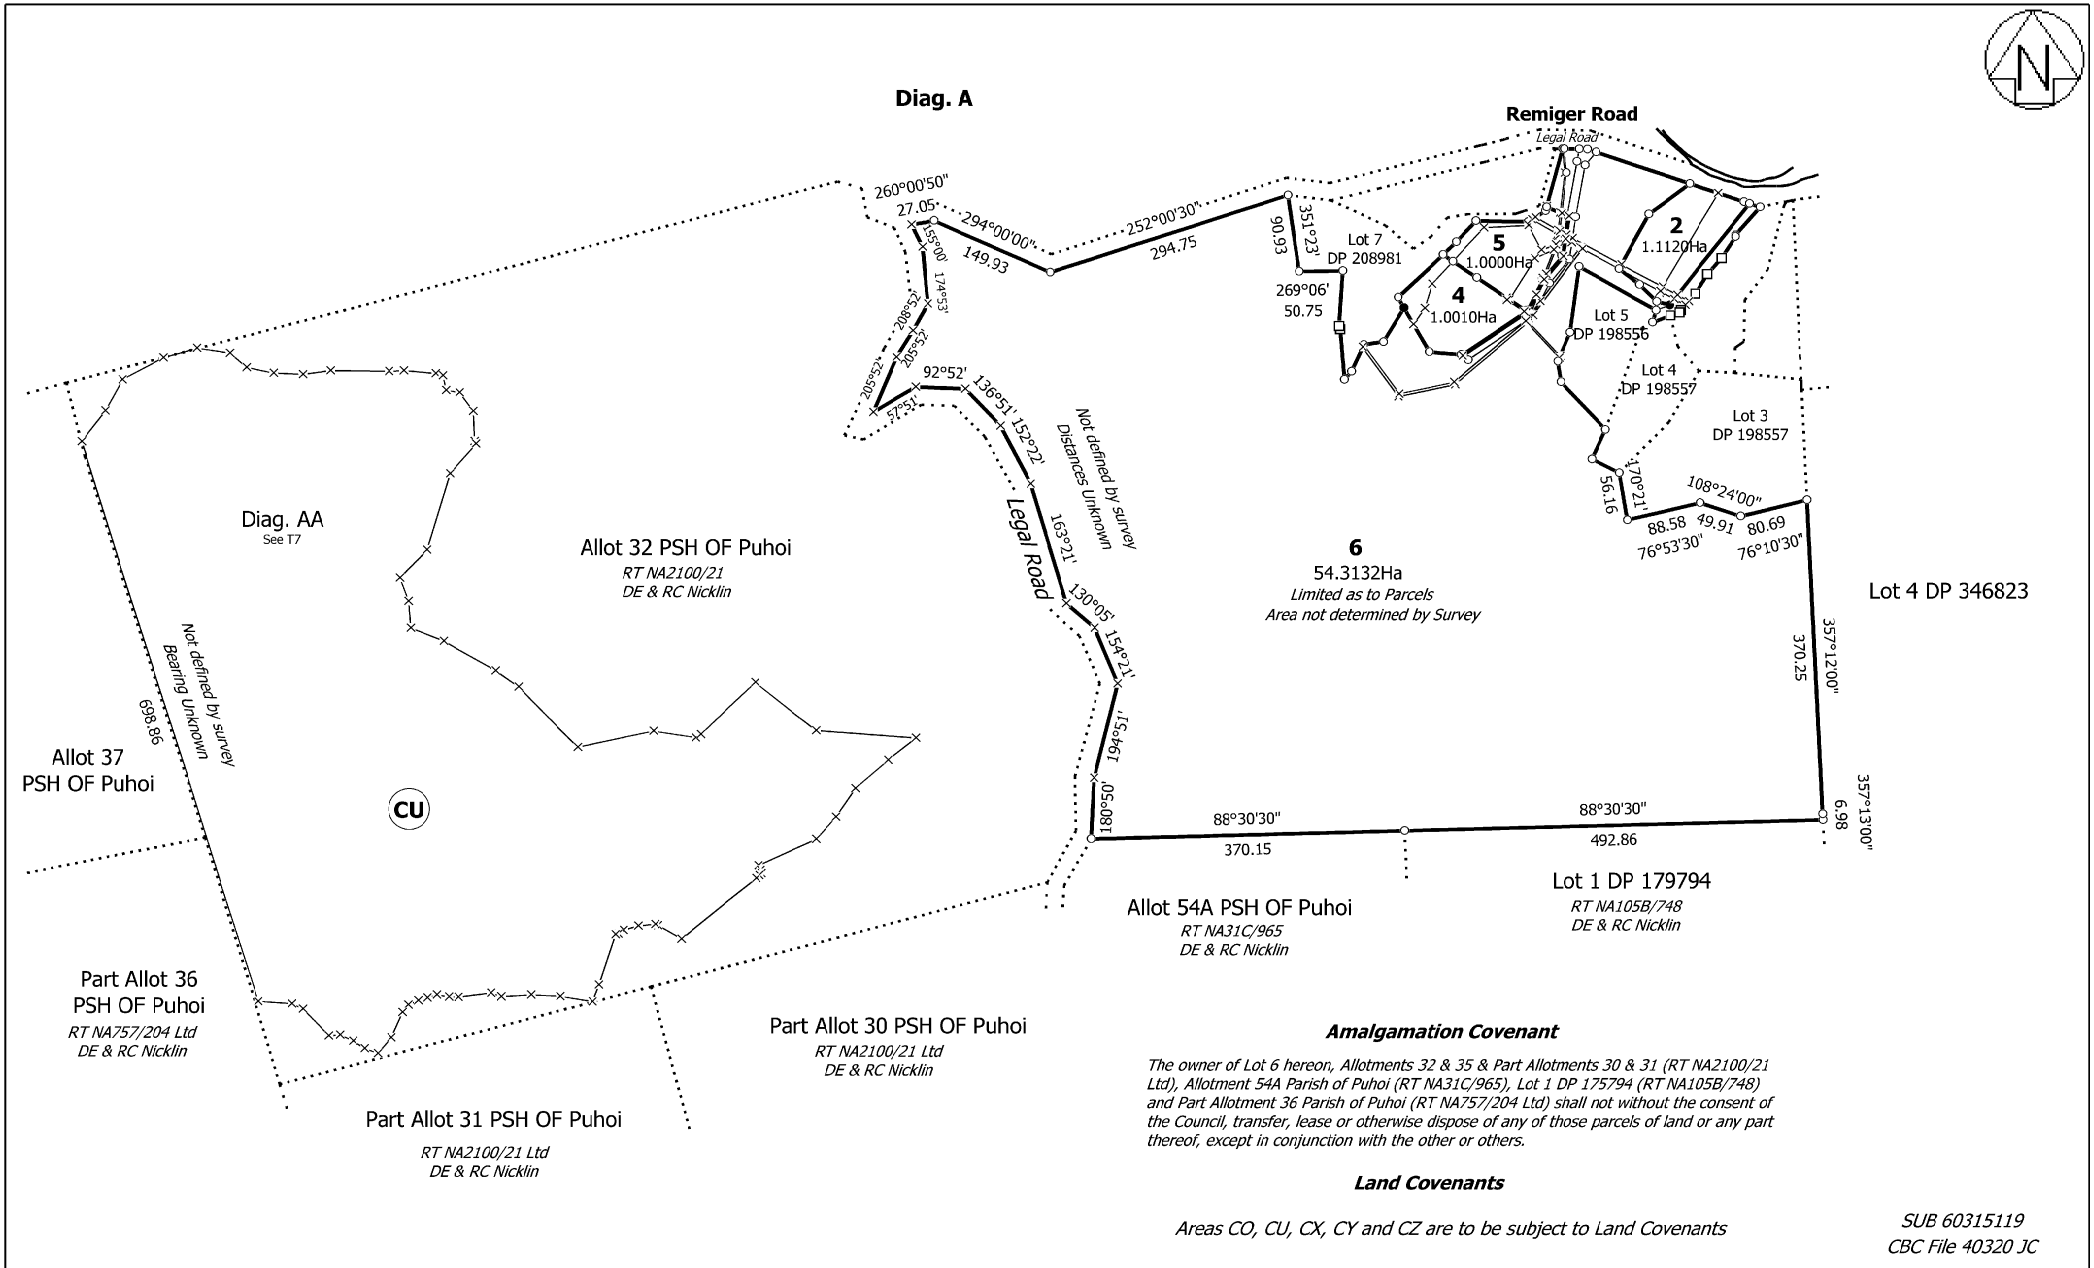

Amalgamation Covenant

The owner of Lot 6 hereon, Allotments 32 & 35 & Part Allotments 30 & 31 (RT NA2100/21 Ltd), Allotment 54A Parish of Puhoi (RT NA31C/965), Lot 1 DP 175794 (RT NA105B/748) and Part Allotment 36 Parish of Puhoi (RT NA757/204 Ltd) shall not without the consent of the Council, transfer, lease or otherwise dispose of any of those parcels of land or any part thereof, except in conjunction with the other or others.


Land Covenants

Areas CO, CU, CX, CY and CZ are to be subject to Land Covenants


SUB 60315119
CBC File 40320 JC

T 1/7

Land District: North Auckland Digitally Generated Plan Generated on: 02/06/2020 09:52am Page 5 of 11	Lots 2, 4, 5 & 6 Being Subdivision of Lot 8 DP 208981 & Land Covenant over Allot 32 Puhoi Parish	Surveyor: Bradley Mark Mowat Firm: Cato Bolam Consultants Ltd (Orewa)	Title Plan LT 541977 DRAFT

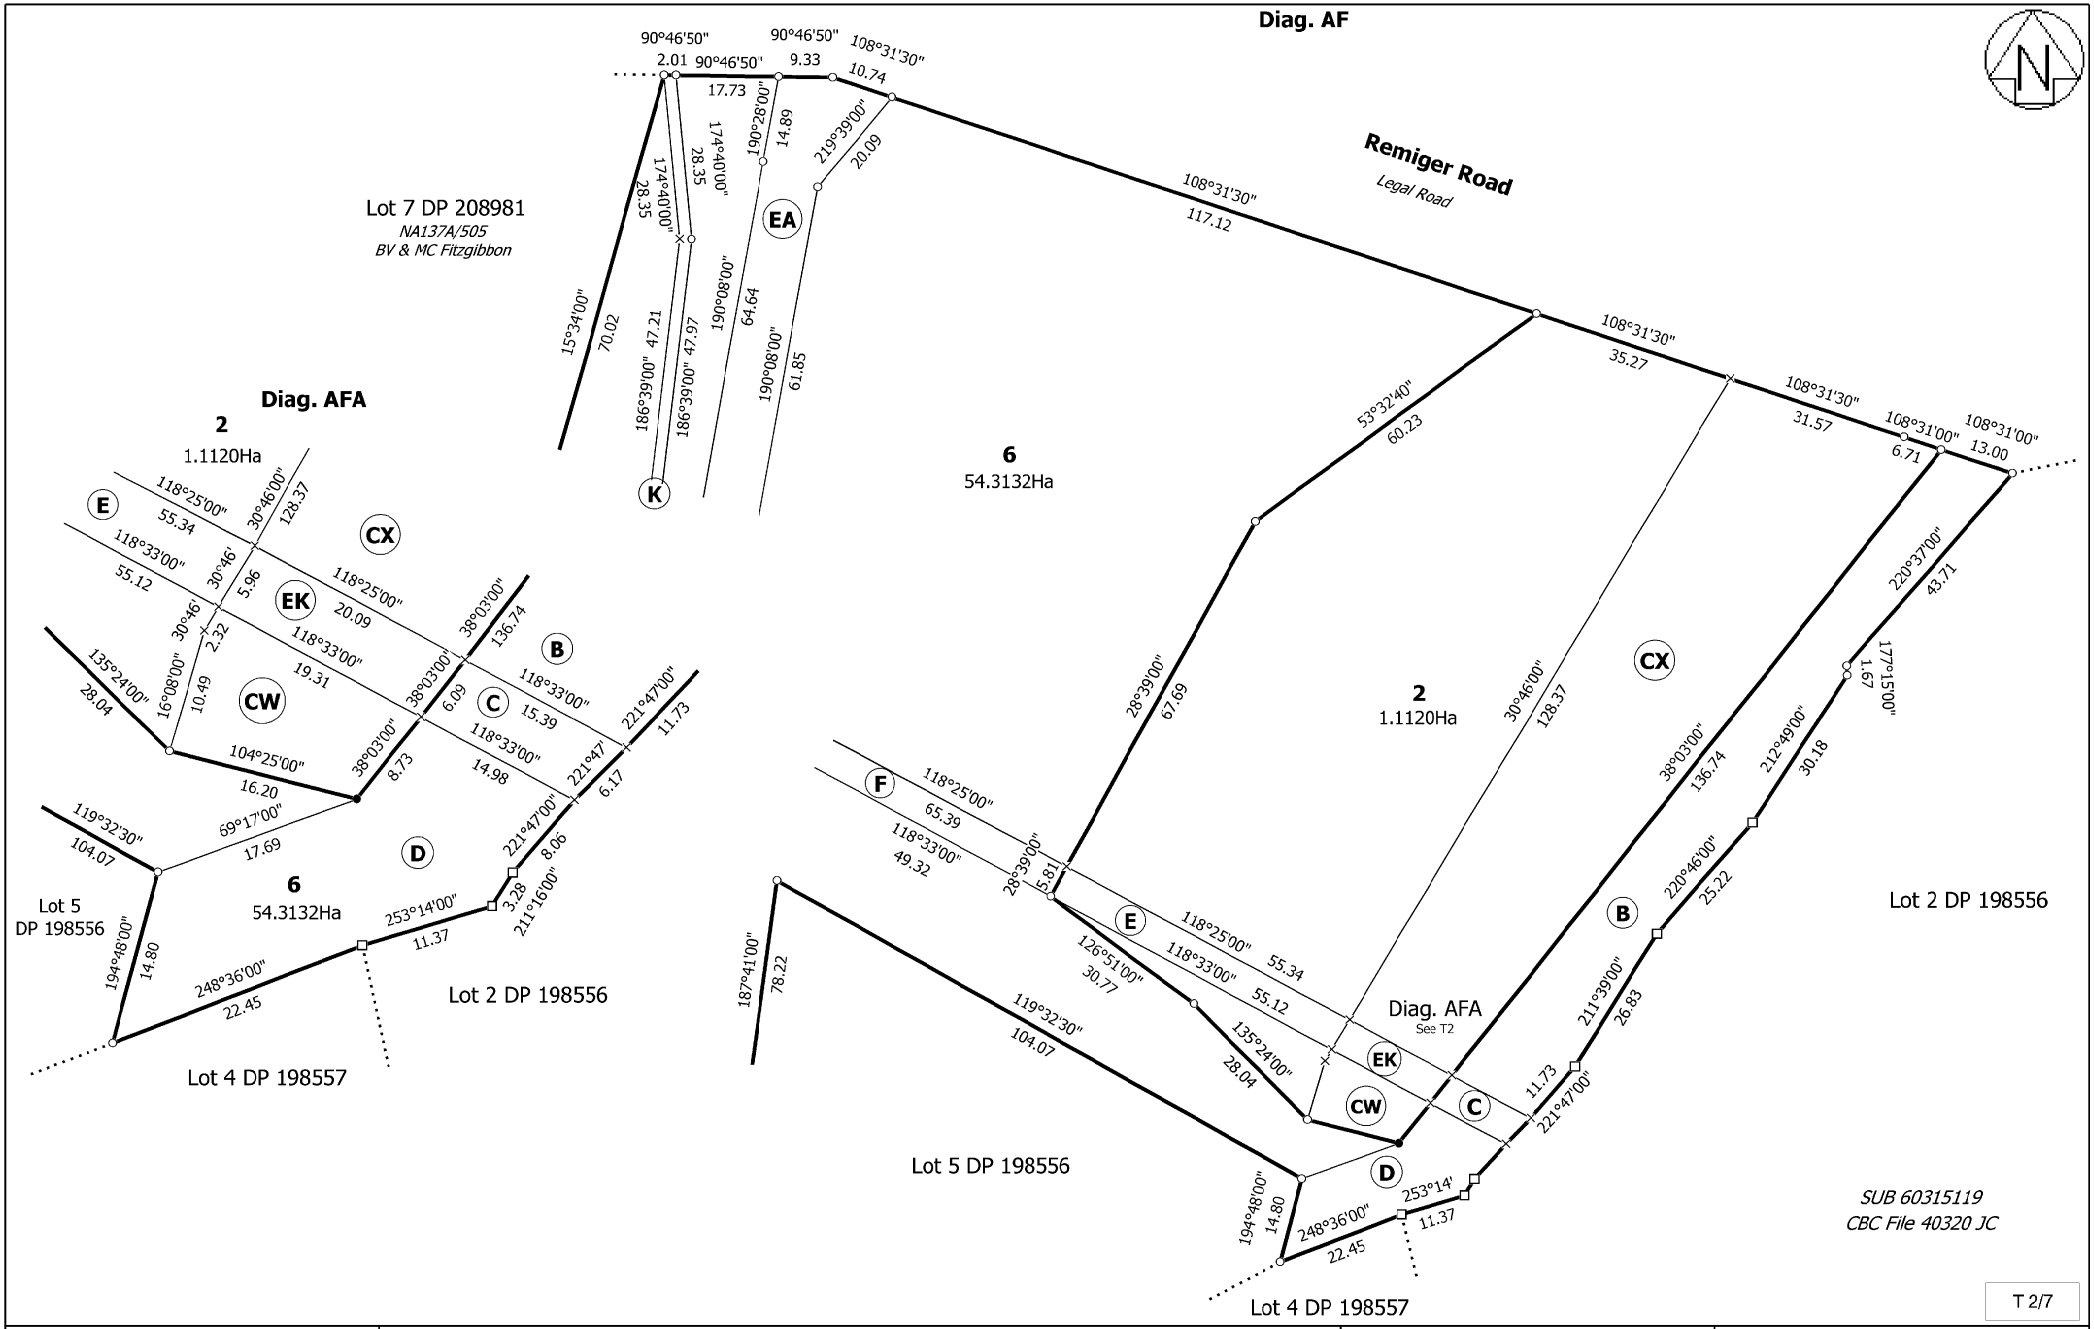


Land District: North Auckland Digitally Generated Plan Generated on: 02/06/2020 09:52am Page 6 of 11	Lots 2, 4, 5 & 6 Being Subdivision of Lot 8 DP 208981 & Land Covenant over Allot 32 Puhoi Parish	Surveyor: Bradley Mark Mowat Firm: Cato Bolam Consultants Ltd (Orewa)	Title Plan LT 541977 DRAFT

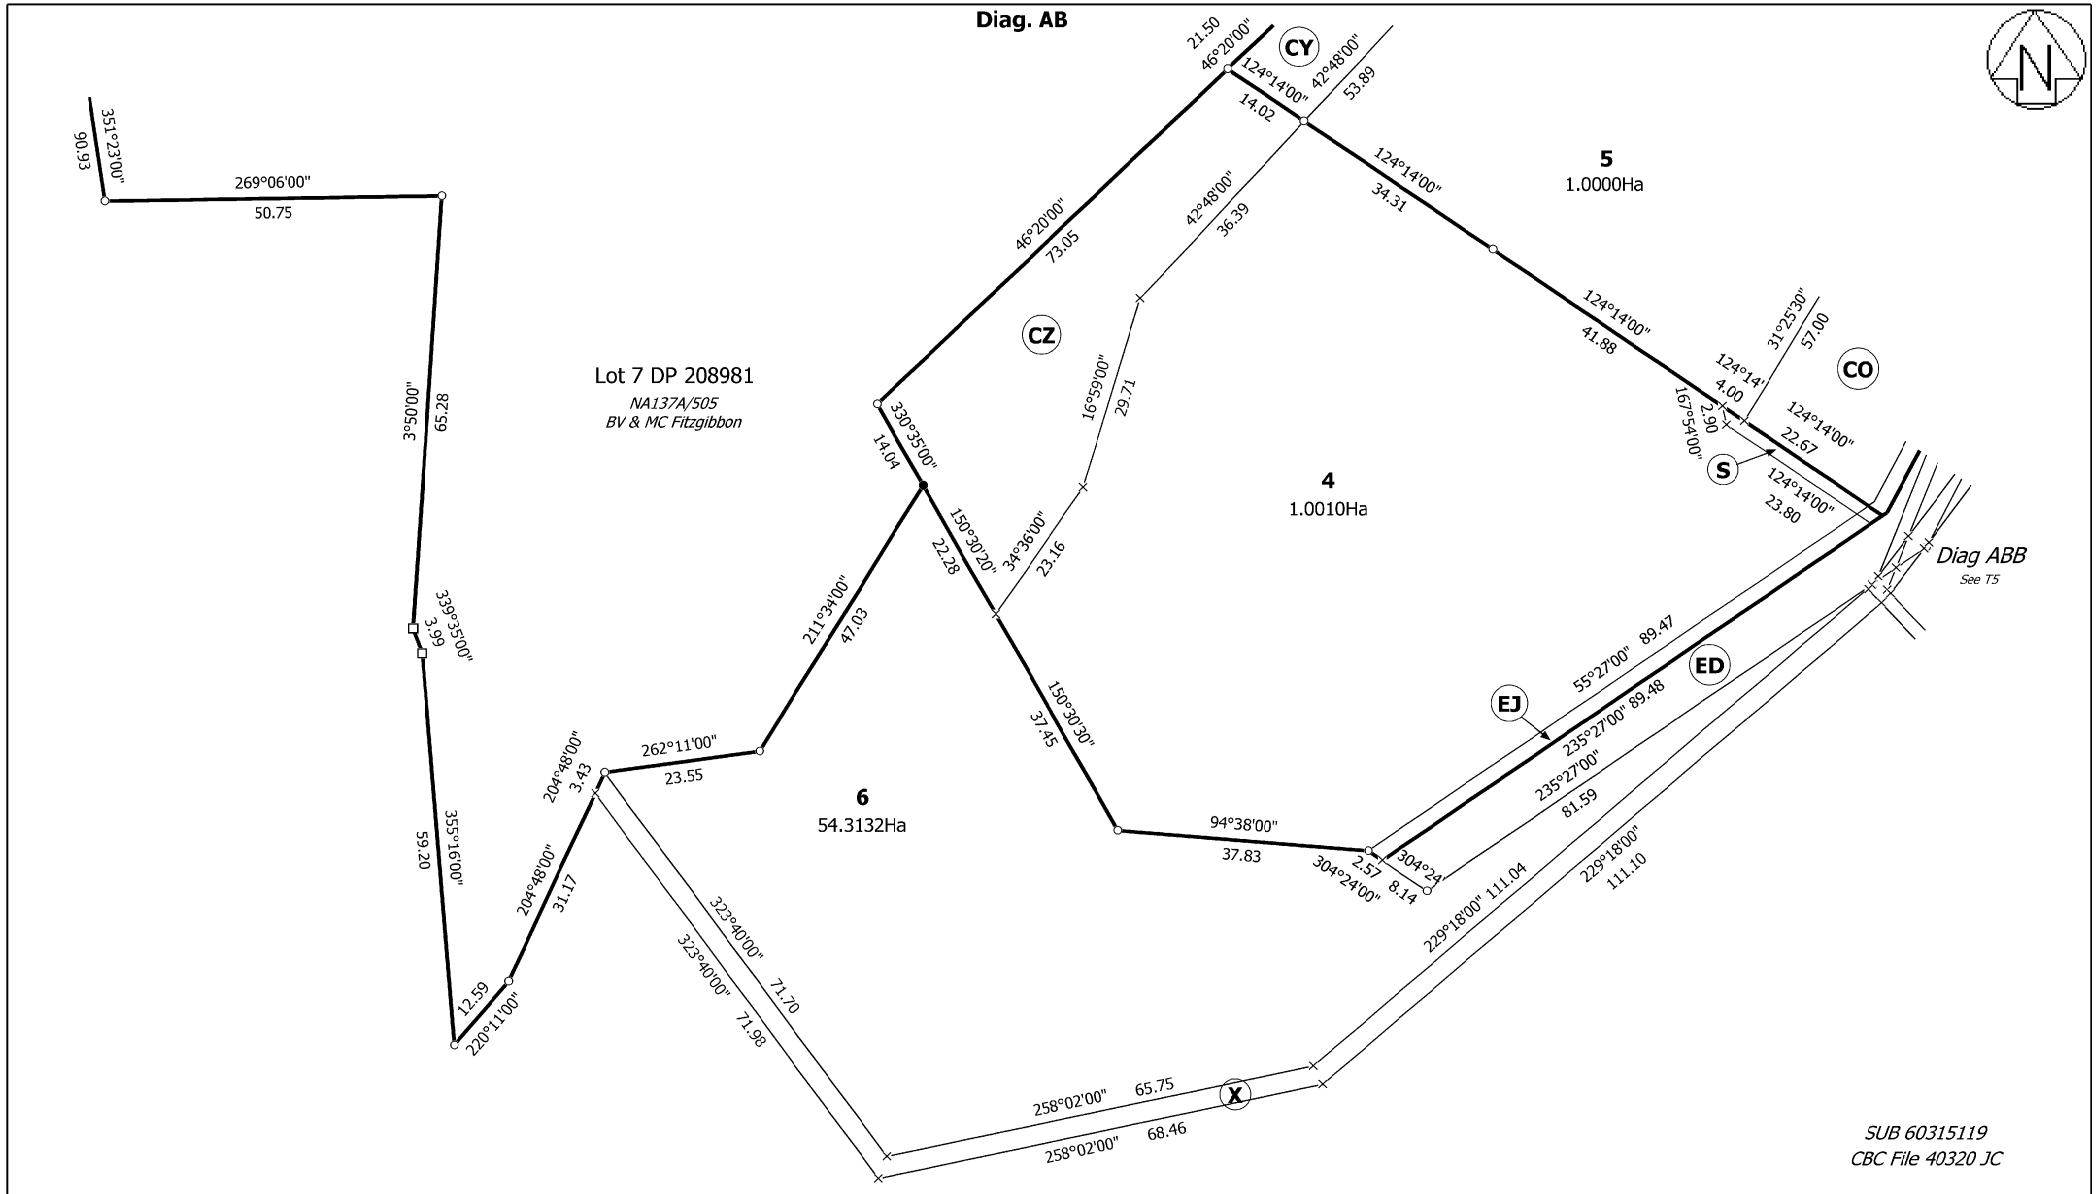

SUB 60315119
CBC File 40320 JC

T 3/7


Land District: North Auckland Digitally Generated Plan Generated on: 02/06/2020 09:52am Page 7 of 11	Lots 2, 4, 5 & 6 Being Subdivision of Lot 8 DP 208981 & Land Covenant over Allot 32 Puhoi Parish	Surveyor: Bradley Mark Mowat Firm: Cato Bolam Consultants Ltd (Orewa)	Title Plan LT 541977 DRAFT

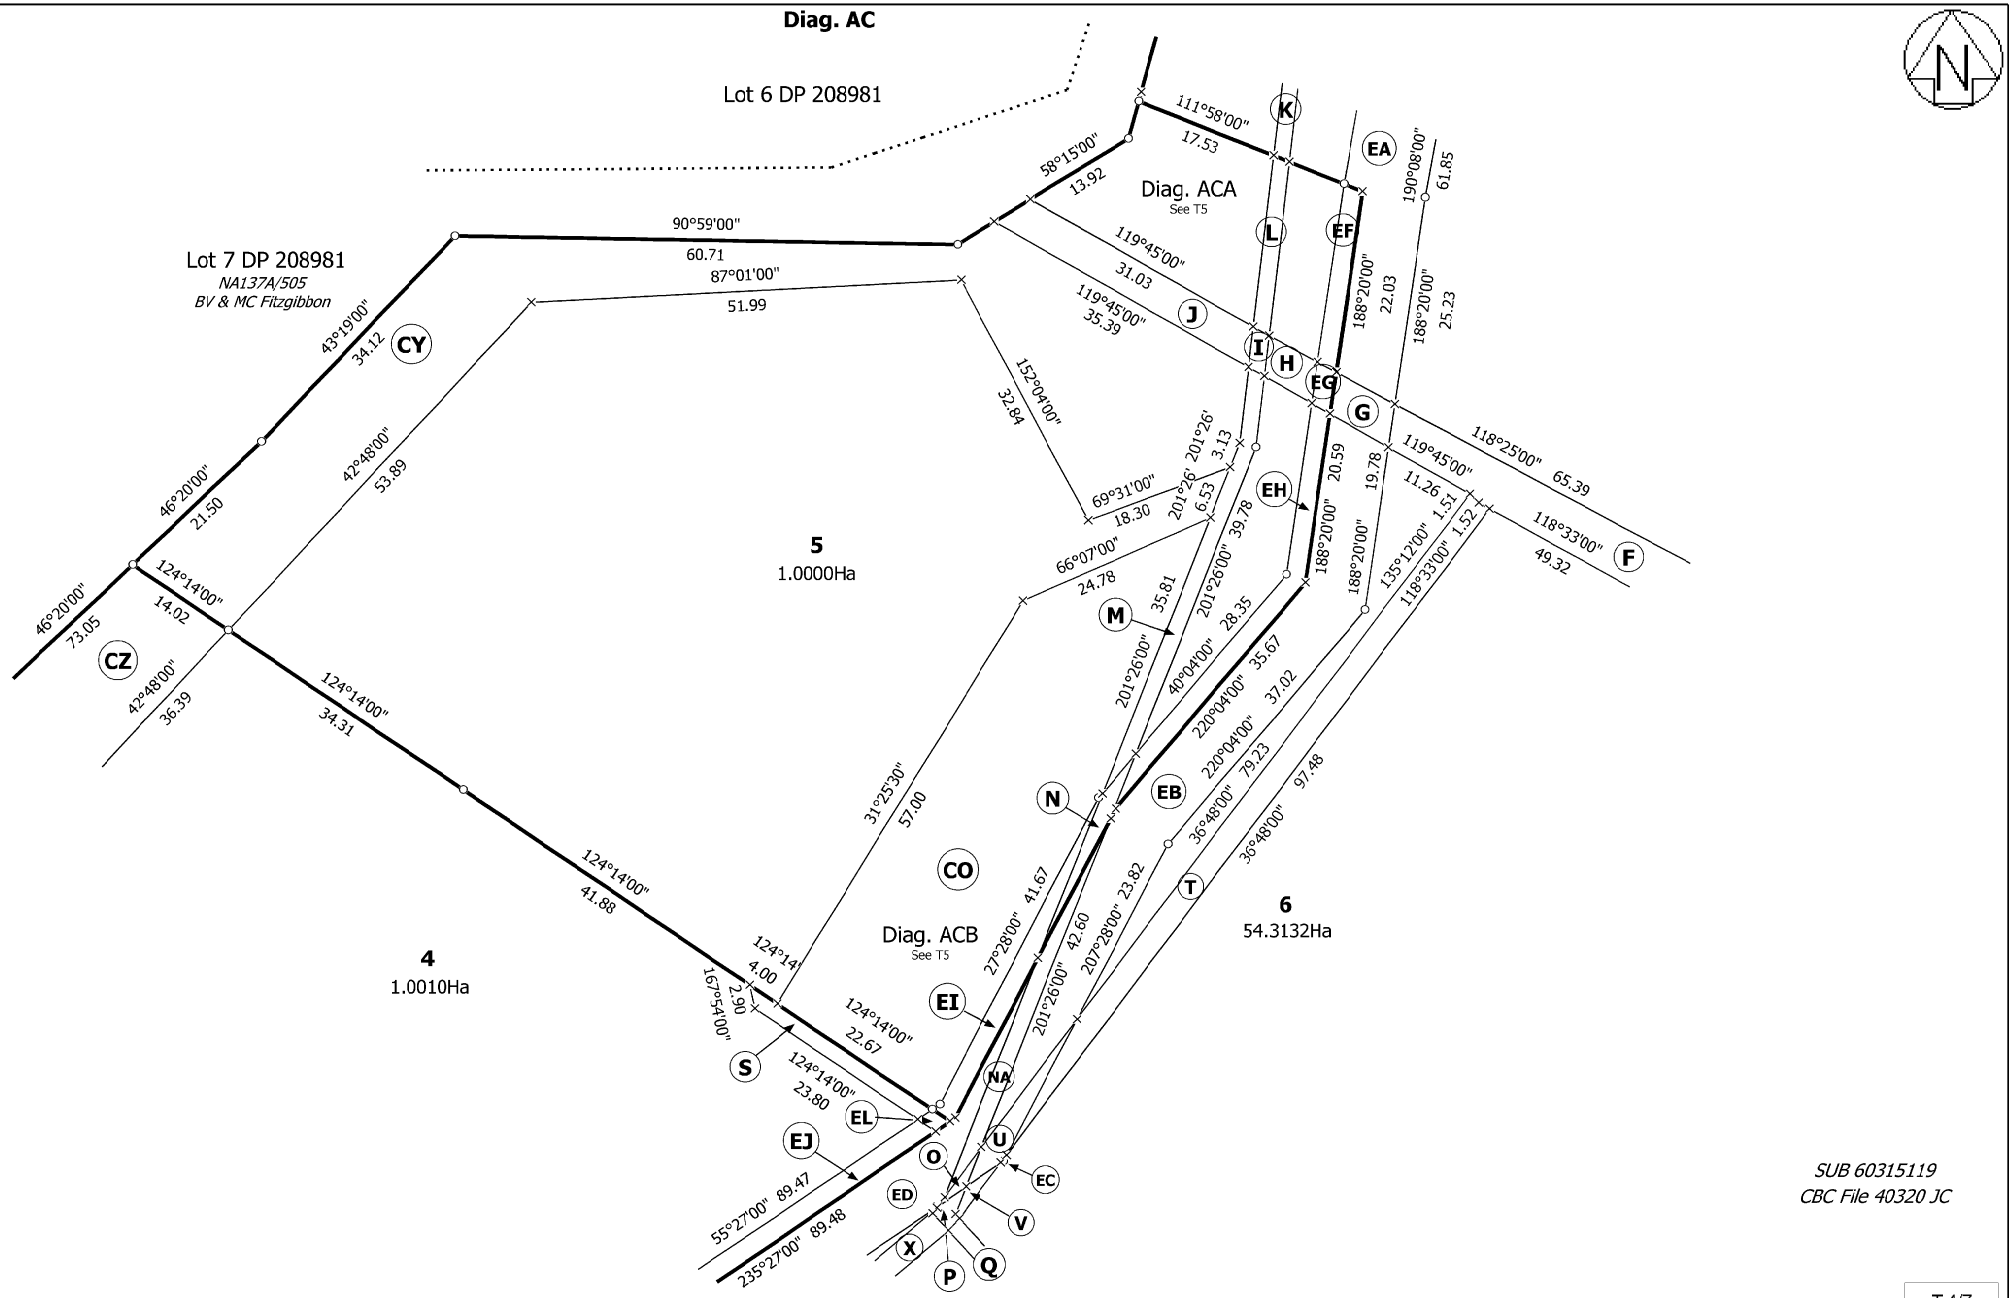


SUB 60315119
CBC File 40320 JC

T 4/7

Land District: North Auckland Digitally Generated Plan Generated on: 02/06/2020 09:52am Page 8 of 11	Lots 2, 4, 5 & 6 Being Subdivision of Lot 8 DP 208981 & Land Covenant over Allot 32 Puhoi Parish	Surveyor: Bradley Mark Mowat Firm: Cato Bolam Consultants Ltd (Orewa)	Title Plan LT 541977 DRAFT

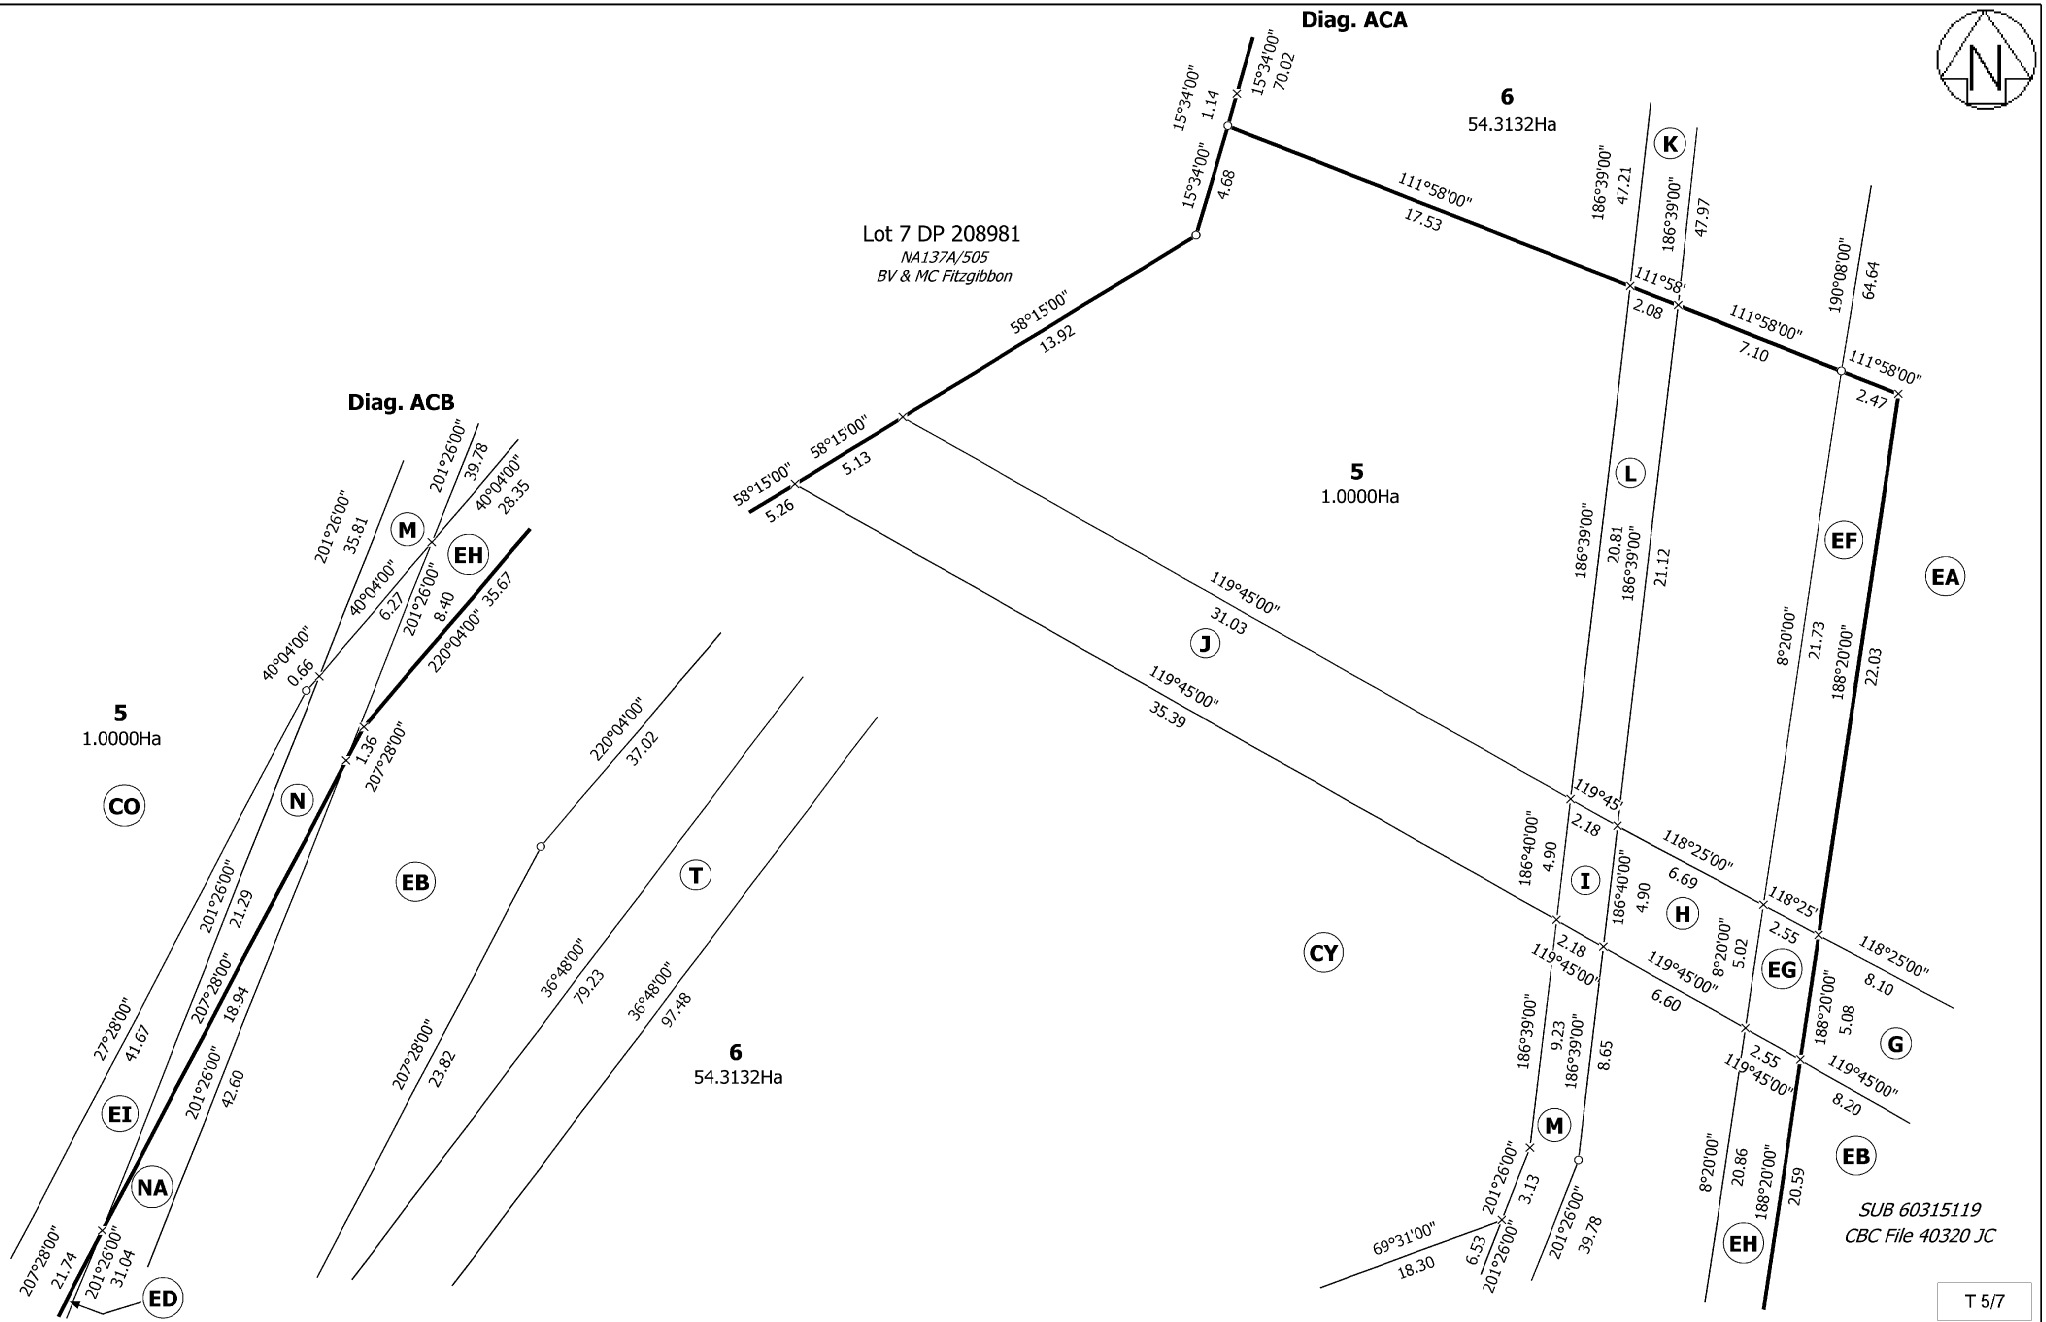


Land District: North Auckland Digitally Generated Plan Generated on: 02/06/2020 09:52am Page 9 of 11	Lots 2, 4, 5 & 6 Being Subdivision of Lot 8 DP 208981 & Land Covenant over Allot 32 Puhoi Parish	Surveyor: Bradley Mark Mowat Firm: Cato Bolam Consultants Ltd (Orewa)	Title Plan LT 541977 DRAFT

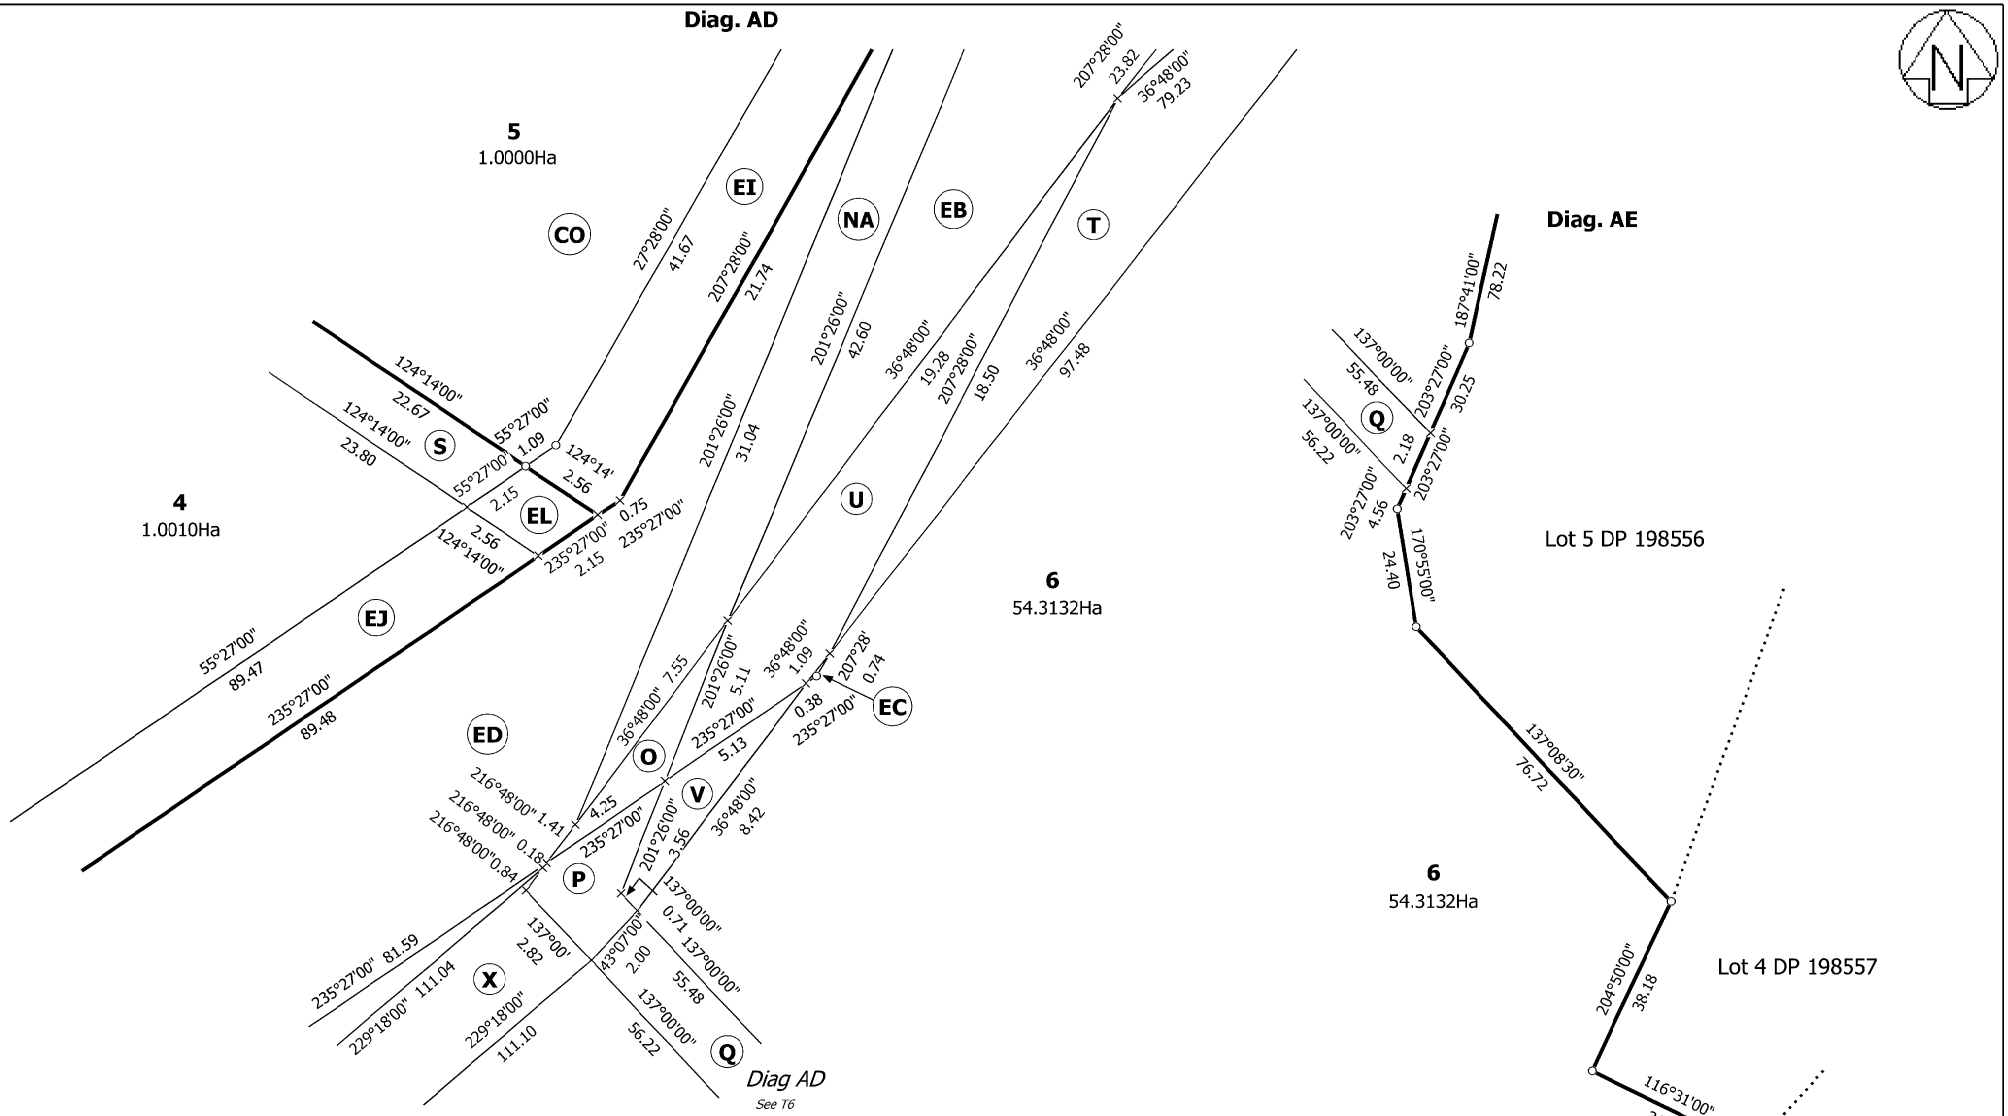

T 6/7

Land District: North Auckland Digitally Generated Plan Generated on: 02/06/2020 09:52am Page 10 of 11	Lots 2, 4, 5 & 6 Being Subdivision of Lot 8 DP 208981 & Land Covenant over Allot 32 Puhoi Parish	Surveyor: Bradley Mark Mowat Firm: Cato Bolam Consultants Ltd (Orewa)	Title Plan LT 541977 DRAFT

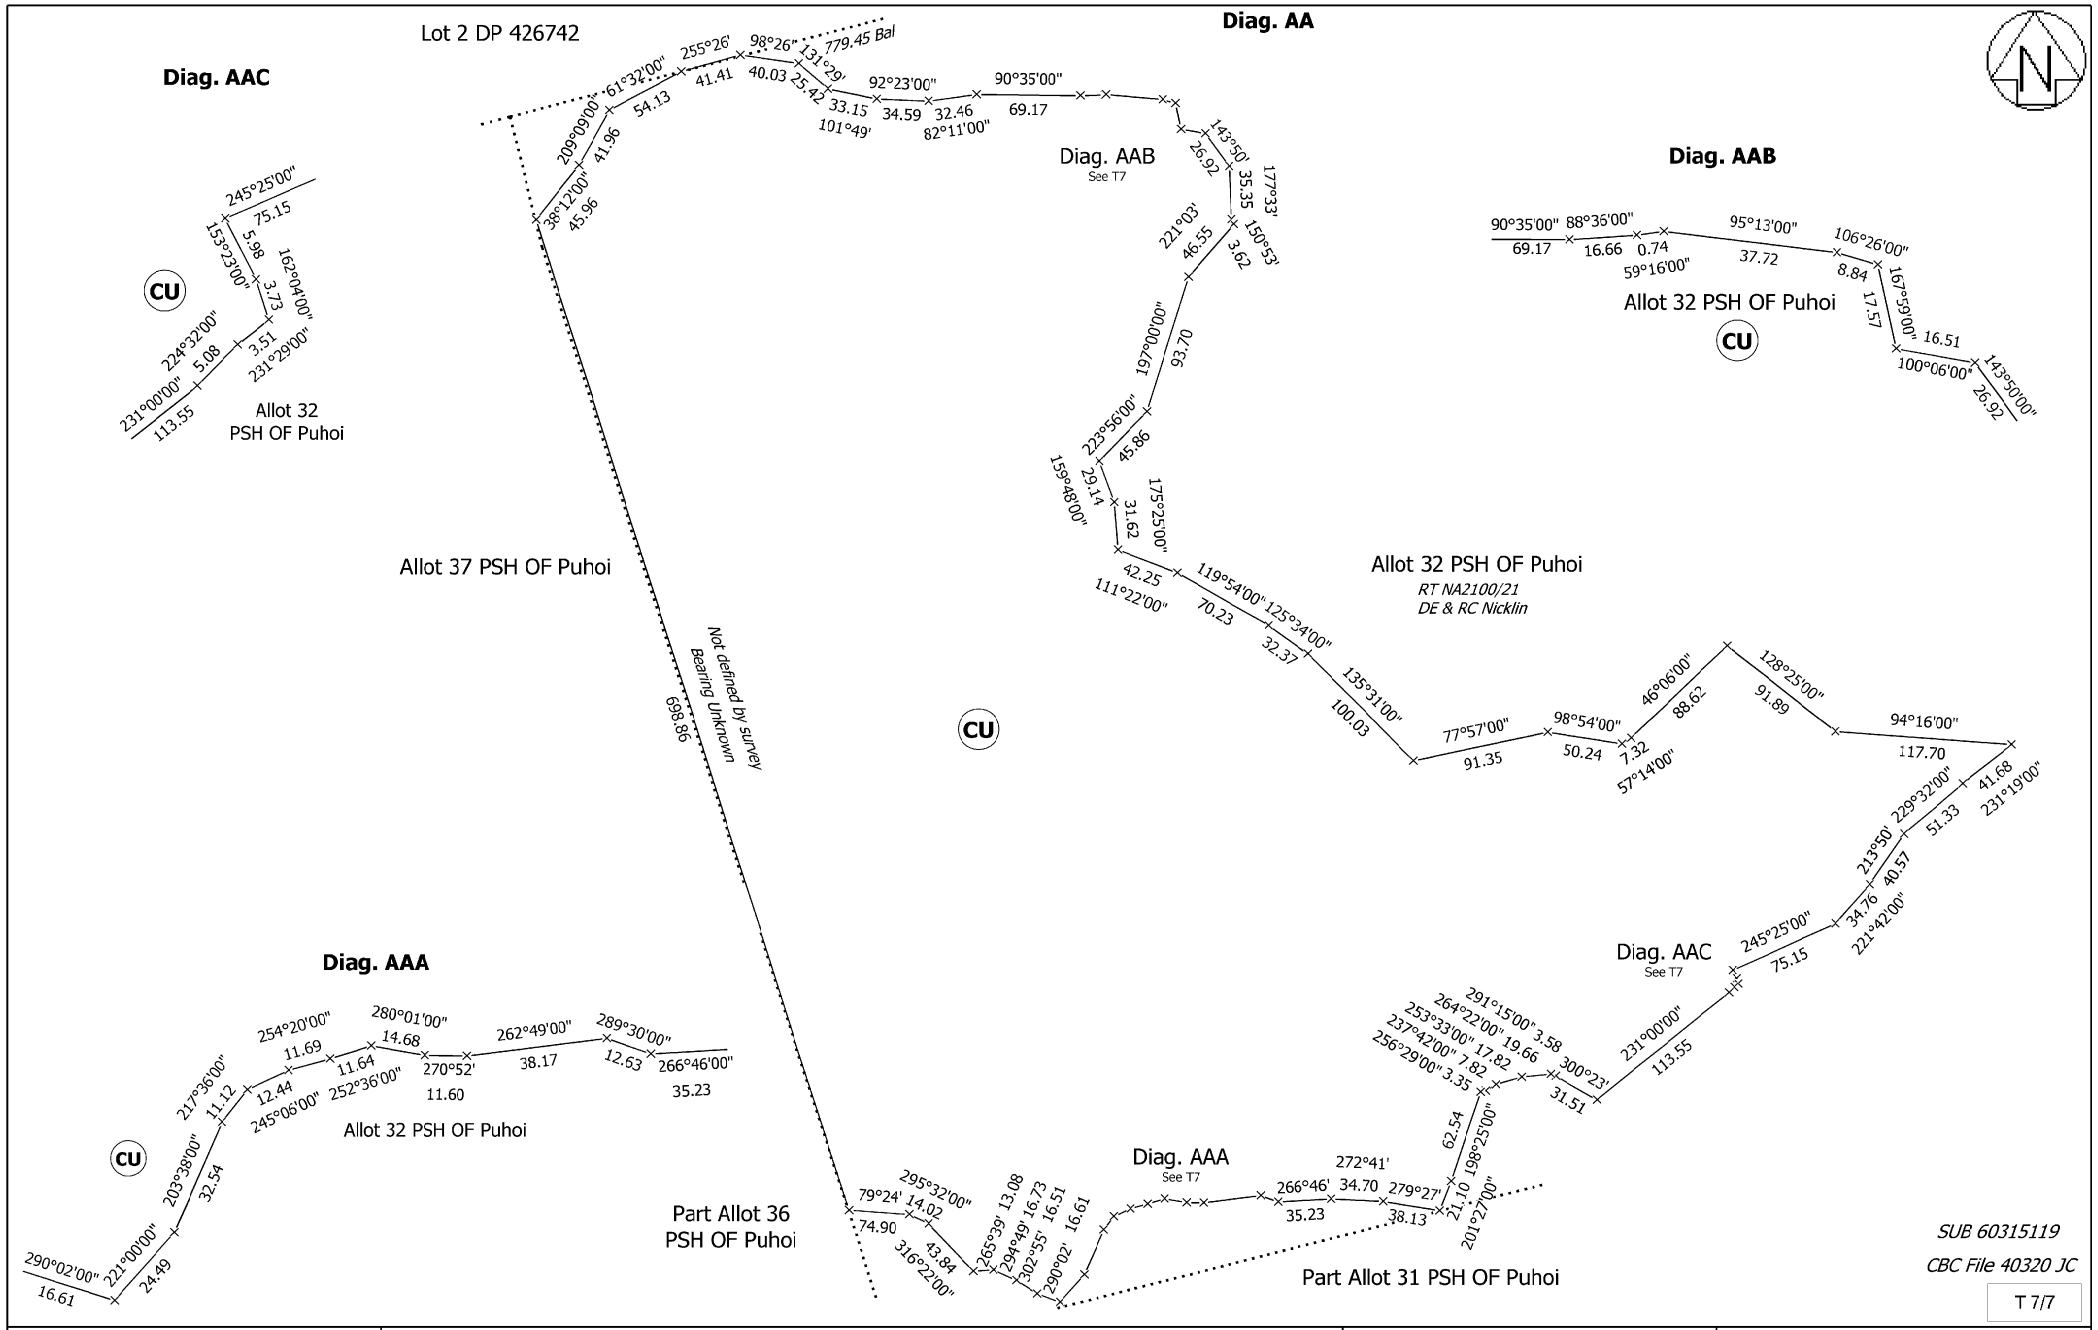

Land District: North Auckland Digitally Generated Plan Generated on: 02/06/2020 09:52am Page 11 of 11	Lots 2, 4, 5 & 6 Being Subdivision of Lot 8 DP 208981 & Land Covenant over Allot 32 Puhoi Parish	Surveyor: Bradley Mark Mowat Firm: Cato Bolam Consultants Ltd (Orewa)	Title Plan LT 541977 DRAFT