
APPROVED JThomson
DATE 20/11/18
REF SUB60315119

Areas (CP)-(CW) (52.37ha) are to be subject to land covenants to protect native bush .

Areas (CO)-(CX)-(CZ)-(Z) (0.9ha) are to be subject to land covenants to protect riparian planting.

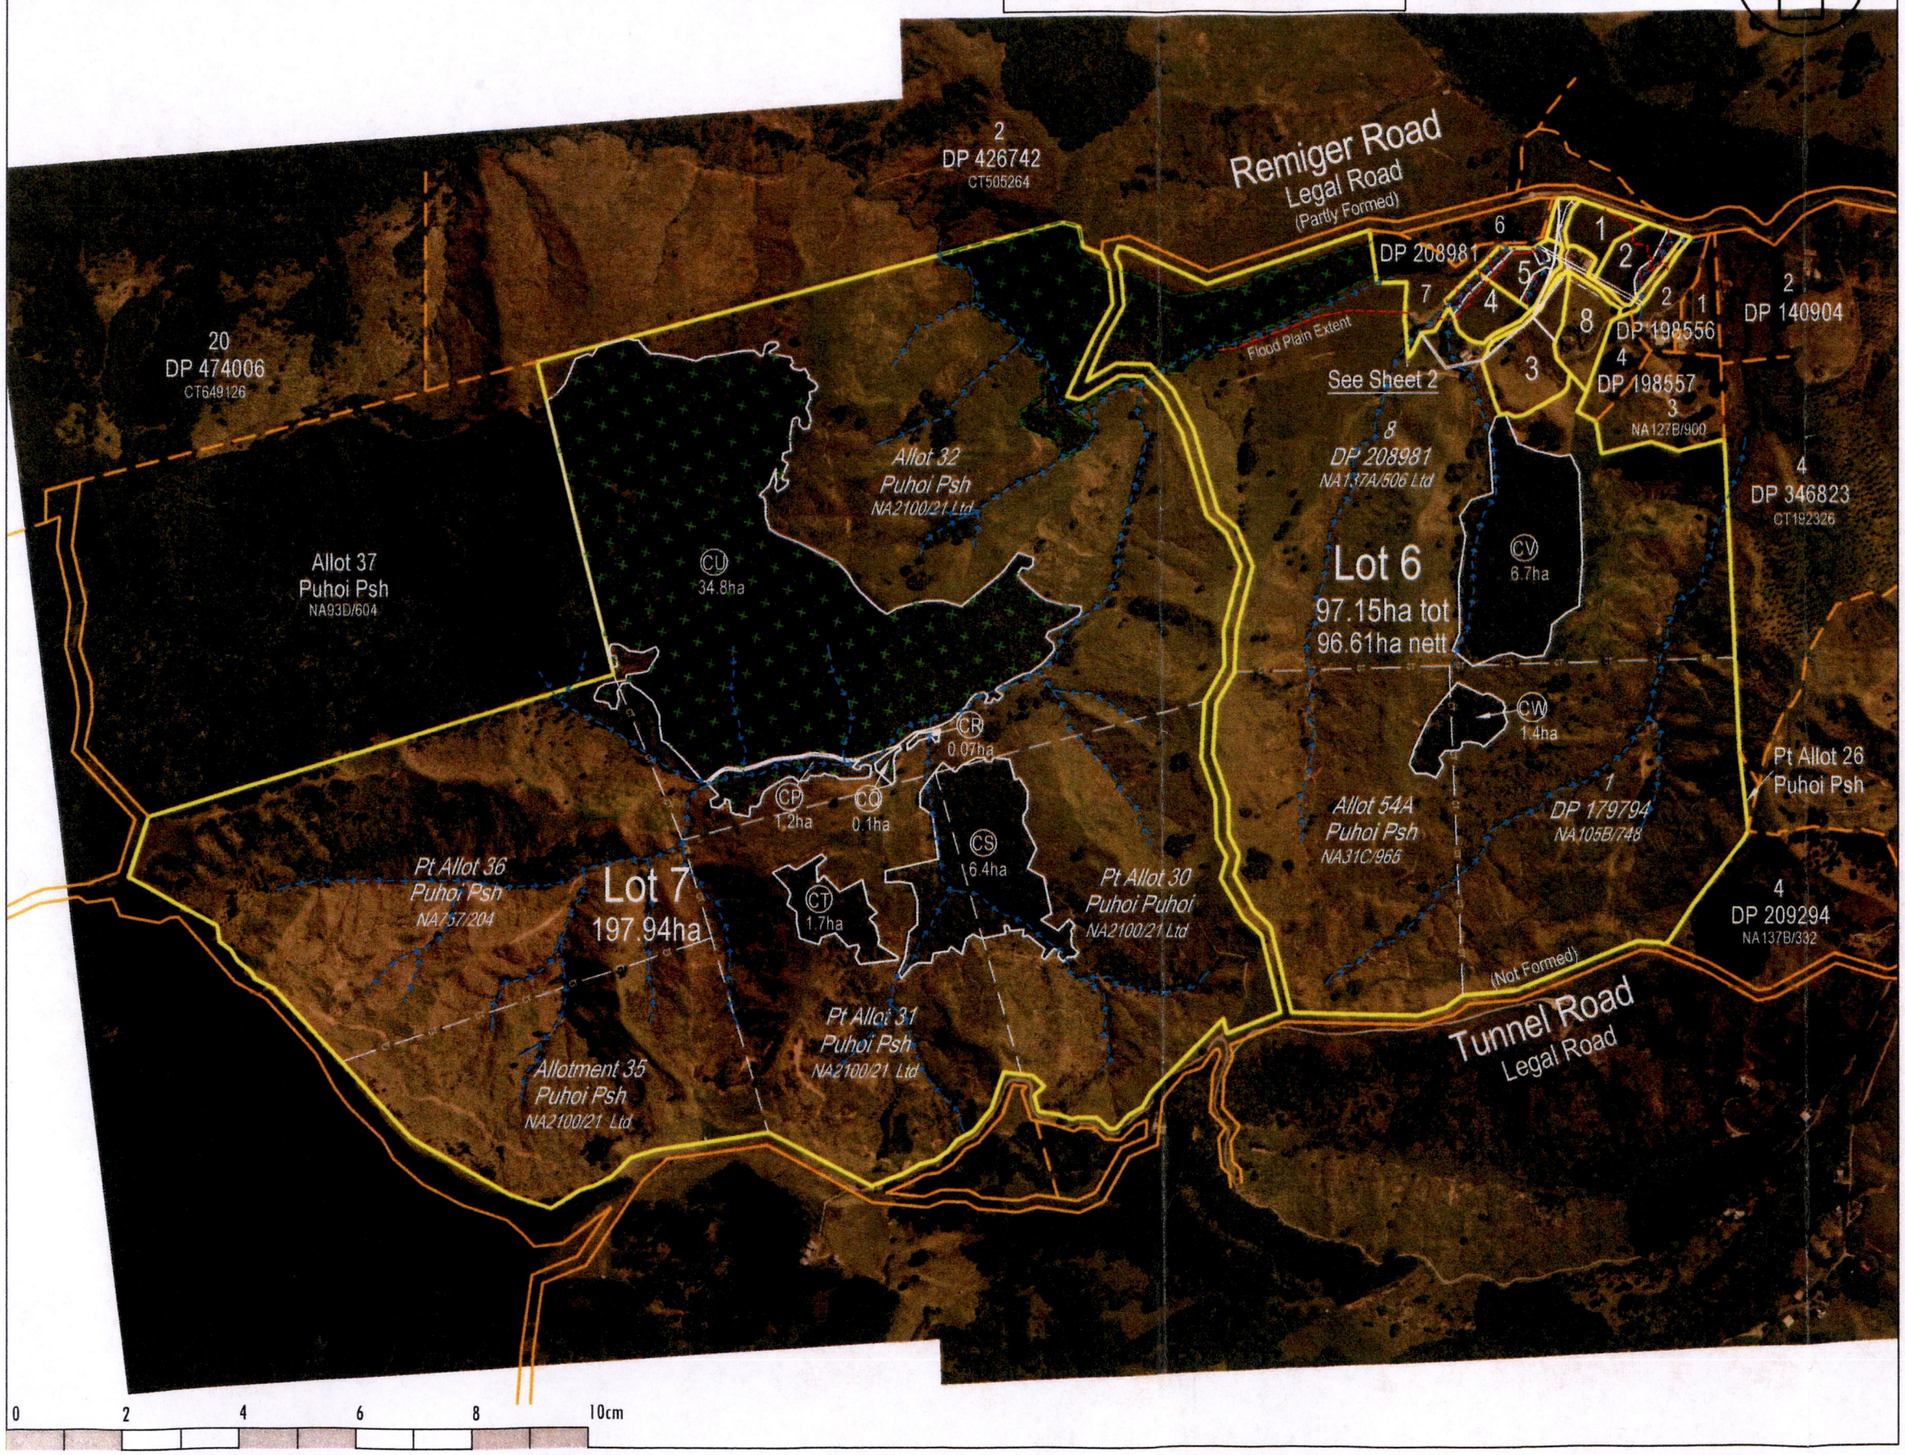

This drawing and design remains the property of Cato Bolam Consultants ltd and may not be reproduced without the written permission of Cato Bolam Consultants ltd.

This plan and accompanying report(s) have been prepared for the purpose of obtaining a resource consent only and for no other purpose. Use of this plan and or the information on it for any other purpose is at the user's risk

AUCKLAND COUNCIL Rodney Section

COMPRISED IN CT	NA137A/506Ltd	57.4262ha
	NA105B/748	24.1140ha
	NA31C/965	21.6507ha
	NA757/204Ltd	37.0692ha
	NA2100/21Ltd	160.87ha
	NA127B/898	1.1705ha
TOTAL AREA		302.3006ha

LEVELS ARE IN TERMS OF LANDS AND SURVEY DATUM, AREAS AND MEASUREMENTS ARE SUBJECT TO SURVEY.

- Riparian Margin Protection
- Significant Ecological Area
- Proposed Building Area
- Watercourse
- Extent of Flood Plain

Amendment

R5	ROW EE & Rip Covnt CO added	LS	05.18
R4	Bdys Lots 1 & 6 amended. Lot 8 added	LS	01.18
R3	Bdys Lots 1,2 & 6 amended	LS	12.17
R2	Flood Plain Added Lots 1 & 2	LS	11.17
	REVISION (DESCRIPTIONS)	NAME	DATE

	NAME	DATE
SURVEYED		
DESIGNED		
DRAWN	LS	09.17
CHECKED	MG	09.17
APPROVED	MG	09.17

CATO BOLAM CONSULTANTS
SURVEYORS PLANNERS ENGINEERS

CATO BOLAM CONSULTANTS LTD
19 Tamariki Avenue
PO Box 157
Orewa 0946
phone 09-427 0072
fax 09-426 7331
email catobolam@catobolam.co.nz

CLIENT
R.C. & D.E. NICKLIN
53B REMIGER ROAD
PUHOI


TITLE
LOTS 1 - 8 BEING
PROPOSED SUBDIVISION OF
LOT 8 DP 208981, LOT 5 DP 198556
LOT 1 DP 179794, ALLOTS 32,35,54A &
PT ALLOTS 30,31,36 PARISH OF PUHOI

ORIGINAL SCALE 1:10000	ORIGINAL SIZE A3	REVISION NO	R5
DATE SEP 2017	CAD REFERENCE 40320-1200	SHEET NO	1 OF 2
DIRECTORY SYNERGY 40320\Drwgs\Schemes		JOB NO	1200 40320

APPROVED HEThomson
DATE 20/11/18
REF SUB60315119

EXISTING EASEMENTS			
PURPOSE	SHOWN	SERVIENT TENEMENT	CREATED BY
RIGHT OF WAY & TELECOMMUNICATIONS	(B)(C)(D)	LOT 6 HEREON	E.C. D460766.5 E.C. D611644.6
RIGHT TO CONVEY TELECOMMUNICATIONS	(K)(N)(O)(W)(Y)	LOT 5 HEREON	E.C. D460766.5 E.I. 6170820.9
	(I)(L)(M)	LOT 3 HEREON	
	(P)(Q)(X)	LOT 6 HEREON	
RIGHT TO CONVEY ELECTRICITY	(P)(Q)(T)(V)(X)	LOT 3 HEREON	
	(O)(S)(U)(W)(Y)		

EXISTING EASEMENTS IN GROSS			
PURPOSE	SHOWN	SERVIENT TENEMENT	CREATED BY
RIGHT TO CONVEY ELECTRICITY	(C)(G)(R)	LOT 6 HEREON	E.I. 9236051.4
	(E)	LOT 2 HEREON	
	(F)	LOT 1 HEREON	
	(H)(I)(J)(Z)	LOT 5 HEREON	

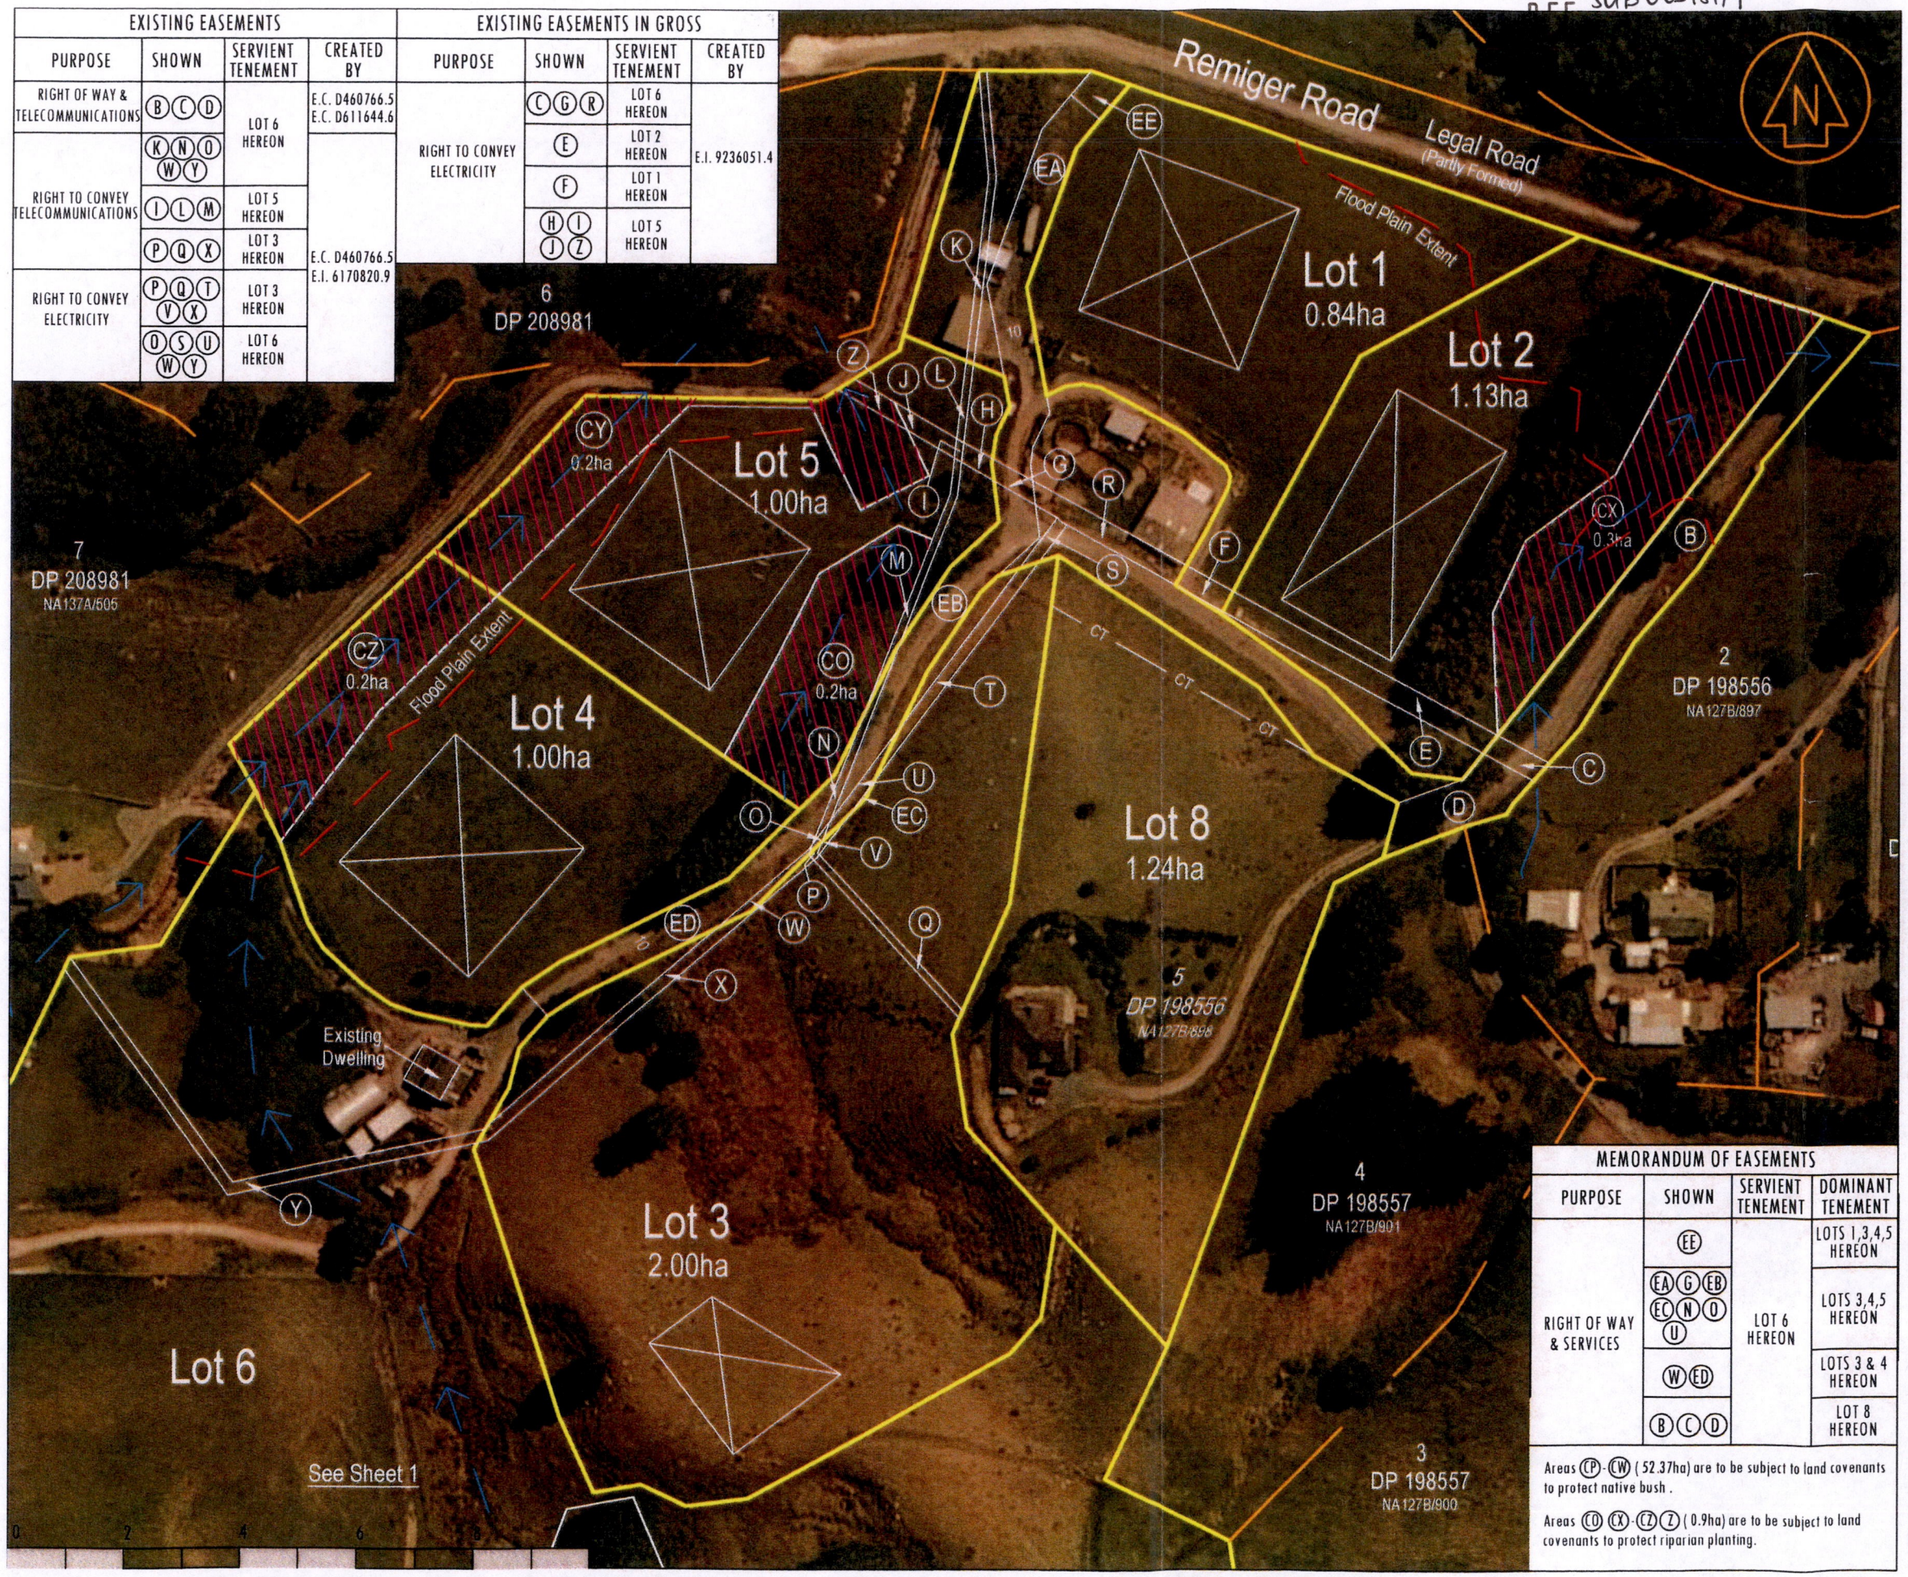

MEMORANDUM OF EASEMENTS			
PURPOSE	SHOWN	SERVIENT TENEMENT	DOMINANT TENEMENT
RIGHT OF WAY & SERVICES	(EE)	LOT 6 HEREON	LOTS 1,3,4,5 HEREON
	(EA)(G)(EB)(EC)(N)(O)(U)		LOTS 3,4,5 HEREON
	(W)(ED)		LOTS 3 & 4 HEREON
	(B)(C)(D)		LOT 8 HEREON

Areas (CP)-(CW) (52.37ha) are to be subject to land covenants to protect native bush.

Areas (CO)(CX)-(CZ)(Z) (0.9ha) are to be subject to land covenants to protect riparian planting.

This drawing and design remains the property of Cato Bolam Consultants ltd and may not be reproduced without the written permission of Cato Bolam Consultants ltd.

This plan and accompanying report(s) have been prepared for the purpose of obtaining a resource consent only and for no other purpose. Use of this plan and or the information on it for any other purpose is at the user's risk

AUCKLAND COUNCIL Rodney Section

COMPRISED IN CT	NA137A/506Ltd	57.4262ha
	NA105B/748	24.1140ha
	NA31C/965	21.6507ha
	NA757/204Ltd	37.0692ha
	NA2100/21Ltd	160.87ha
	NA127B/898	1.1705ha
TOTAL AREA		302.3006ha

LEVELS ARE IN TERMS OF LANDS AND SURVEY DATUM, AREAS AND MEASUREMENTS ARE SUBJECT TO SURVEY.

Riparian Margin Protection

Significant Ecological Area

Proposed Building Area

Watercourse

Extent of Flood Plain

Amendment

R5	ROW EE & Rip Covnt CO added	LS	05.18
R4	Bdys Lots 1 & 6 amended. Lot 8 added	LS	01.18
R3	Bdys Lots 1,2 & 6 amended	LS	12.17
R2	Flood Plain Added Lots 1 & 2	LS	11.17
	REVISION (DESCRIPTIONS)	NAME	DATE

	NAME	DATE
SURVEYED		
DESIGNED		
DRAWN	LS	09.17
CHECKED	MG	09.17
APPROVED	MG	09.17

CATO BOLAM CONSULTANTS
SURVEYORS PLANNERS ENGINEERS

CATO BOLAM CONSULTANTS LTD
19 Tamariki Avenue
PO Box 157
Orewa 0946
phone 09-427 0072
fax 09-426 7331
email catobolam@catobolam.co.nz

CLIENT
R.C. & D.E. NICKLIN
53B REMIGER ROAD
PUHOI

TITLE
LOTS 1 - 8 BEING
PROPOSED SUBDIVISION OF
LOT 8 DP 208981, LOT 5 DP 198556
LOT 1 DP 179794, ALLOTS 32,35,54A &
PT ALLOTS 30,31,36 PARISH OF PUHOI

ORIGINAL SCALE	1:10000	ORIGINAL SIZE	A3
DATE	SEP 2017	CAD REFERENCE	40320-1200
DIRECTORY SYNERGY 40320:Drwgs:Schemes			
REVISION NO	R5		
SHEET NO 2 OF 2			
JOB NO	1200 40320		