COMPUTER FREEHOLD REGISTER
UNDER LAND TRANSFER ACT 1952
Limited as to Parcels

Search Copy

R.W. Muir
Registrar-General
of Land

Identifier	**NA137A/506**
Land Registration District	**North Auckland**
Date Issued	05 October 2004

Prior References
NA127B/902 NA2100/21

Estate	Fee Simple
Area	57.4262 hectares more or less
Legal Description	Lot 8 Deposited Plan 208981

Proprietors
Raymond Charles Nicklin as to a 1/2 share
Desma Elizabeth Nicklin as to a 1/2 share

Interests

C269124.5 Mortgage to Bank of New Zealand - 28.5.1991 at 9.40 am

Subject to an electricity right (in gross) over parts marked C, L, M and S on DP 208981 in favour of (now) Vector Limited created by Transfer C640690.1 - 15.8.1994 at 9.17 am

Subject to a right of way over parts marked B, C and D and to telecommunications rights over parts marked B, C, D, M, O, P and Q and to an electricity right over parts marked Q and R on DP 208981 specified in Easement Certificate D460766.5 - produced 9.12.1999 at 12.34 pm and entered 1.2.2000 at 9.00 am

Some of the easements specified in Easement Certificate D460766.5 are subject to Section 243 (a) Resource Management Act 1991

Appurtenant hereto are electricity rights specified in Easement Certificate D460766.5 - produced 9.12.1999 at 12.34 pm and entered 1.2.2000 at 9.00 am

Subject to a right of way and to a telecommunications right over parts marked B, C and D on DP 208981 specified in Easement Certificate D611644.6 - produced 11.6.2001 at 9.00 am and entered 2.7.2001 at 9.00 am

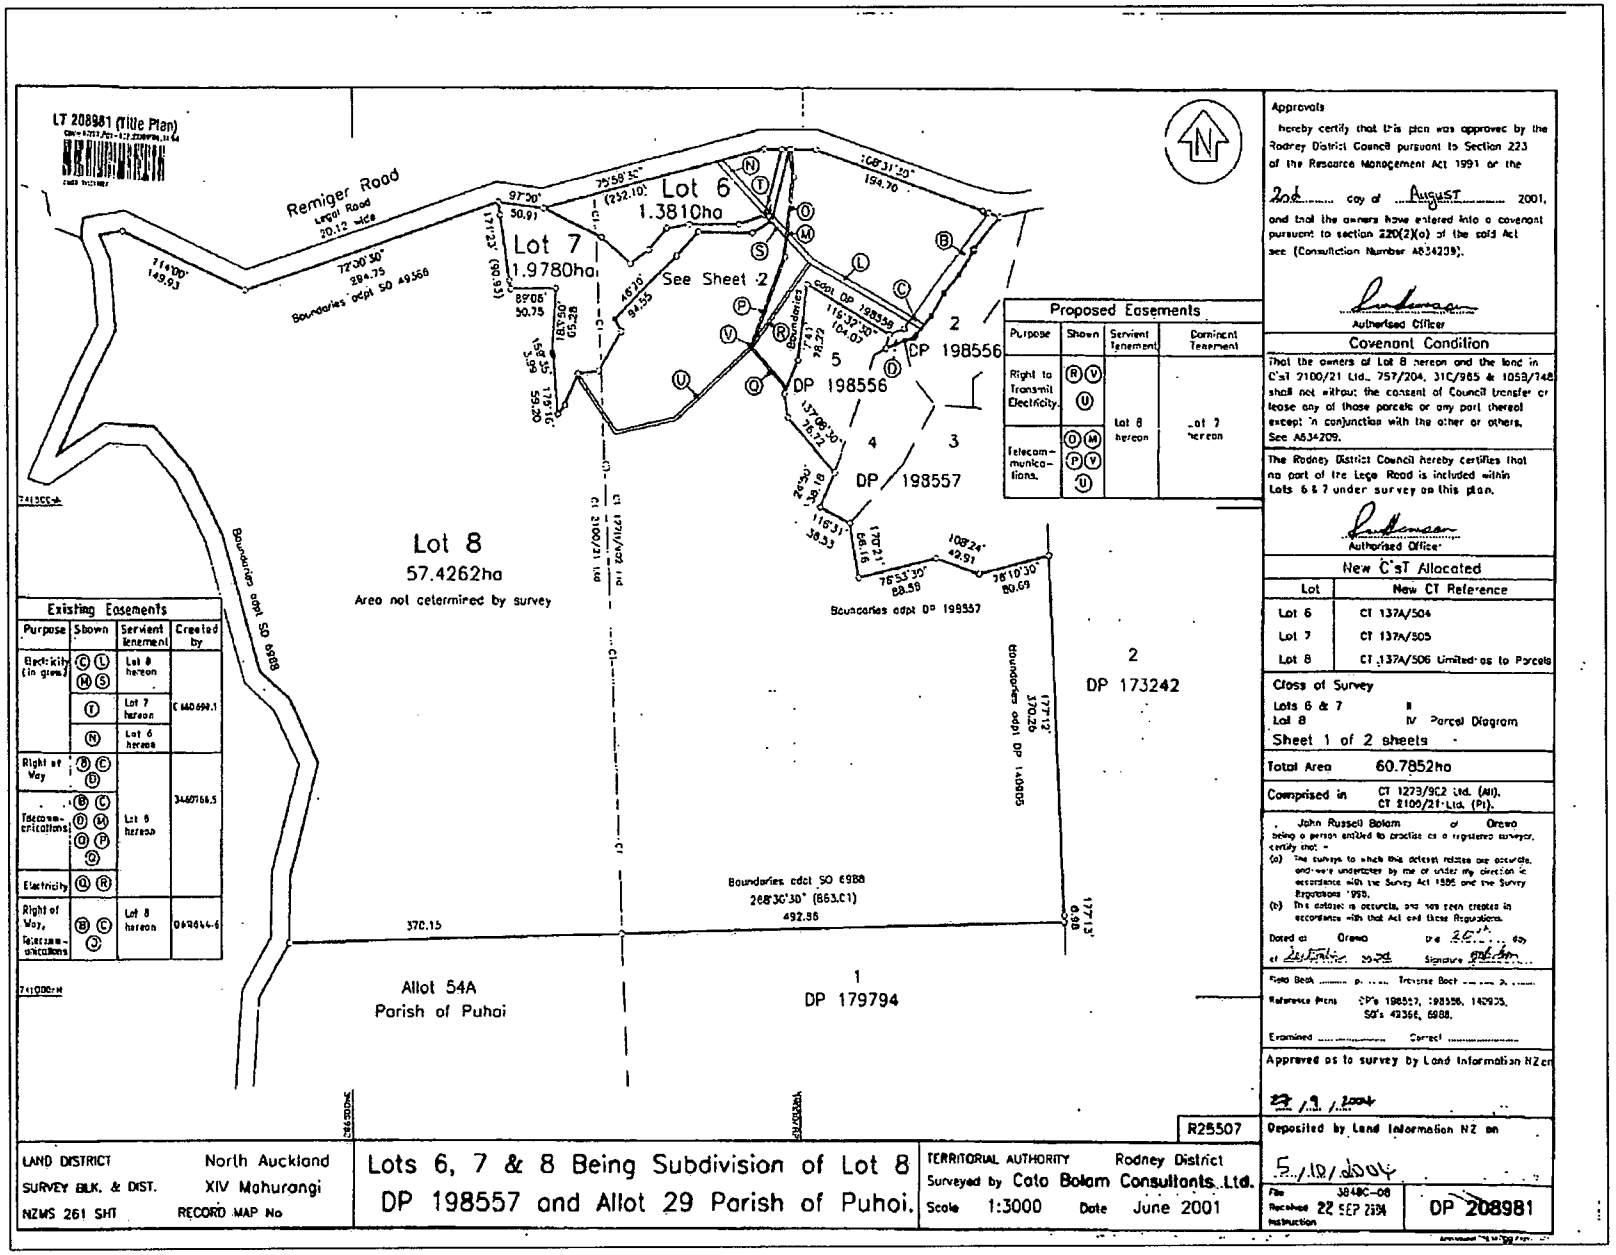
6170820.4 Covenant pursuant to Section 108(2)(d) Resource Management Act 1991 - 5.10.2004 at 9:00 am (Also affects CsT NA2100/21, NA31C/965, NA105B/748 and NA757/204)

Subject to a right to transmit an electricity easement over parts marked R, U and V on DP 208981 and a right to transmit telecommunications over parts marked O, M, P, U and V on DP 208981 created by Easement Instrument 6170820.9 - 5.10.2004 at 9:00 am

Appurtenant hereto are right to convey water & electricity easements created by Easement Instrument 8505466.1 - 28.5.2010 at 1:07 pm

9236051.3 Surrender of the electricity right parts marked L, M and S on DP 208981 created by Transfer C640690.1 - 16.11.2012 at 12:04 pm

Subject to a right (in gross) to convey electricity over parts marked D, E and F on DP 451839 in favour of Vector Limited created by Easement Instrument 9236051.4 - 16.11.2012 at 12:04 pm



Approvals

I hereby certify that this plan was approved by the Rodney District Council pursuant to Section 223 of the Resource Management Act 1991 on the 2nd day of August 2001, and that the owners have entered into a covenant pursuant to section 220(2)(a) of the said Act see (Consultation Number A634209).

Authorised Officer

Covenant Condition

That the owners of Lot 8 hereon and the land in C/sT 2100/21 Ltd., 757/204, 31C/985 & 1059/148 shall not without the consent of Council transfer or lease any of those parcels or any part thereof except in conjunction with the other or others. See A634209.

The Rodney District Council hereby certifies that no part of the Legal Road is included within Lots 6 & 7 under survey on this plan.

Authorised Officer

New C/sT Allocated

Lot	New CT Reference
Lot 6	CT 137A/504
Lot 7	CT 137A/505
Lot 8	CT 137A/506 Limited as to Parcels

Cross of Survey

Lots 6 & 7 II
Lot 8 IV Parcel Diagram

Sheet 1 of 2 sheets

Total Area 60.7852ha

Comprised in CT 1273/9C2 Ltd. (All).
CT 2100/21 Ltd. (Pt).

I, John Russell Bolam of Orewa being a person entitled to practise as a registered surveyor, certify that:-

(a) The survey to which this deposit relates was accurate, and was undertaken by me or under my direction in accordance with the Survey Act 1986 and the Survey Regulations 1990.

(b) This dataset is accurate, and was taken created in accordance with that Act and those Regulations.

Dated at Orewa this 20th day of September 2001

Signature

Field Book ... p. ... Traverse Book ... p. ...

Reference Plans SP's 198557, 198556, 142905, SO's 49366, 6988.

Examined ... Correct ...

Approved as to survey by Land Information NZ on

23/9/2004

Deposited by Land Information NZ on

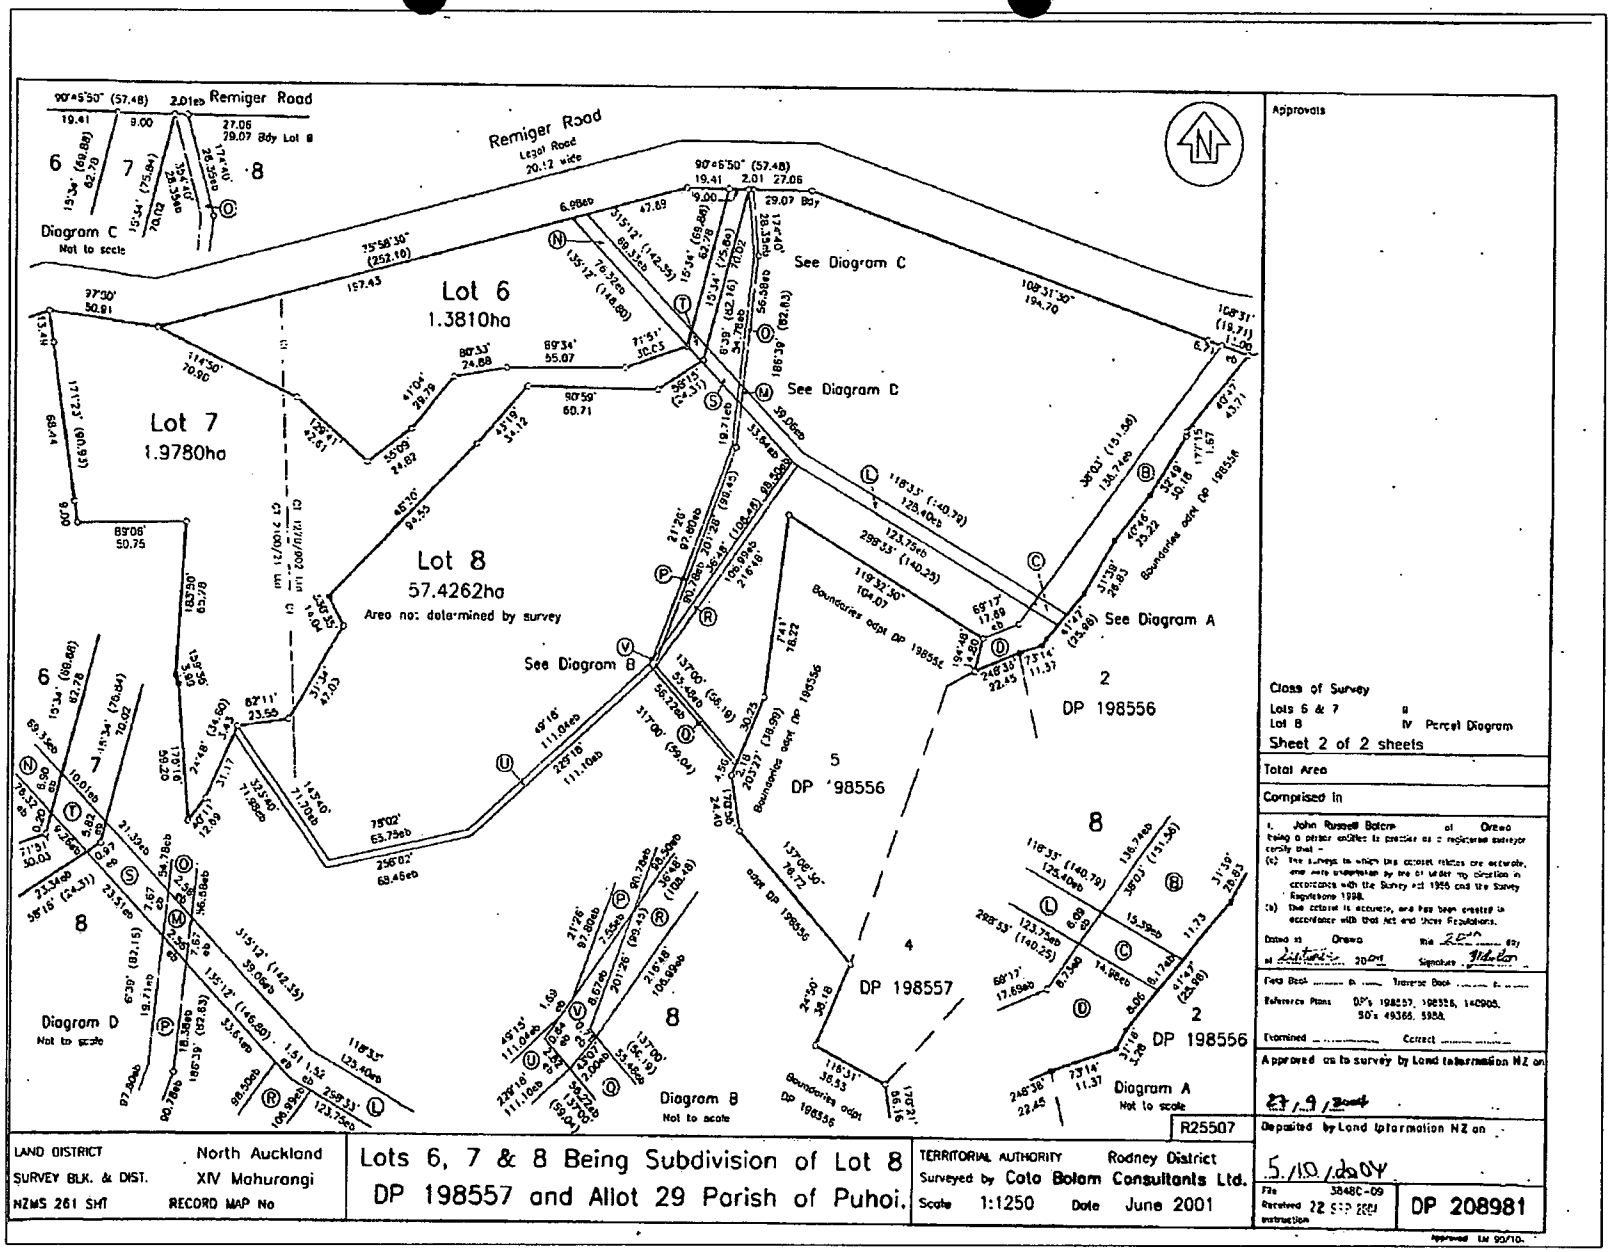
5/10/2004

File 3840C-08
Received 22 SEP 2004
Instruction

DP 208981

LAND DISTRICT	North Auckland	Lots 6, 7 & 8 Being Subdivision of Lot 8 DP 198557 and Allot 29 Parish of Puhoi.	TERRITORIAL AUTHORITY Rodney District
SURVEY BLK. & DIST.	XIV Mahurangi		Surveyed by Cato Bolam Consultants Ltd.
NZMS 261 SHT	RECORD MAP No		Scale 1:3000 Date June 2001

Transaction Id
Client Reference 40320
Search Copy Dated 1/02/18 4:05 pm, Page 2 of 3
Register Only


Remiger Road
Legal Road
20.12 wide
Lot 6
1.3810ha
Lot 7
1.9780ha
Lot 8
57.4262ha
Area no: determined by survey
See Diagram C
See Diagram D
See Diagram B
See Diagram A
DP 198556
DP 198557
Diagram C
Not to scale
Diagram D
Not to scale
Diagram B
Not to scale
Diagram A
Not to scale
Approvals
Class of Survey
Lots 6 & 7
Lot 8
III Parcel Diagram
Sheet 2 of 2 sheets
Total Area
Comprised in
LAND DISTRICT North Auckland
SURVEY BLK. & DIST. XIV Mahurangi
NZMS 261 SHT RECORD MAP No
Lots 6, 7 & 8 Being Subdivision of Lot 8
DP 198557 and Allot 29 Parish of Puhoi.
TERRITORIAL AUTHORITY Rodney District
Surveyed by Coto Bolam Consultants Ltd.
Scale 1:1250 Date June 2001
R25507
Deposited by Land Information NZ on
5/10/2004
DP 208981

COMPUTER FREEHOLD REGISTER
UNDER LAND TRANSFER ACT 1952

Search Copy

R.W. Muir
Registrar-General
of Land

Identifier	**NA105B/748**
Land Registration District	**North Auckland**
Date Issued	19 December 1996

Prior References
NA31C/964

Estate	Fee Simple
Area	24.1140 hectares more or less
Legal Description	Lot 1 Deposited Plan 179794

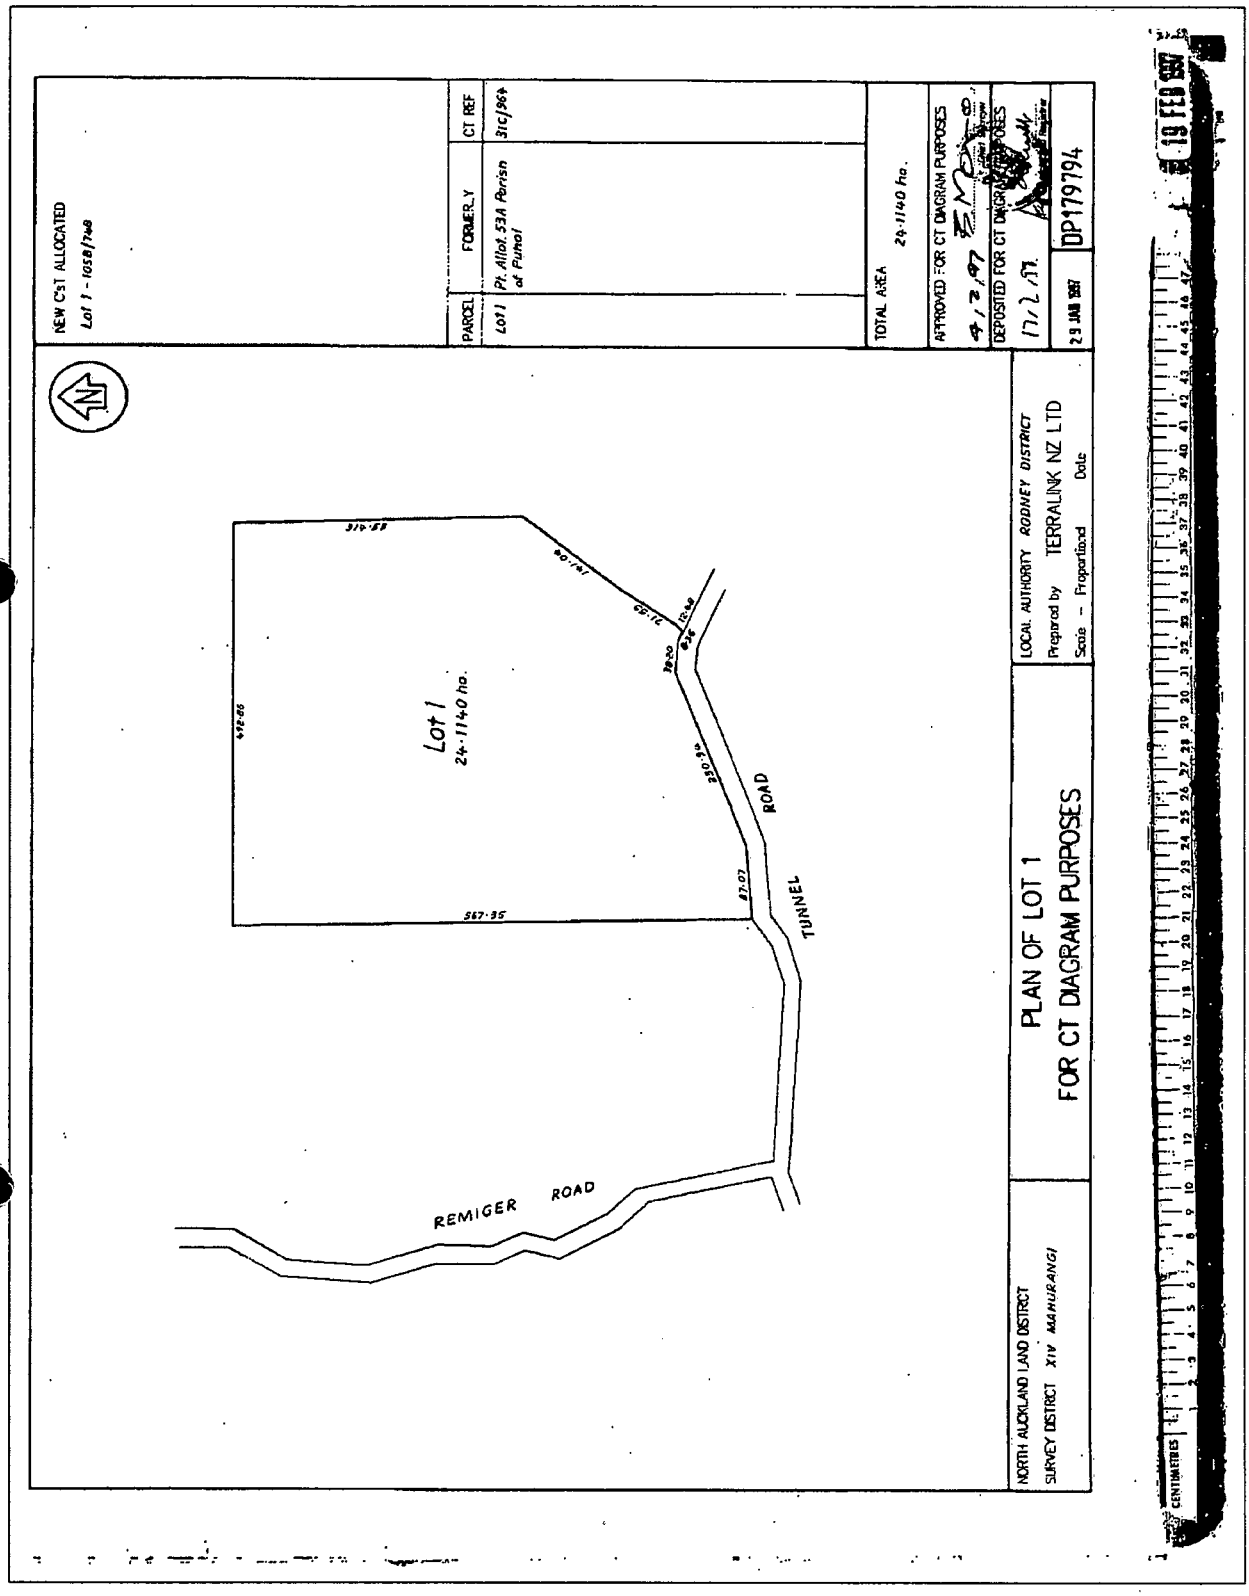
Proprietors
Raymond Charles Nicklin and Desma Elizabeth Nicklin

Interests

Subject to Section 59 Land Act 1948

C269124.5 Mortgage to Bank of New Zealand - 28.5.1991 at 9.40 am

6170820.4 Covenant pursuant to Section 108(2)(d) Resource Management Act 1991 - 5.10.2004 at 9:00 am (Also affects CsT NA137A/506, NA2100/21, NA31C/965 and NA757/204)


NEW C'ST ALLOCATED
Lot 1 - 1058/748
PARCEL
FORMERLY
CT REF
LOT 1
Pt Allot. 53A Parish of Puhoi
31C/964
TOTAL AREA 24·1140 ha.
APPROVED FOR CT DIAGRAM PURPOSES
DEPOSITED FOR CT DIAGRAM PURPOSES
17/2/97
29 JAN 1997
DP 179794
Lot 1
24·1140 ha.
314·58
90·74
62·76
12·48
38·20
8·36
230·34
47·07
567·35
412·66
ROAD
TUNNEL
REMIGER ROAD
PLAN OF LOT 1
FOR CT DIAGRAM PURPOSES
LOCAL AUTHORITY RODNEY DISTRICT
Prepared by TERRALINK NZ LTD
Scale - Proportional Date
NORTH AUCKLAND LAND DISTRICT
SURVEY DISTRICT XIV MAHURANGI
19 FEB 1997
CENTIMETRES

COMPUTER FREEHOLD REGISTER
UNDER LAND TRANSFER ACT 1952

Search Copy

R.W. Muir
Registrar-General
of Land

Identifier	**NA31C/965**
Land Registration District	**North Auckland**
Date Issued	02 September 1975

Prior References
NA1111/288

Estate	Fee Simple
Area	21.6507 hectares more or less
Legal Description	Allotment 54A Parish of Puhoi

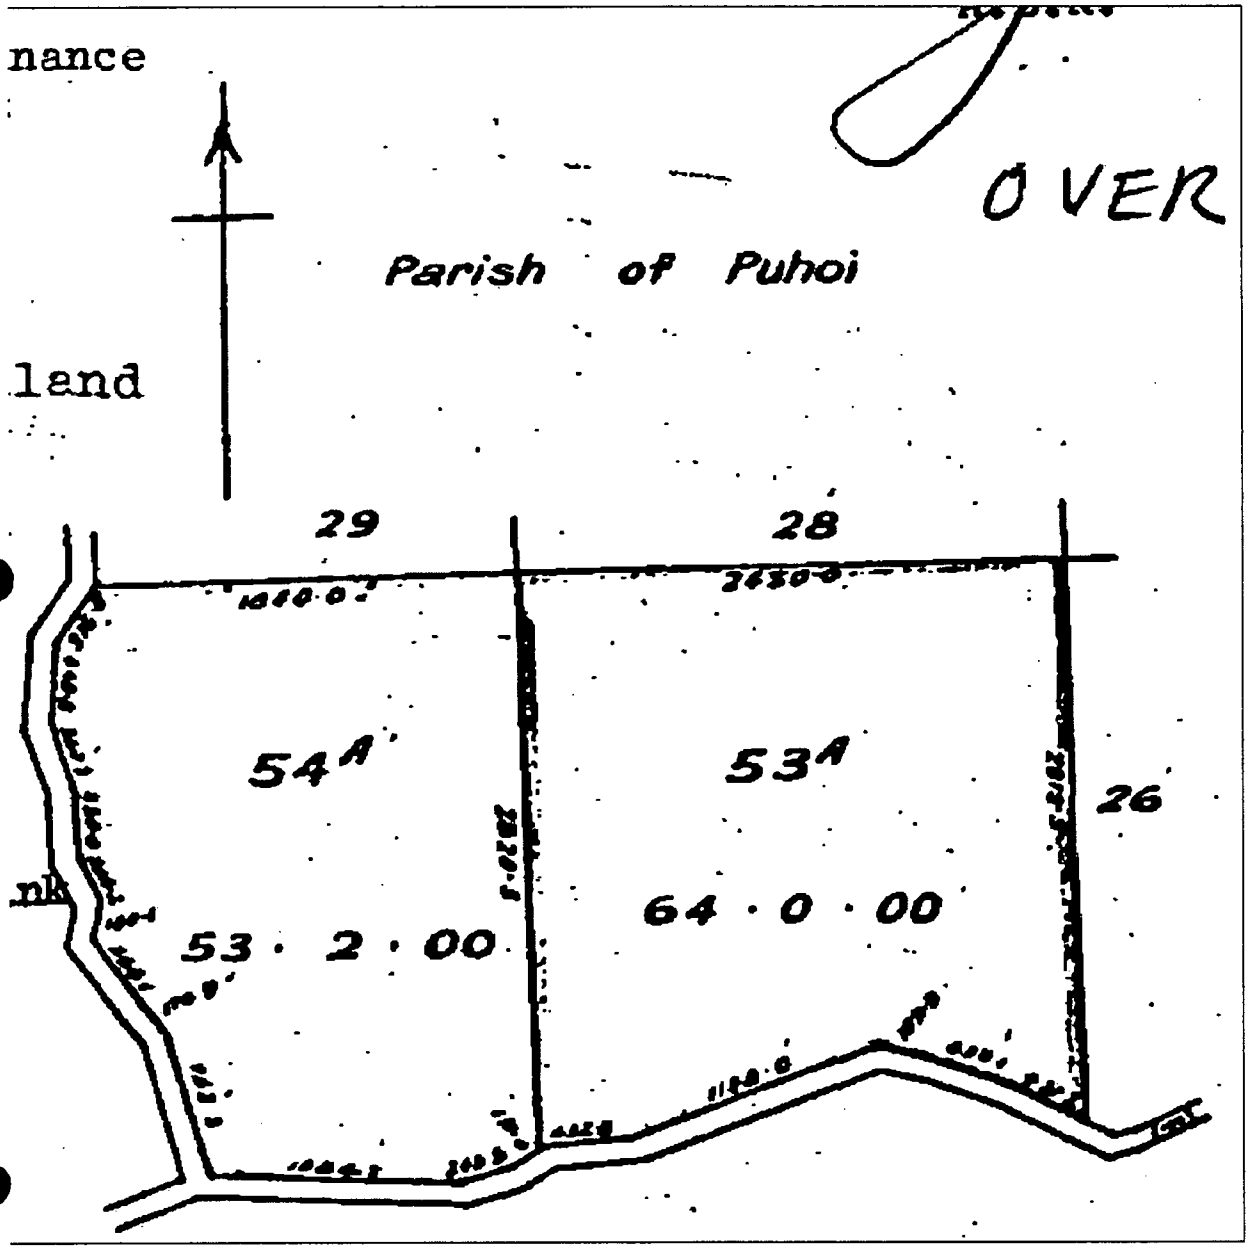
Proprietors
Raymond Charles Nicklin as to a 1/2 share
Desma Elizabeth Nicklin as to a 1/2 share

Interests

Subject to Section 59 Land Act 1948

C269124.5 Mortgage to Bank of New Zealand - 28.5.1991 at 9.40 am

6170820.4 Covenant pursuant to Section 108(2)(d) Resource Management Act 1991 - 5.10.2004 at 9:00 am (Also affects CsT NA137A/506, NA2100/21, NA105B/748 and NA757/204)


nance
OVER
Parish of Puhoi
land
29
28
54A
53A
26
53 · 2 · 00
64 · 0 · 00

COMPUTER FREEHOLD REGISTER
UNDER LAND TRANSFER ACT 1952
Limited as to Parcels

Search Copy

R.W. Muir
Registrar-General
of Land

Identifier	**NA757/204**
Land Registration District	**North Auckland**
Date Issued	21 September 1939

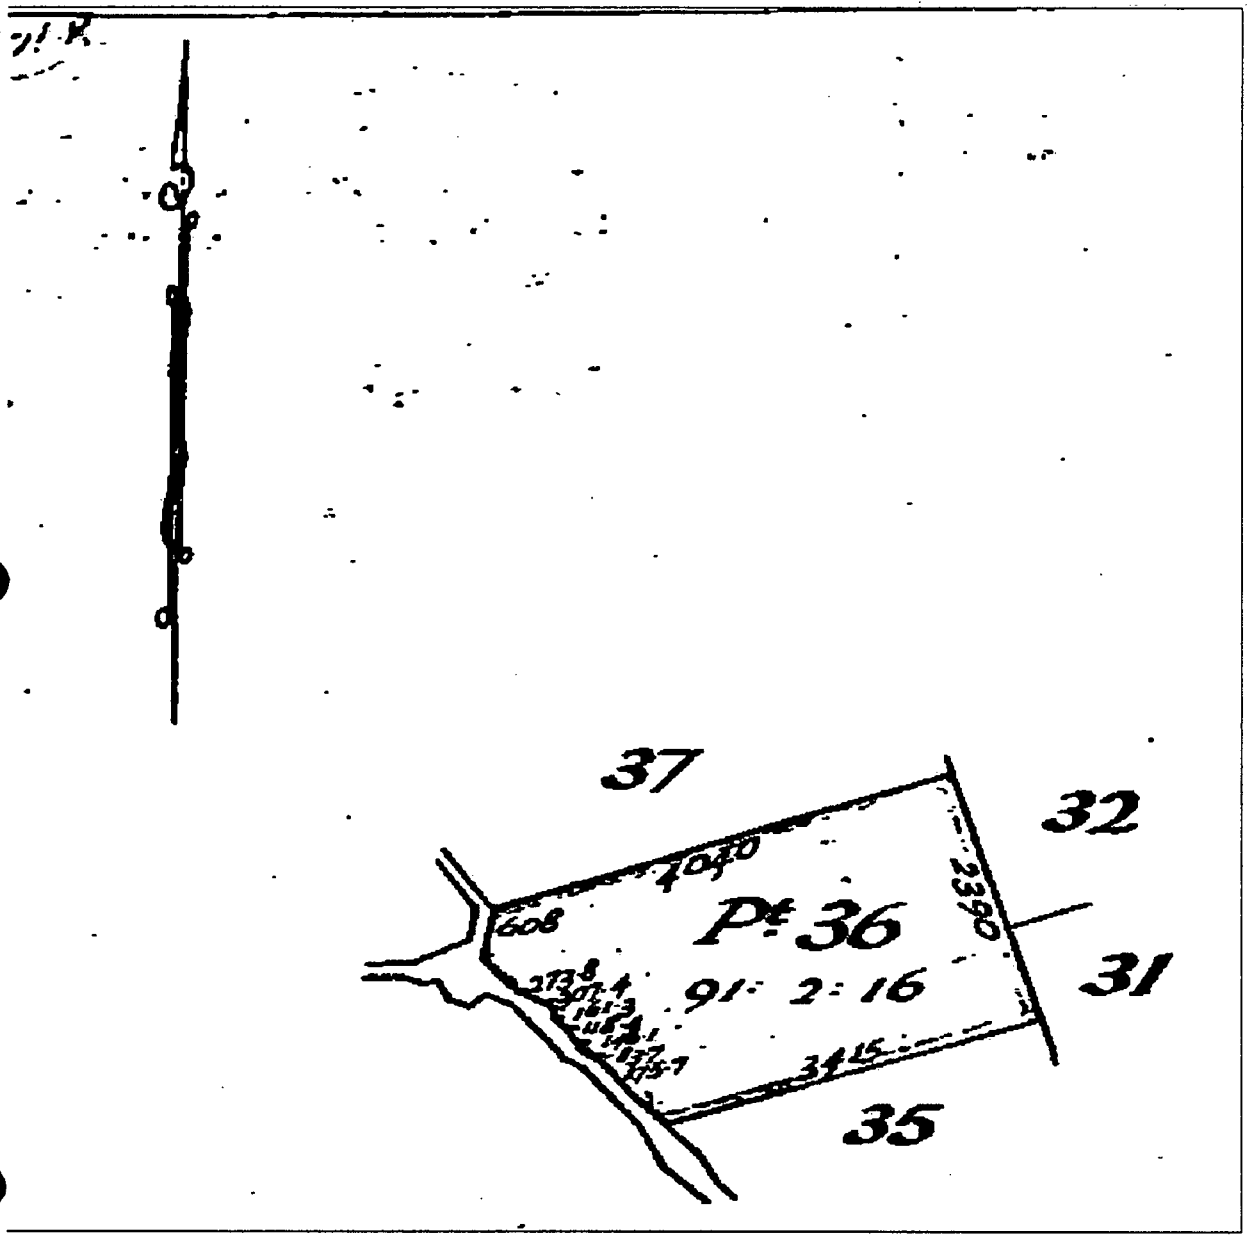
Prior References
DI 8B.692

Estate	Fee Simple
Area	37.0692 hectares more or less
Legal Description	Part Allotment 36 Parish of Puhoi

Proprietors
Raymond Charles Nicklin as to a 1/2 share
Desma Elizabeth Nicklin as to a 1/2 share

Interests
797043A.2 Mortgage to Bank of New Zealand - 14.8.1981 at 9.47 am

6170820.4 Covenant pursuant to Section 108(2)(d) Resource Management Act 1991 - 5.10.2004 at 9:00 am (Also affects CsT NA137A/506, NA2100/21, NA31C/965 and NA105B/748)


37
32
1040
2390
608
Pt 36
91- 2- 16
31
35

COMPUTER FREEHOLD REGISTER
UNDER LAND TRANSFER ACT 1952
Limited as to Parcels

Search Copy

R.W. Muir
Registrar-General
of Land

Part-Cancelled

Identifier	**NA2100/21**
Land Registration District	**North Auckland**
Date Issued	05 November 1962

Prior References
NA757/202

Estate	Fee Simple
Area	229.2180 hectares more or less
Legal Description	Allotment 29, 32, 35 Parish of Puhoi and Part Allotment 28, 30-31 Parish of Puhoi

Proprietors
Raymond Charles Nicklin as to a 1/2 share
Desma Elizabeth Nicklin as to a 1/2 share

Interests

C269124.5 Mortgage to Bank of New Zealand - 28.5.1991 at 9.40 am

Subject to an electricity right (in gross) over part marked B on DP 159737 in favour of (now) Vector Limited created by Transfer C640690.1 - 15.8.1994 at 9.17 am

D460766.3 CTs NA127B/896, NA127B/898-899 issued for part Lots 1, 5, and 8 DP 198556 -produced 9.12.1999 at 12:34 pm and entered 1.2.2000 at 9:00 am

6170820.1 Certificate pursuant to Section 223 Resource Management Act 1991(affects DP 208981) - 5.10.2004 at 9:00 am

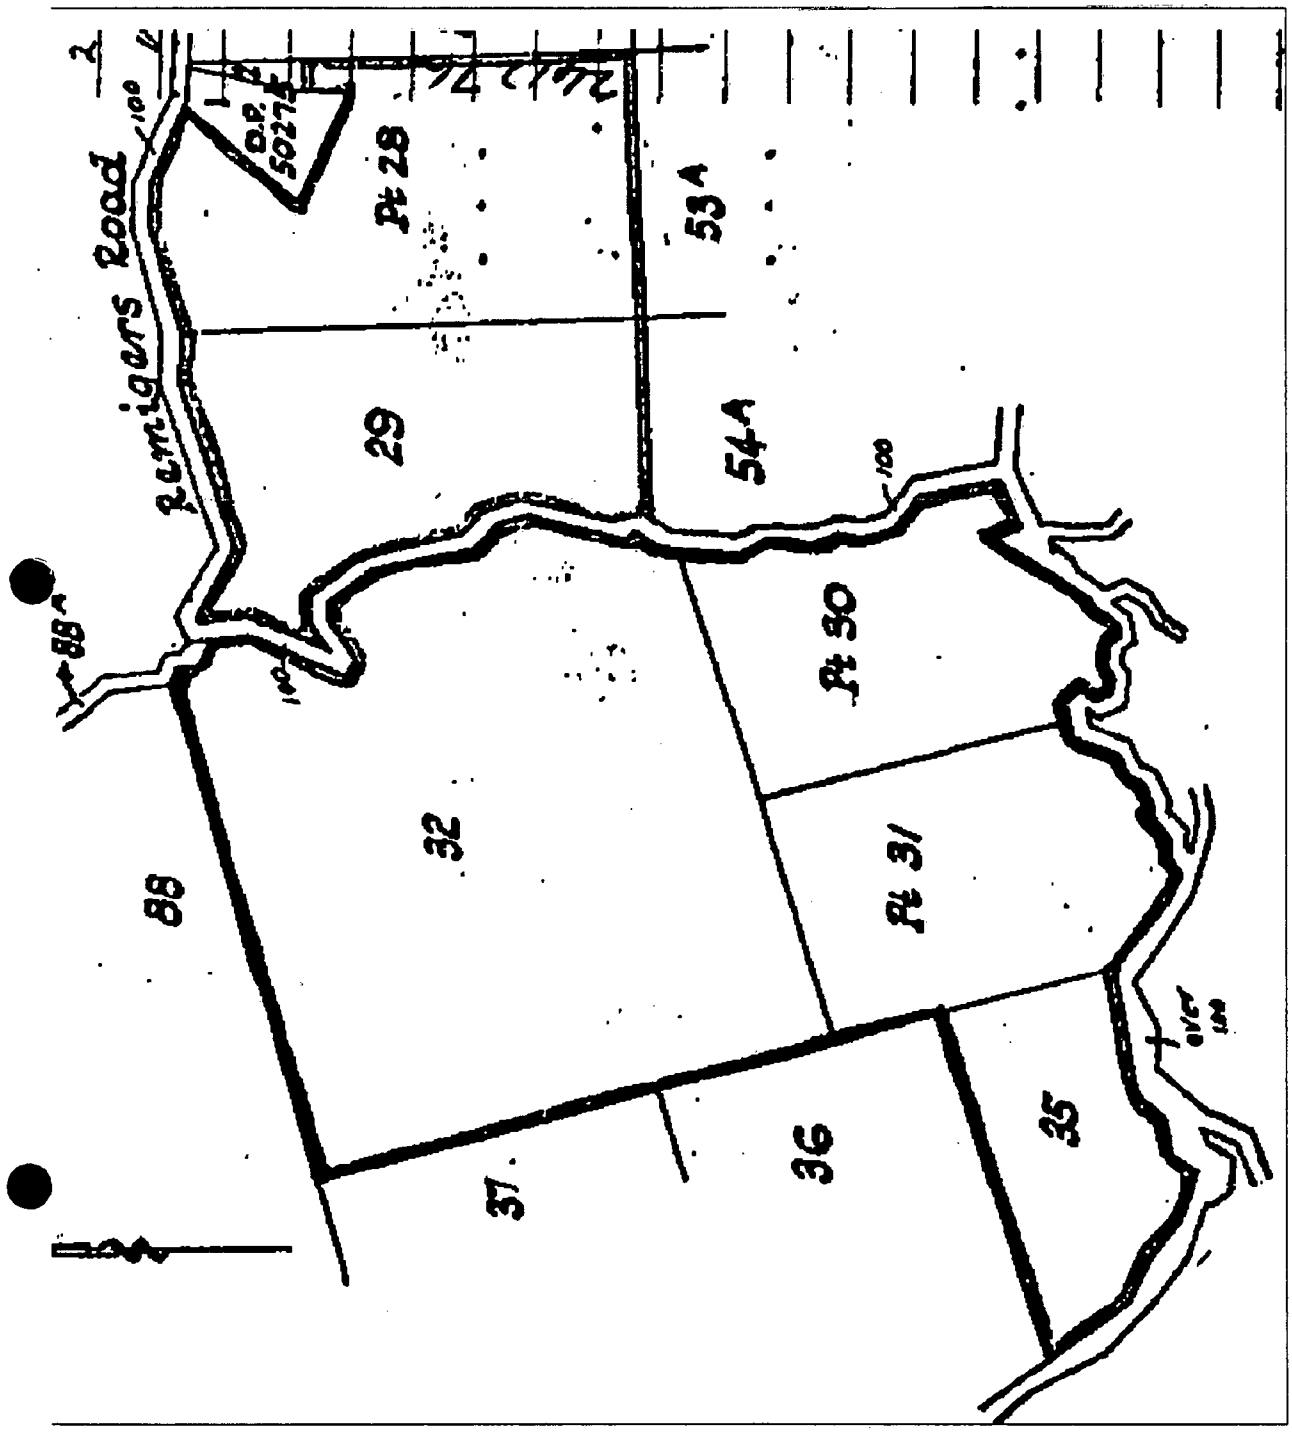
6170820.2 Certificate pursuant to Section 224(c) Resource Management Act 1991 (affects DP 208981 - 5.10.2004 at 9:00 am

6170820.3 Consent Notice pursuant to Section 221 Resource Management Act 1991 - 5.10.2004 at 9:00 am (affects Lot 6 DP 208981)

6170820.4 Covenant pursuant to Section 108(2)(d) Resource Management Act 1991 - 5.10.2004 at 9:00 am (Also affects CsT NA137A/506, NA31C/965, NA105B/748 and NA757/204)

6170820.8 CTs issued - 5.10.2004 at 9:00 am

Legal Description	**Title**
Lot 6 Deposited Plan 208981	NA137A/504
Lot 7 Deposited Plan 208981	NA137A/505
Lot 8 Deposited Plan 208981	NA137A/506


Lemiggers Road
100
D.P. 50274
Pt 28
53A
29
54A
100
Pt 30
88A
140
32
Pt 31
88
35
36
37

CONO 6170820.3 Cons
Cpy-01/01,Pgs-001,04/10/04,16:37
DocID: 311626489

IN THE MATTER of a Plan lodged for Deposit under Number 208981

Pursuant to Section 221 of the Resource Management Act 1991 THE RODNEY DISTRICT COUNCIL HEREBY GIVES NOTICE that its subdivision consent given in respect of the land in the Second Schedule as shown on Land Transfer Plan 208981 is conditional inter alia upon the compliance on a continuing basis by the Subdivider and the subsequent owners of the land in the Third Schedule hereto with the conditions set forth in the First Schedule hereto.

FIRST SCHEDULE

(building restrictions) Any buildings erected on Lot 6 shall be subject to a minimum habitable floor level not lower than 0.6 metres above the top of the strainer post at the northern corner of Lot 6 or 2.5 metres above the existing bridge deck off the end of Remiger Road, as per the recommendations of the report from Hutchinson Consultants Ltd, dated 30 April 1999.

SECOND SCHEDULE

An estate in fee simple in 60.7852 hectares more or less being Lot 8 DP 198557 and Allot 29 Parish of Puhoi comprised in Certificates of Title 127B/902 Ltd (All) and 2100/21 Ltd (Pt) North Auckland Land Registry.

THIRD SCHEDULE

Lot 6 DP 208981 totalling 1.3810 hectares in area.

DATED this 15th day of July 2004.

SIGNED for and on behalf of)
the RODNEY DISTRICT COUNCIL)

Authorised Officer

SCHEME PLAN: R 25507

COMPUTER FREEHOLD REGISTER
UNDER LAND TRANSFER ACT 1952

Search Copy

R.W. Muir
Registrar-General
of Land

Identifier	**NA127B/898**
Land Registration District	**North Auckland**
Date Issued	01 February 2000

Prior References
NA2036/1 NA2100/21

Estate	Fee Simple
Area	1.1705 hectares more or less
Legal Description	Lot 5 Deposited Plan 198556

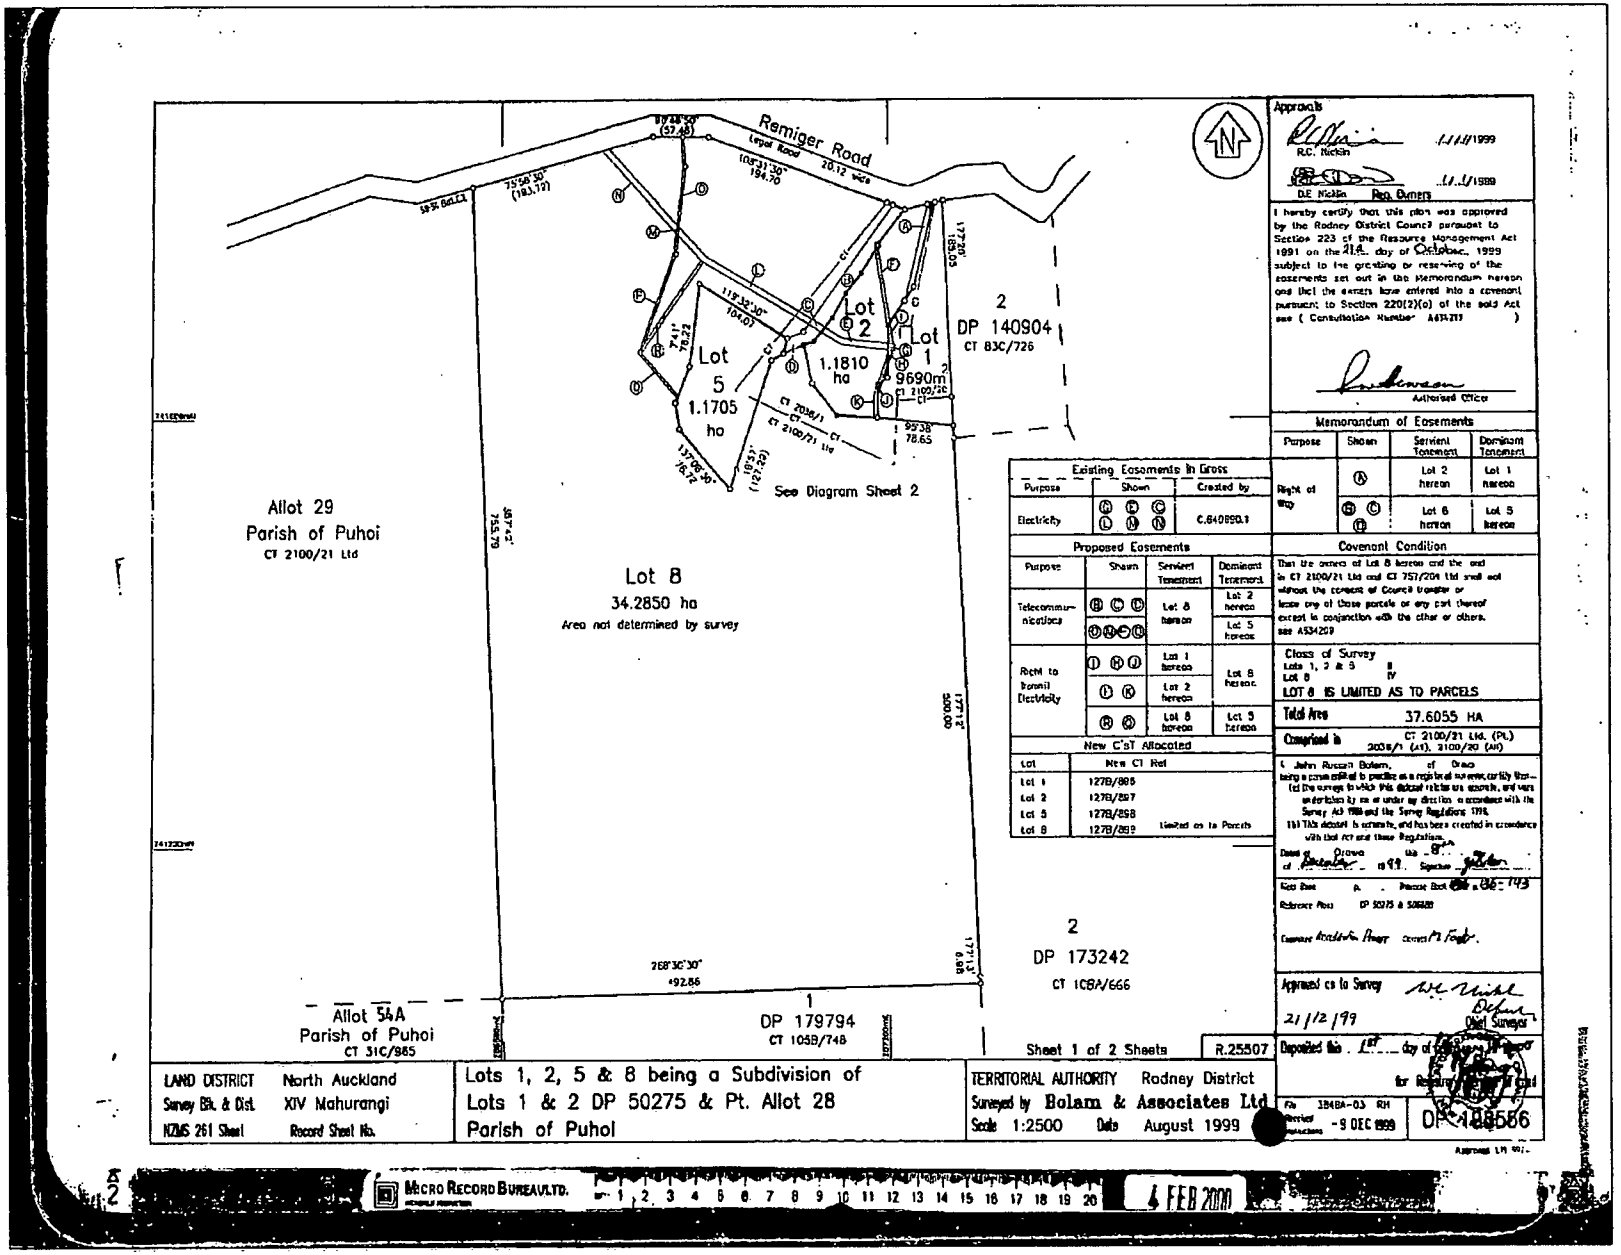
Proprietors
Christopher Charles Nicklin and Kathryn Ann Nicklin

Interests

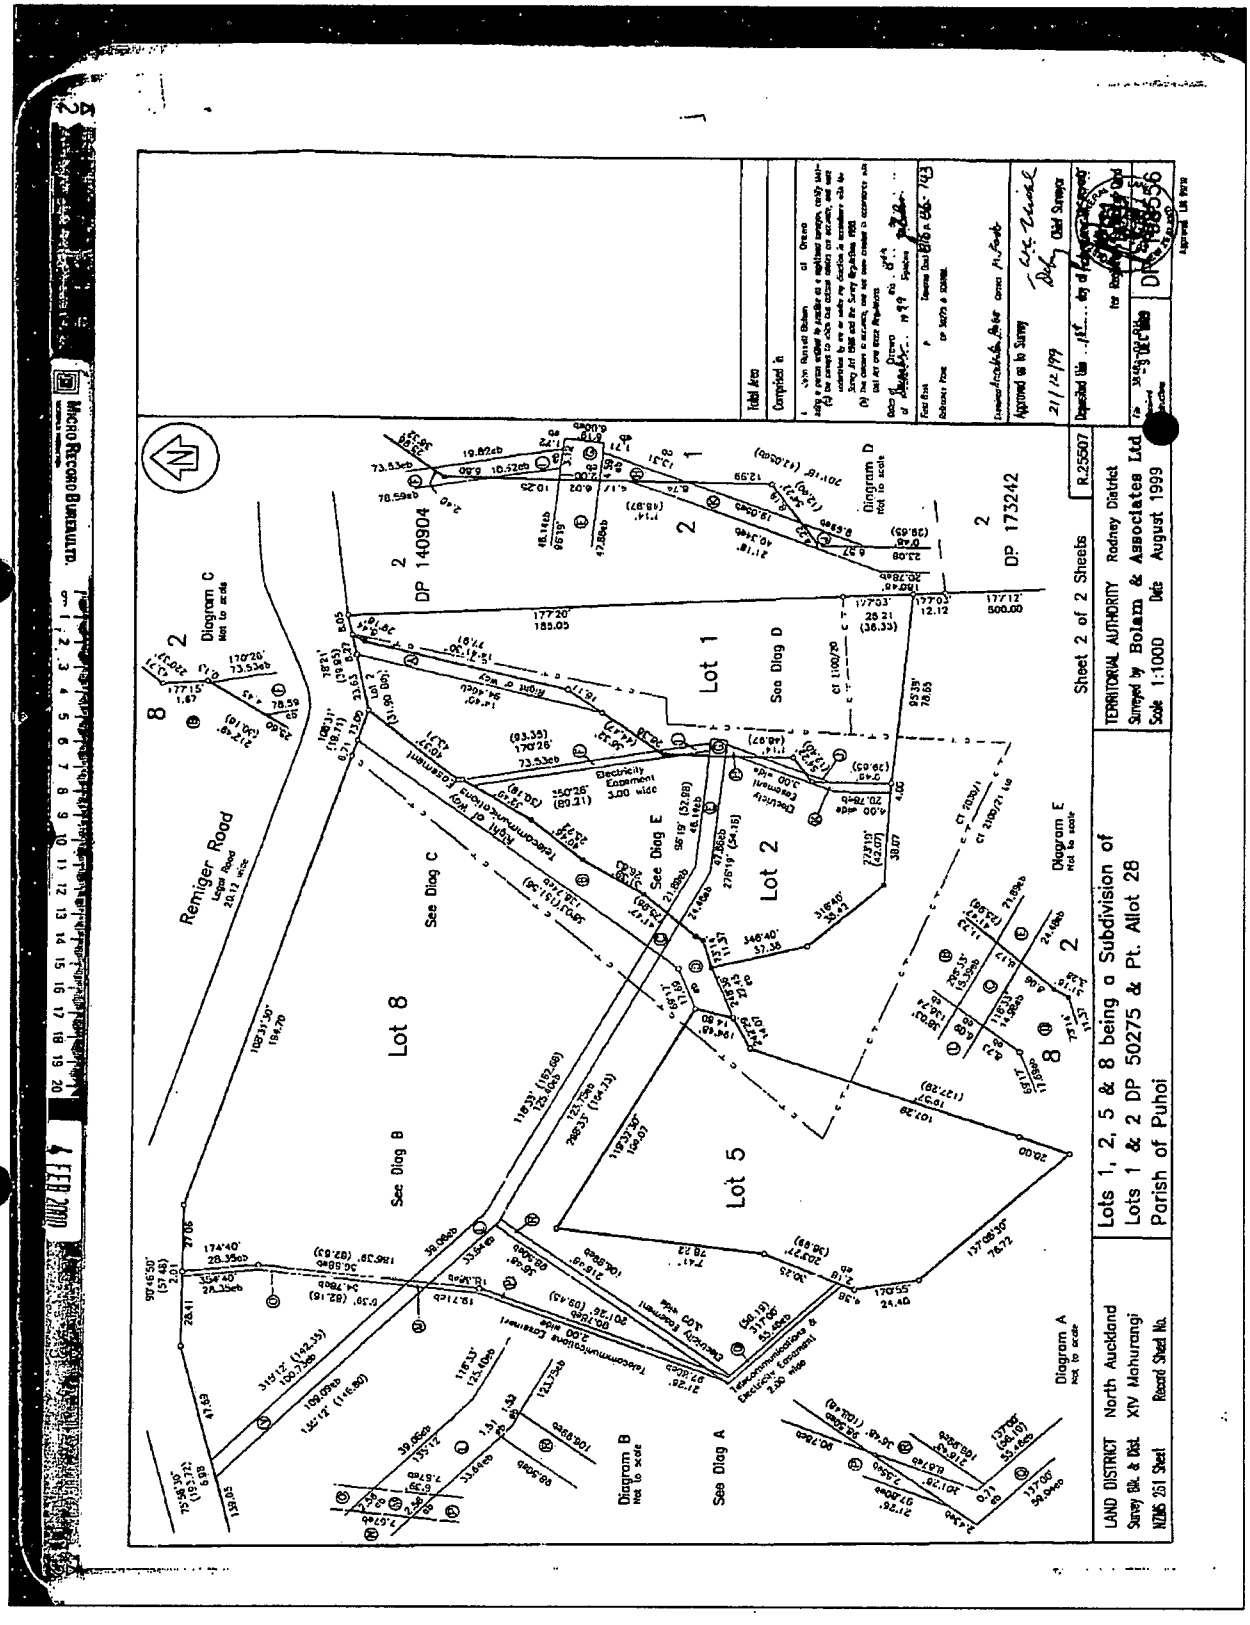
Appurtenant hereto is a right of way and telecommunications and electricity rights specified in Easement Certificate D460766.5 - produced 9.12.1999 at 12.34 pm and entered 1.2.2000 at 9.00 am

Some of the easements specified in Easement Certificate D460766.5 are subject to Section 243 (a) Resource Management Act 1991 (see DP 198556)

6231198.4 Mortgage to Bank of New Zealand - 29.11.2004 at 9:00 am



Transaction Id 40320
Client Reference
Search Copy Dated 1/02/18 4:06 pm, Page 2 of 3
Register Only


Lots 1, 2, 5 & 8 being a Subdivision of
Lots 1 & 2 DP 50275 & Pt. Allot 28
Parish of Puhoi
LAND DISTRICT North Auckland
Survey Bk. & Dist. XIV Mahurangi
NZMS 251 Sheet Record Sheet No.
TERRITORIAL AUTHORITY Rodney District
Surveyed by Bolam & Associates Ltd
Scale 1:1000 Date August 1999
Sheet 2 of 2 Sheets
R.25507
DP 173242
DP 140904
Lot 1
Lot 2
Lot 5
Lot 8
Remiger Road
Diagram A
Diagram B
Diagram C
Diagram D
Diagram E
Electricity Easement 3.00 wide
Telecommunications & Electricity Easement 3.00 wide
Right of Way
See Diag A
See Diag B
See Diag C
See Diag D
See Diag E