From: Myles Goodwin
To: Hannah Thomson
Subject: RE: [#CBC 40320] Remiger Road - Nicklin
Date: Thursday, 12 October 2023 1:28:35 pm
Attachments: image001.png
image002.png
image003.png
image004.png
369303.png
LinkedIn2.png
5150136.png
Facebook2.png

Hi Hannah, yes, should be. Did not ask for any other alteration.

Regards
Myles

Cato Bolam
creating great places

Myles Goodwin
Director
09 427 0072 | 027 493 3022
catobolam.co.nz

WARNING This e-mail contains information which is CONFIDENTIAL and that may be subject to PRIVILEGE. If you are not the intended recipient, you must not peruse, use, disseminate, distribute or copy this email or attachments. If you have received this in error, please notify us immediately by return e-mail, facsimile or telephone and delete this e-mail. Thank you

---

From: Hannah Thomson <hannah@planningplus.co.nz>
Sent: Thursday, October 12, 2023 12:51 PM
To: Myles Goodwin <MylesG@catobolam.co.nz>
Subject: RE: [#CBC 40320] Remiger Road - Nicklin

Thanks Myles. Is everything else (apart from Lot 3 size and boundaries) the same as the last plan version?

Kind regards,

Hannah

Hannah Thomson

Principal Planner/ Director
p: 09 4279966 m: 0212619966
a: PO Box 310 174, Red Beach. Auckland 0945
w: www.planningplus.co.nz/ e: hannah@planningplus.co.nz

PLANNINGPLUS

PLANNING PLUS is a registered trade mark of PLANNING PLUS LIMITED
Disclaimer: This email message and any attachments contain information that may be confidential and may be LEGALLY PRIVILEGED. If you are not the intended recipient, any use, disclosure or copying of this message or attachments is strictly prohibited. If you have received this email message in error please notify us immediately and erase all copies of the message and attachments. We do not accept responsibility for any viruses or similar carried with our email, or any effects our email may have on the recipient computer system or network. Any views expressed in this email may be those of the individual sender and may not necessarily reflect the views of Planning Plus Ltd ®.

From: Myles Goodwin <MylesG@catobolam.co.nz>
Sent: Wednesday, October 11, 2023 3:42 PM

To: Hannah Thomson <hannah@planningplus.co.nz>
Subject: [#CBC 40320] Remiger Road - Nicklin

Hi Hannah, please see attached. Lot 3 is showing at 0.77ha and now includes the area of willows to north east. Ray would really like to keep the lot contained to this area is possible as this is the area where the house and associated wastewater disposal field has been granted. It is a smaller, self contained area separated from the main farm by a significant gully to the west, and the main farm access to the south. Therefore given the presence of the house, this area is never going to be part of the larger productive area of the farm. We could add in another bit to the south of the ROW to get the 1ha area, but then that area would no longer be grazed as part of the farm. While not good quality land due to it being steeper land, it is still productive when used as part of a significantly larger landholding. Therefore what is shown is what Ray Nicklin would ideally like to achieve.

Regards
Myles

Myles Goodwin
DirectorEnvironmental Planner | BSc | MSc(Hons)
09 427 0072 | **027 493 3022**
mylesg@catobolam.co.nz
19 Tamariki Avenue, Orewa
catobolam.co.nz

This drawing and design remains the property of, and may not be reproduced or amended without the written permission of Cato Bolam Consultants Ltd. No liability shall be accepted for unauthorised use of this drawing and design.

Auckland Council
Comprised in:

RT NA137A/506Ltd	57.4262ha
RT NA105B/748	24.1140ha
RT NA31C/965	21.6507ha
RT NA757/204Ltd	37.0692ha
RT NA2100/21Ltd	160.87ha
RT NA127B/898	1.1705ha
Total Area	302.3006ha

Areas and measurements are subject to survey.

- Riparian Margin Protection
- Significant Ecological Area
- Proposed Building Area
- Watercourse
- Extent of Flood Plain

Areas (CP)-(CV) (53.07ha) are to be subject to land covenants to protect native bush .

Areas (CO)(CX)-(CZ)(Z) (0.9ha) are to be subject to land covenants to protect riparian planting.

Cato Bolam
creating great places
PLANNERS | SURVEYORS | ENGINEERS
ARCHITECTS | ENVIRONMENTAL

R.C.& D.E. Nicklin
53B Remiger Road
Puhoi

Lots 1 - 8 being
Proposed Subdivision of
Lot 8 DP 208981, Lot 5 DP 198556
Lot 1 DP 179794, Allots 32,35,54A &
Pt Allots 30,31,36 Parish of Puhoi

FOR RESOURCE CONSENT

No.	REVISION (DESCRIPTIONS)	NAME	DATE
C	Lots 3 & 8 adjusted	MG	05/05/2023
D	Lots 3 & 6 adjusted Lots 9 & 10 added	MG	22/06/2023
E	Lot 8 adjusted, OLFPS deleted	MG	25/07/2023
F	Lot 3/6 bdy adjstd, Lots 9 & 10 deleted	MG	11/10/2023
SURVEYED			
DESIGNED			
DRAWN		LS	08/09/2017

DATE	ORIGINAL SCALE	ORIGINAL SIZE
11/10/2023	1:10,000	A3


DRAWING NO.	REVISION
40320-DR-PLN-1200	F

EXISTING EASEMENTS

PURPOSE	SHOWN	BURDENED LAND	CREATED BY
RIGHT OF WAY & TELECOMMUNICATIONS	B C D	LOT 6 HEREON	E.C. D460766.5 E.C. D611644.6
RIGHT TO CONVEY TELECOMMUNICATIONS	K N O W XA Y YA	LOT 6 HEREON	E.C. D460766.5 E.I. 6170820.9
	I L M	LOT 5 HEREON	
	P Q X	LOT 8 HEREON	
	YB	LOT 3 HEREON	
RIGHT TO CONVEY ELECTRICITY	YB	LOT 3 HEREON	
	O S U W XA Y YA	LOT 6 HEREON	
	P Q T V X	LOT 8 HEREON	

EXISTING EASEMENTS IN GROSS

PURPOSE	SHOWN	BURDENED LAND	CREATED BY
RIGHT TO CONVEY ELECTRICITY	C G R	LOT 6 HEREON	E.I. 9236051.4
	E	LOT 2 HEREON	
	F	LOT 1 HEREON	
	H I J Z	LOT 5 HEREON	

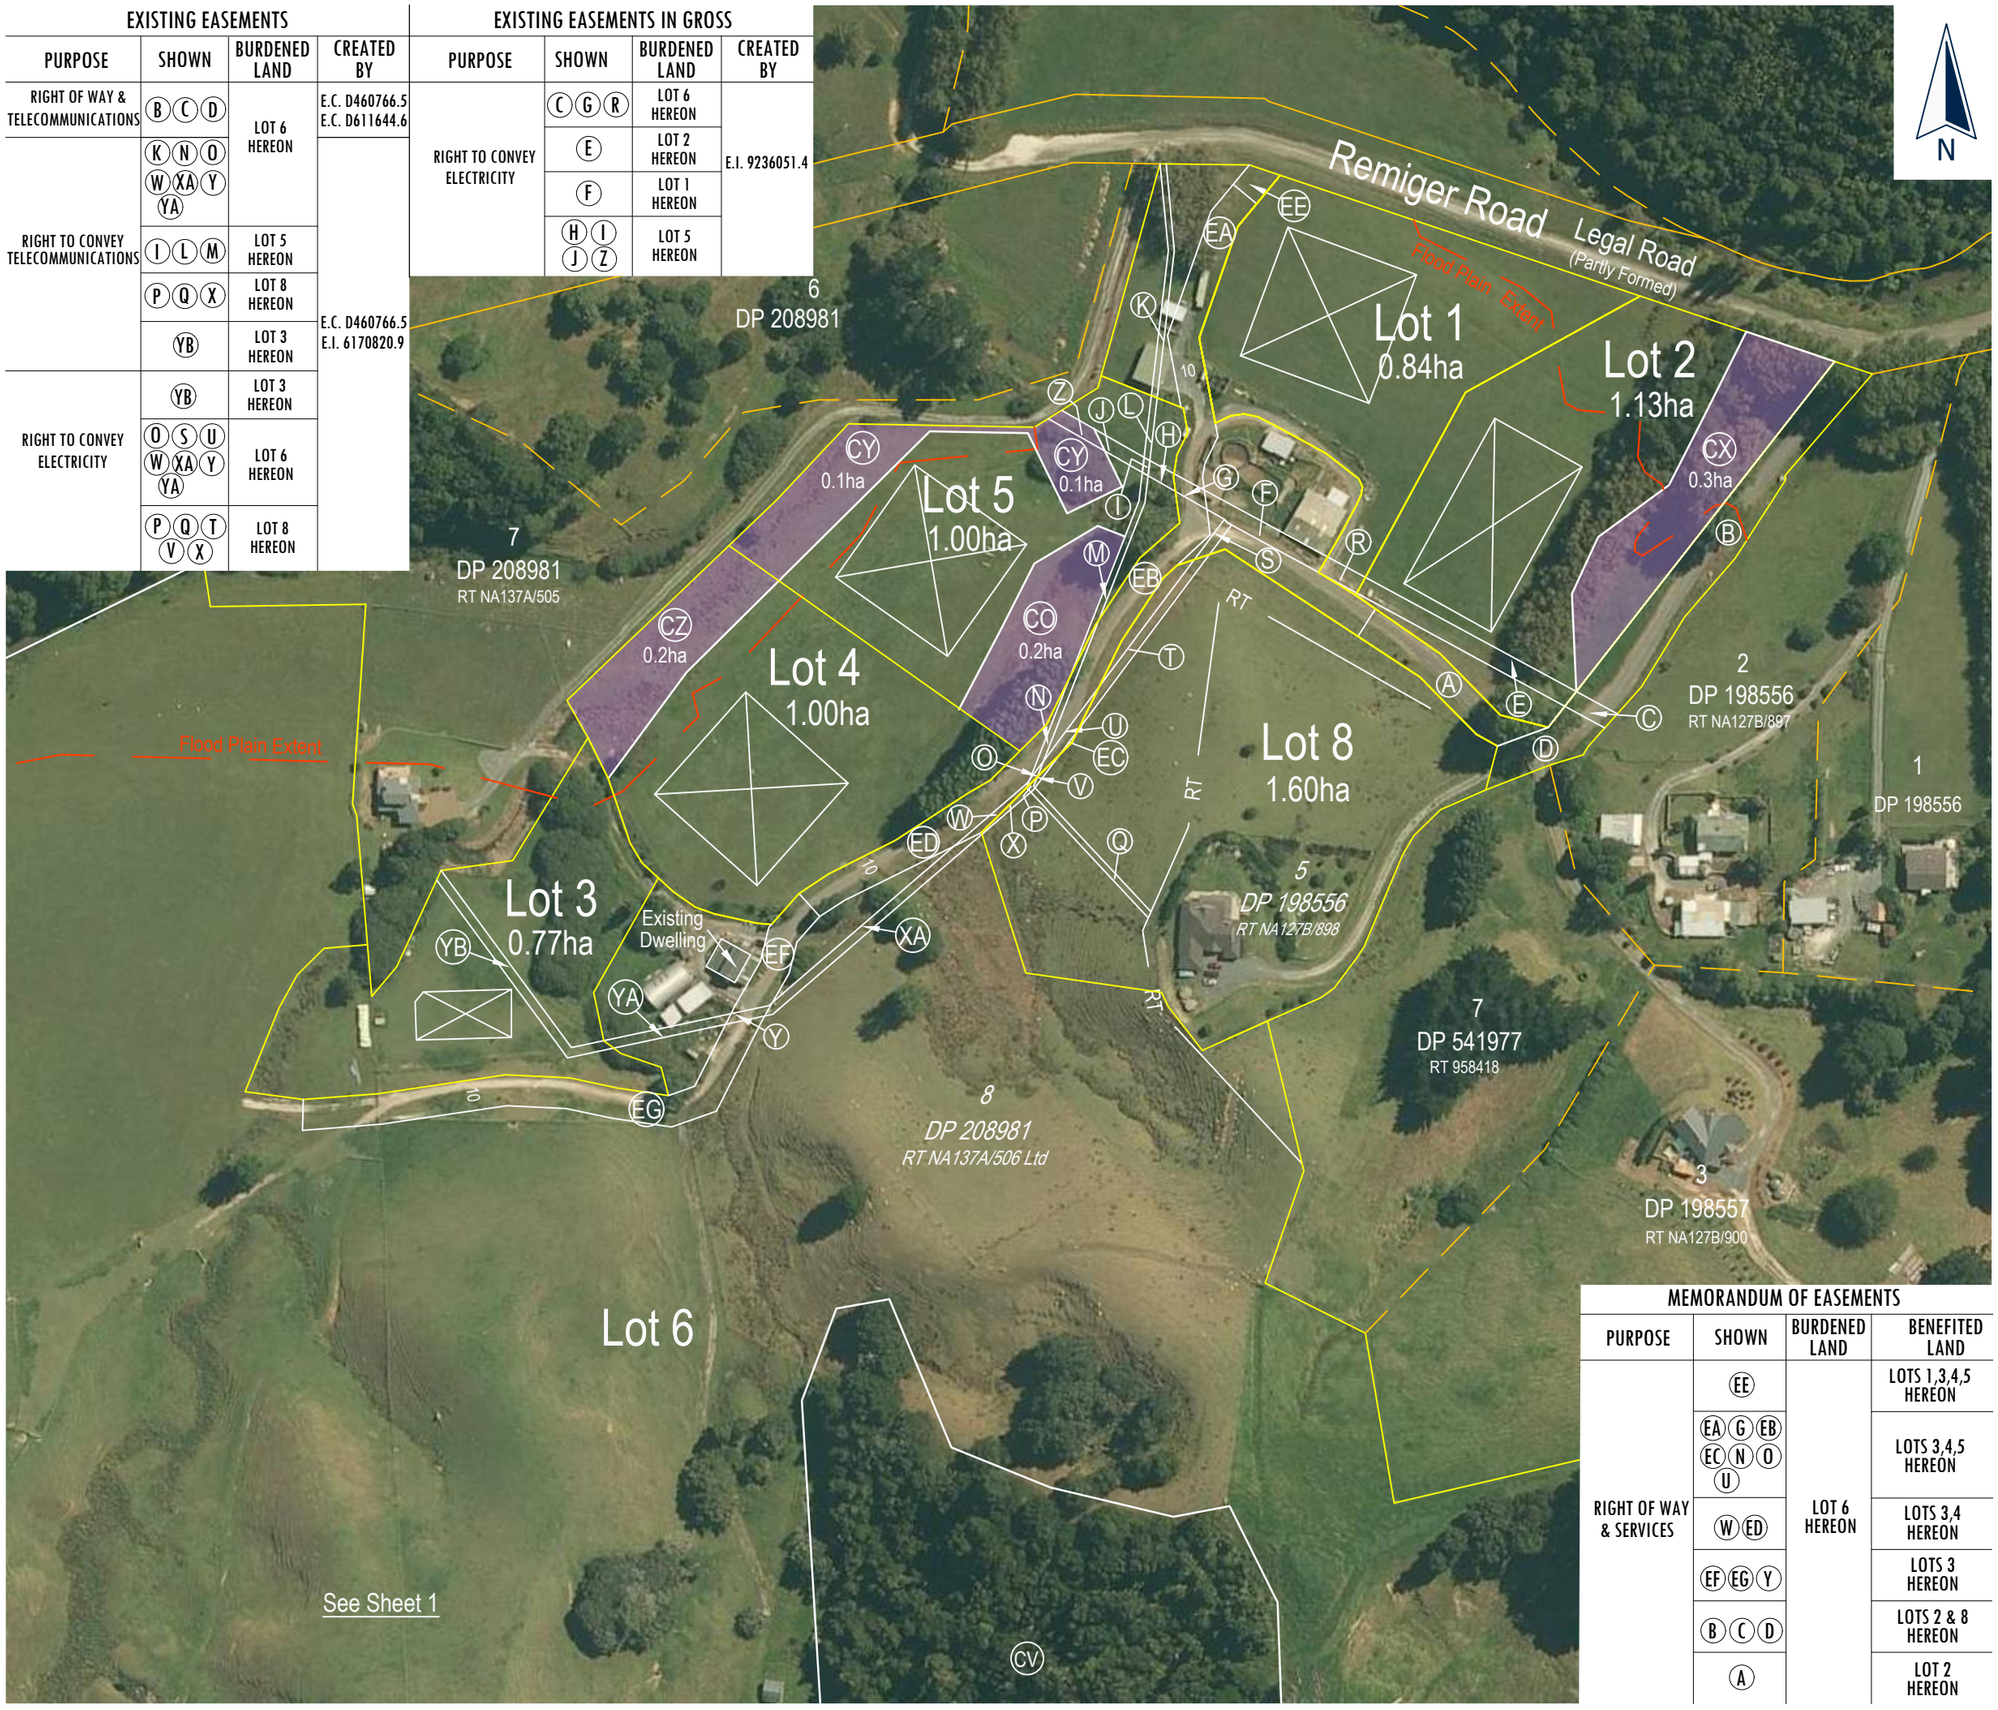

MEMORANDUM OF EASEMENTS

PURPOSE	SHOWN	BURDENED LAND	BENEFITED LAND
RIGHT OF WAY & SERVICES	EE	LOT 6 HEREON	LOTS 1,3,4,5 HEREON
	EA G EB EC N O U		LOTS 3,4,5 HEREON
	W ED		LOTS 3,4 HEREON
	EF EG Y		LOTS 3 HEREON
	B C D		LOTS 2 & 8 HEREON
	A		LOT 2 HEREON

This drawing and design remains the property of, and may not be reproduced or amended without the written permission of Cato Bolam Consultants Ltd. No liability shall be accepted for unauthorised use of this drawing and design.

Auckland Council
Comprised in:

RT NA137A/506Ltd	57.4262ha
RT NA105B/748	24.1140ha
RT NA31C/965	21.6507ha
RT NA757/204Ltd	37.0692ha
RT NA2100/21Ltd	160.87ha
RT NA127B/898	1.1705ha
Total Area	302.3006ha

Areas and measurements are subject to survey.

- Riparian Margin Protection
- Significant Ecological Area
- Proposed Building Area
- Watercourse
- Extent of Flood Plain

Areas CP-CV (53.07ha) are to be subject to land covenants to protect native bush .

Areas CO CX-CZ Z (0.9ha) are to be subject to land covenants to protect riparian planting.

Cato Bolam
creating great places
PLANNERS | SURVEYORS | ENGINEERS
ARCHITECTS | ENVIRONMENTAL

R.C.& D.E. Nicklin
53B Remiger Road
Puhoi

Lots 1 - 8 being
Proposed Subdivision of
Lot 8 DP 208981, Lot 5 DP 198556
Lot 1 DP 179794, Allots 32,35,54A &
Pt Allots 30,31,36 Parish of Puhoi

FOR RESOURCE CONSENT

No.	REVISION (DESCRIPTIONS)	NAME	DATE
C	Lots 3 & 8 adjusted	MG	05/05/2023
D	Lots 3 & 6 adjusted Lots 9 & 10 added	MG	22/06/2023
E	Lot 8 adjusted OLFP deleted	MG	25/07/2023
F	Lot 3/6 bdy adjstd, Lots 9 & 10 deleted	MG	11/10/2023
SURVEYED			
DESIGNED			
DRAWN		LS	08/09/2017

DATE	ORIGINAL SCALE	ORIGINAL SIZE
11/10/2023	1:2000	A3

DRAWING NO. 40320-DR-PLN-1201
REVISION F