RECORD OF TITLE
UNDER LAND TRANSFER ACT 2017
FREEHOLD

Search Copy

R.W. Muir
Registrar-General
of Land

Identifier **974873**

Land Registration District **North Auckland**

Date Issued 15 September 2021

Prior References
NA127B/898

Estate Fee Simple

Area 635 square metres more or less

Legal Description Lot 9 Deposited Plan 541977

Registered Owners

Raymond Charles Nicklin as to a 1/2 share

Desma Elizabeth Nicklin as to a 1/2 share

Interests

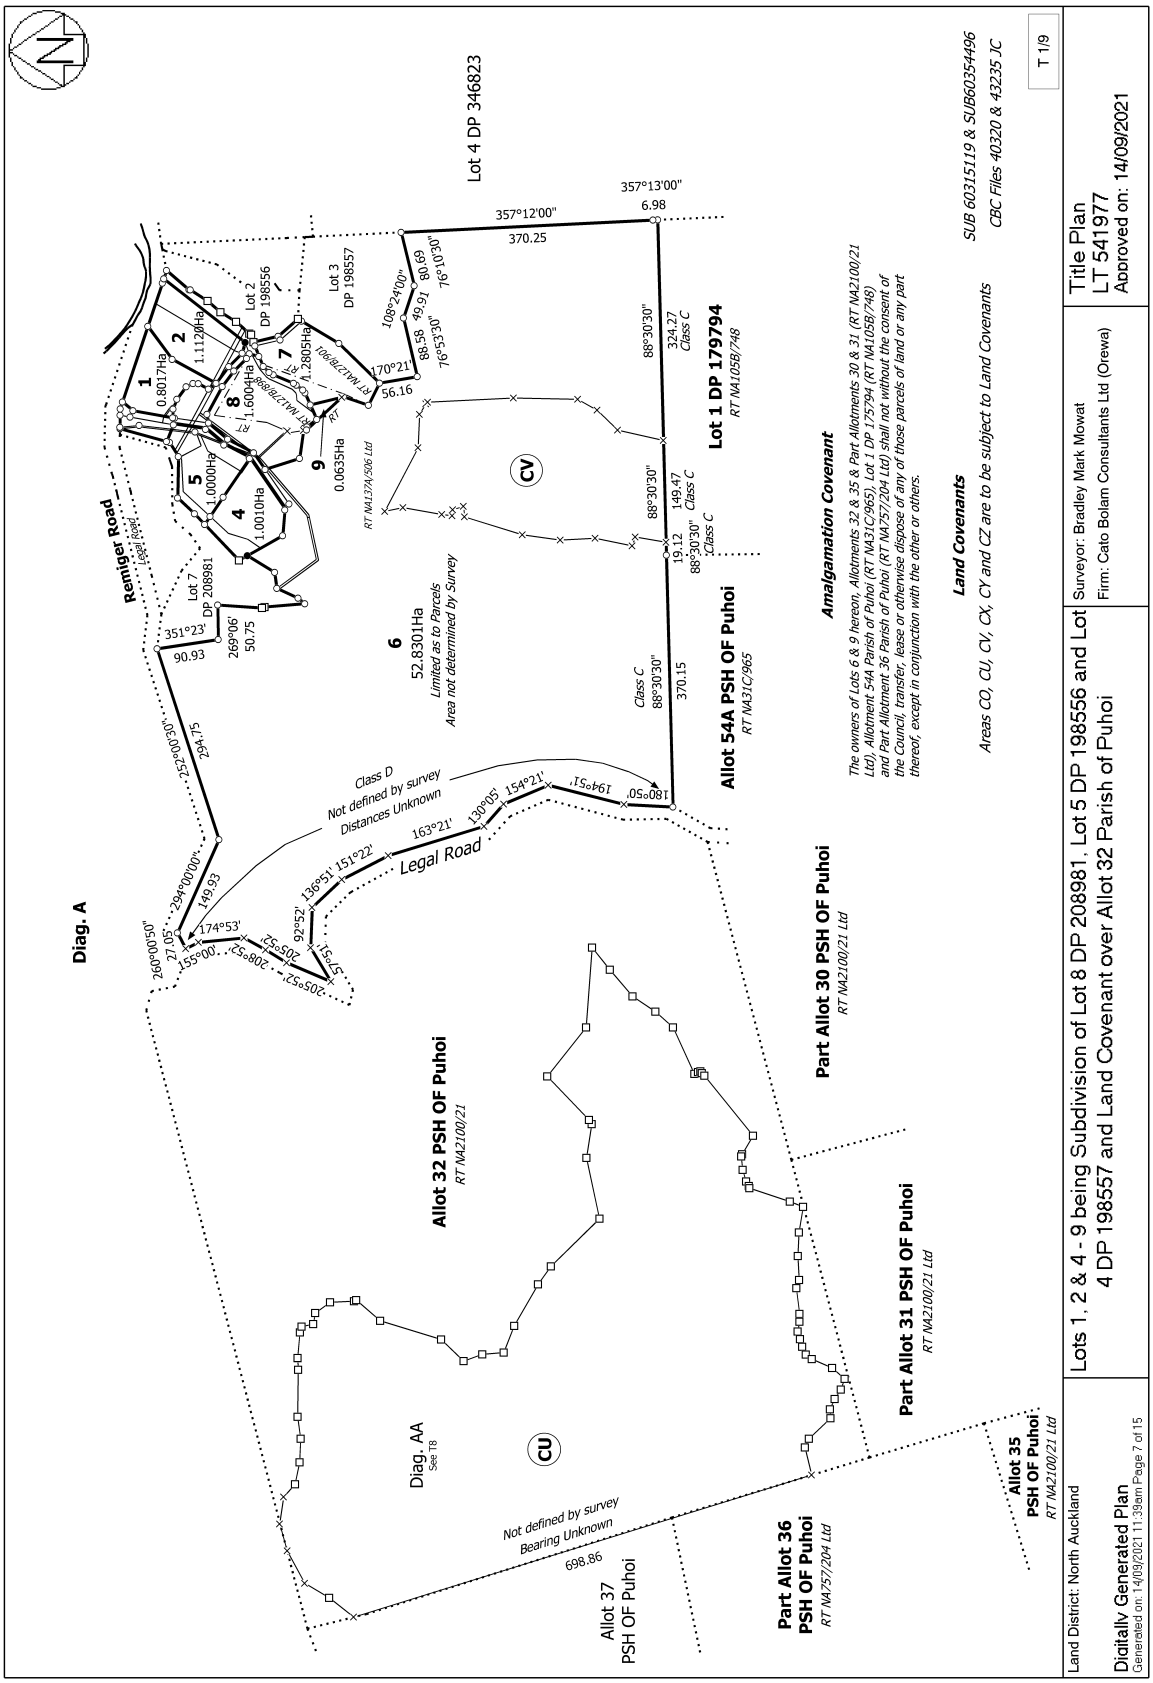
Appurtenant hereto is a right of way and telecommunications and electricity rights specified in Easement Certificate D460766.5 - produced 9.12.1999 at 12.34 pm and entered 1.2.2000 at 9.00 am

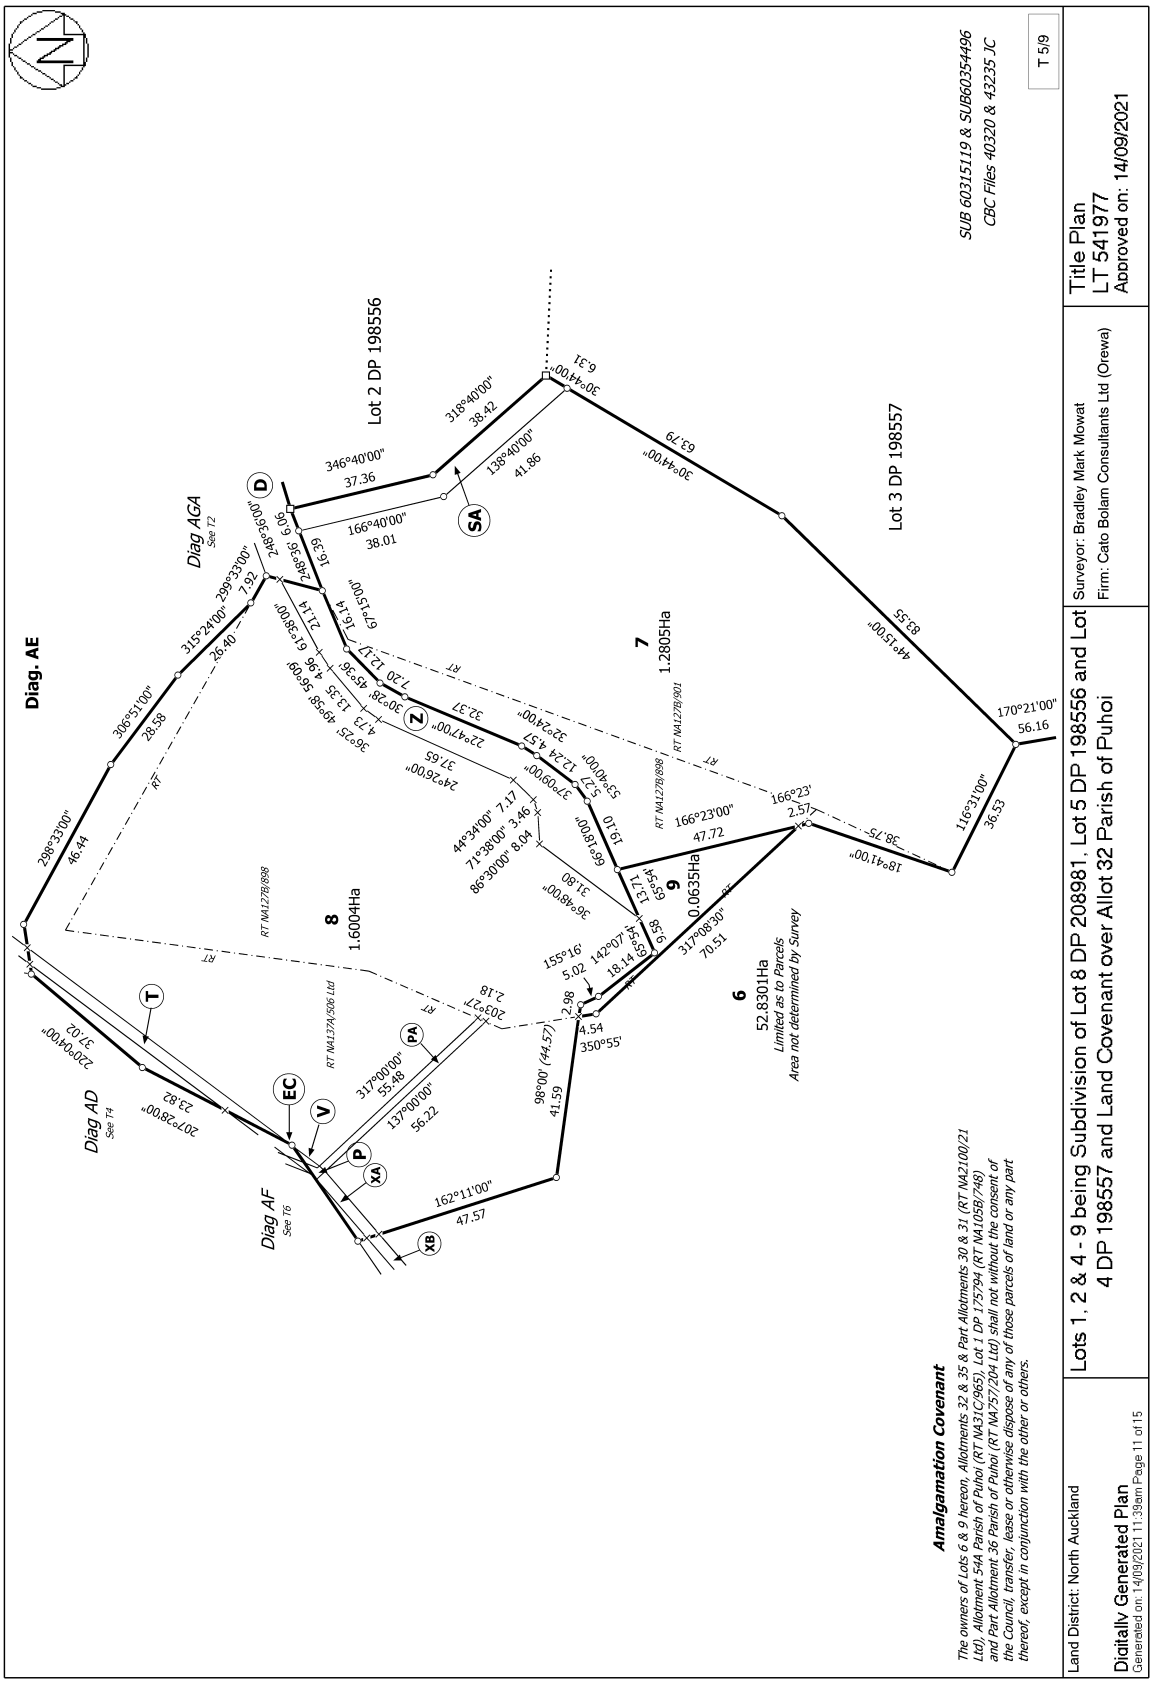
Some of the easements specified in Easement Certificate D460766.5 are subject to Section 243 (a) Resource Management Act 1991 (see DP 198556)

12243692.8 Consent Notice pursuant to Section 221 Resource Management Act 1991 - 15.9.2021 at 12:21 pm

Appurtenant hereto is a right of way and a right to convey electricity and telecommunications created by Easement Instrument 12243692.12 - 15.9.2021 at 12:21 pm

12888387.3 COVENANT UNDER SECTION 240 RESOURCE MANAGEMENT ACT 1991 (ALSO AFFECTS 1159734, NA105B/748, NA2100/21, NA31C/965 and NA757/204) - 23.6.2025 at 3:08 pm


Lot 4 DP 346823
357°13'00"
6.98
357°12'00"
370.25
Remiger Road
Legal Road
Lot 2 DP 198556
Lot 3 DP 198557
Lot 7 DP 208981
1 0.8017Ha
2 1.1120Ha
4 1.0010Ha
5 1.0000Ha
7 0.2805Ha
8 1.6004Ha
9 0.0635Ha
RT NA137A/506 Ltd
6 52.8301Ha
Limited as to Parcels
Area not determined by Survey
Lot 1 DP 179794
RT NA1058/748
Allot 54A PSH OF Puhoi
RT NA31C/965
Class C
Class D
Not defined by survey
Distances Unknown
Legal Road
Allot 32 PSH OF Puhoi
RT NA2100/21
Part Allot 30 PSH OF Puhoi
RT NA2100/21 Ltd
Part Allot 31 PSH OF Puhoi
RT NA2100/21 Ltd
Part Allot 36 PSH OF Puhoi
RT NA757/204 Ltd
Allot 35 PSH OF Puhoi
RT NA2100/21 Ltd
Allot 37 PSH OF Puhoi
Diag. AA
See T8
Not defined by survey
Bearing Unknown
698.86
Diag. A
Amalgamation Covenant
The owners of Lots 6 & 9 hereon, Allotments 32 & 35 & Part Allotments 30 & 31 (RT NA2100/21 Ltd), Allotment 544 Parish of Puhoi (RT NA31C/965), Lot 1 DP 175794 (RT NA1058/748) and Part Allotment 36 Parish of Puhoi (RT NA757/204 Ltd) shall not without the consent of the Council, transfer, lease or otherwise dispose of any of those parcels of land or any part thereof, except in conjunction with the other or others.
Land Covenants
Areas CO, CU, CV, CX, CY and CZ are to be subject to Land Covenants
SUB 60315119 & SUB60354496
CBC Files 40320 & 43235 JC
T 1/9
Land District: North Auckland
Lots 1, 2 & 4 - 9 being Subdivision of Lot 8 DP 208981, Lot 5 DP 198556 and Lot 4 DP 198557 and Land Covenant over Allot 32 Parish of Puhoi
Surveyor: Bradley Mark Mowat
Firm: Cato Bolam Consultants Ltd (Orewa)
Title Plan
LT 541977
Approved on: 14/09/2021
Digitally Generated Plan
Generated on: 14/09/2021 11:39am Page 7 of 15


Diag. AE
Diag AD
See T4
Diag AF
See T6
Diag AGA
See T2
Lot 2 DP 198556
Lot 3 DP 198557
RT NA127B/898
RT NA127B/901
RT NA137A/506 Ltd
RT
6
52.8301Ha
Limited as to Parcels
Area not determined by Survey
7
1.2805Ha
8
1.6004Ha
9
0.0635Ha
SUB 60315119 & SUB60354496
CBC Files 40320 & 43235 JC
T 5/9
Amalgamation Covenant
The owners of Lots 6 & 9 hereon, Allotments 32 & 35 & Part Allotments 30 & 31 (RT NA2100/21 Ltd), Allotment 54A Parish of Puhoi (RT NA31C/965), Lot 1 DP 175794 (RT NA105B/748) and Part Allotment 36 Parish of Puhoi (RT NA757/204 Ltd) shall not without the consent of the Council, transfer, lease or otherwise dispose of any of those parcels of land or any part thereof, except in conjunction with the other or others.
Land District: North Auckland
Digitally Generated Plan
Generated on: 14/09/2021 11:39am Page 11 of 15
Lots 1, 2 & 4 - 9 being Subdivision of Lot 8 DP 208981, Lot 5 DP 198556 and Lot 4 DP 198557 and Land Covenant over Allot 32 Parish of Puhoi
Surveyor: Bradley Mark Mowat
Firm: Cato Bolam Consultants Ltd (Orewa)
Title Plan
LT 541977
Approved on: 14/09/2021