RECORD OF TITLE
UNDER LAND TRANSFER ACT 2017
FREEHOLD

Search Copy

R.W. Muir
Registrar-General
of Land

Identifier	**NA105B/748**
Land Registration District	**North Auckland**
Date Issued	19 December 1996

Prior References
NA31C/964

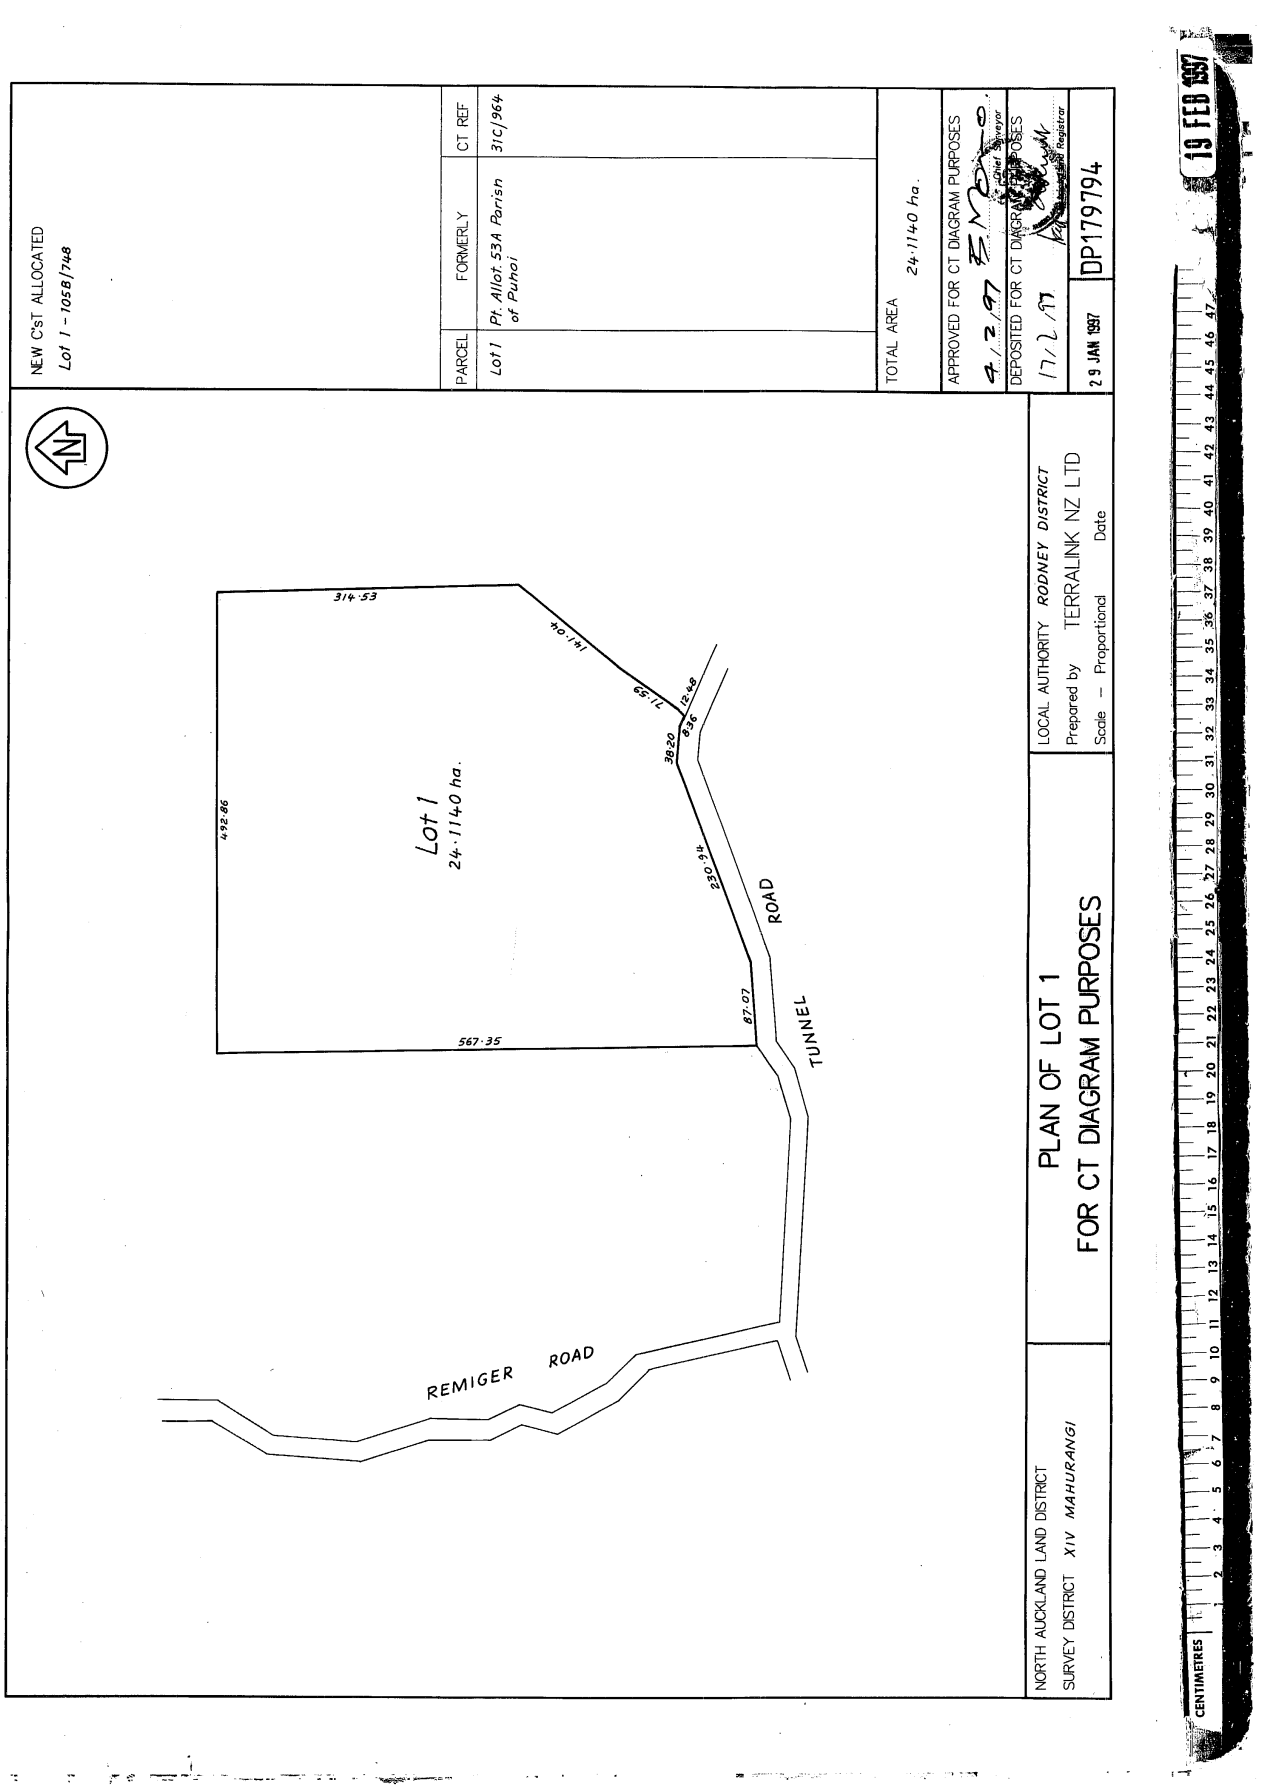
Estate	Fee Simple
Area	24.1140 hectares more or less
Legal Description	Lot 1 Deposited Plan 179794
Registered Owners	

Raymond Charles Nicklin and Desma Elizabeth Nicklin

Interests

Subject to Section 59 Land Act 1948

12888387.3 COVENANT UNDER SECTION 240 RESOURCE MANAGEMENT ACT 1991 (ALSO AFFECTS 1159734, 974873, NA2100/21, NA31C/965 and NA757/204) - 23.6.2025 at 3:08 pm


NEW C'ST ALLOCATED
Lot 1 - 105B/748
PARCEL
FORMERLY
CT REF
Lot 1
Pt. Allot. 53A Parish of Punoi
31C/964
TOTAL AREA
24.1140 ha.
APPROVED FOR CT DIAGRAM PURPOSES
4.2.97
Chief Surveyor
DEPOSITED FOR CT DIAGRAM PURPOSES
17/2/97
Land Registrar
29 JAN 1997
DP179794
Lot 1
24.1140 ha.
314.53
40.141
65.72
12.48
8.36
38.20
230.94
87.07
567.35
492.86
ROAD
TUNNEL
REMIGER ROAD
PLAN OF LOT 1
FOR CT DIAGRAM PURPOSES
NORTH AUCKLAND LAND DISTRICT
SURVEY DISTRICT XIV MAHURANGI
LOCAL AUTHORITY RODNEY DISTRICT
Prepared by TERRALINK NZ LTD
Scale - Proportional Date
19 FEB 1997
CENTIMETRES