# Title Plan - LT 598139

| | |
|---|---|
| **Survey Number** | LT 598139 |
| **Surveyor Reference** | 40320 Nicklin -stage 2 |
| **Surveyor** | Bradley Mark Mowat |
| **Survey Firm** | Cato Bolam Consultants Ltd (Orewa) |
| **Surveyor Declaration** | |

**Survey Details**

| | | | |
|---|---|---|---|
| **Dataset Description** | Lots 3 & 6 Being Subdivision of Lot 6 DP 541977 and Covenant over Allot 32 Parish of Puhoi | | |
| **Status** | Initiated | | |
| **Land District** | North Auckland | **Survey Class** | Class B |
| **Submitted Date** | | **Survey Approval Date** | |
| | | **Deposit Date** | |

**Territorial Authorities**

Auckland Council

**Comprised In**

RT 974873
RT NA105B/748
RT NA2100/21 Ltd
RT NA31C/965
RT NA757/204 Ltd
RT 911735 Ltd

**Created Parcels**

| Parcels | Parcel Intent | Area | RT Reference |
|---|---|---|---|
| Lot 3 Deposited Plan 598139 | Fee Simple Title | 0.8110 Ha | 1159733 |
| Lot 6 Deposited Plan 598139 | Fee Simple Title | 52.0191 Ha | 1159734 |
| Area B Deposited Plan 598139 | Easement | | |
| Area C Deposited Plan 598139 | Easement | | |
| Area CS Deposited Plan 598139 | Covenant - Land | | |
| Area CT Deposited Plan 598139 | Covenant - Land | | |
| Area CV Deposited Plan 598139 | Covenant - Land | | |
| Area D Deposited Plan 598139 | Easement | | |
| Area EA Deposited Plan 598139 | Easement | | |
| Area EB Deposited Plan 598139 | Easement | | |
| Area ED Deposited Plan 598139 | Easement | | |
| Area EE Deposited Plan 598139 | Easement | | |
| Area EF Deposited Plan 598139 | Easement | | |
| Area EG Deposited Plan 598139 | Easement | | |
| Area F Deposited Plan 598139 | Easement | | |
| Area G Deposited Plan 598139 | Easement | | |
| Area NA Deposited Plan 598139 | Easement | | |
| Area O Deposited Plan 598139 | Easement | | |

# Title Plan - LT 598139

**Created Parcels**

| Parcels | Parcel Intent | Area | RT Reference |
|---|---|---|---|
| Area TA Deposited Plan 598139 | Easement | | |
| Area U Deposited Plan 598139 | Easement | | |
| Area XA Deposited Plan 598139 | Easement | | |
| Area Y Deposited Plan 598139 | Easement | | |
| Area YA Deposited Plan 598139 | Easement | | |
| Area YB Deposited Plan 598139 | Easement | | |
| Area YC Deposited Plan 598139 | Easement | | |
| Area EC Deposited Plan 598139 | Easement | | |
| **Total Area** | | 52.8301 Ha | |

Our Ref: 40320

Cato Bolam
creating great places

**Land Registration District**
North Auckland

**Plan Number**
DP 598139 (stage 2)

**Territorial Authority**
Auckland Council

**TA Reference**
SUB60315119-A

| MEMORANDUM OF EASEMENT(S) | | | |
|---|---|---|---|
| Purpose | Shown | Servient Tenement (Burdened Land) | Dominant Tenement (Benefited Land) |
| Right of Way, right to convey water, electricity & telecommunications | EE, EA, G, EB, NA, U, EC, O, ED, EF, EG, Y & YC | Lot 6 hereon | Lot 3 hereon |

| SCHEDULE OF EXISTING EASEMENTS | | | |
|---|---|---|---|
| Purpose | Shown | Servient Tenement (Burdened Land) | Creating Document |
| Right of Way, right to convey water, electricity & telecommunications | EA, EB, EC, ED, EE, G, NA, O & U | Lot 6 hereon | Easement Instrument 12243692.10 |
| Right of Way & telecommunications right | B, C & D | | Easement Certificate D460766.5 |
| | B, C & D | | Easement Certificate D611644.6 |
| Electricity Right | TA, O & U | | Easement Certificate D460766.5 |
| Telecommunications right | K, O & NA | | Easement Certificate D460766.5 |
| Right to transmit electricity | O, TA, U, XA, Y, YA, YB & YC | | Easement Instrument 6170820.9 |
| Right to transmit telecommunications | K, NA, O, XA, Y, YA, YB & YC | | Easement Instrument 6170820.9 |

| SCHEDULE OF EXISTING EASEMENT(S) IN GROSS | | | |
|---|---|---|---|
| Purpose | Shown | Servient Tenement (Burdened Land) | Creating Document |
| Right to Convey Electricity | O, U, TA, XA & YC | Lot 6 hereon | Easement Instrument 12243692.11 |

**Proposed Covenants**

Areas CS and CT are to be subject to Land Covenants to protect the native bush within.


**Existing Covenants**

Area CV is subject to an existing Land Covenant to protect native bush within, created by Consent Notice 12243692.8.

**Amalgamation Covenant**

The owner of Lot 6 hereon, Lot 9 DP 541977 (RT 974873), Allotments 32 & 35 and Part Allotments 30 & 31 (RT NA2100/21 Ltd), Allotment 54A Parish of Puhoi (RT NA31C/965), Lot 1 DP 179794 (RT NA105B/748) and Part Allotment 36 Parish of Puhoi (RT NA757/204 Ltd) shall not without the consent of Council , transfer, lease or otherwise dispose of any of those parcels of land or any part thereof, except in conjunction with the other or others.

**Diag. A**

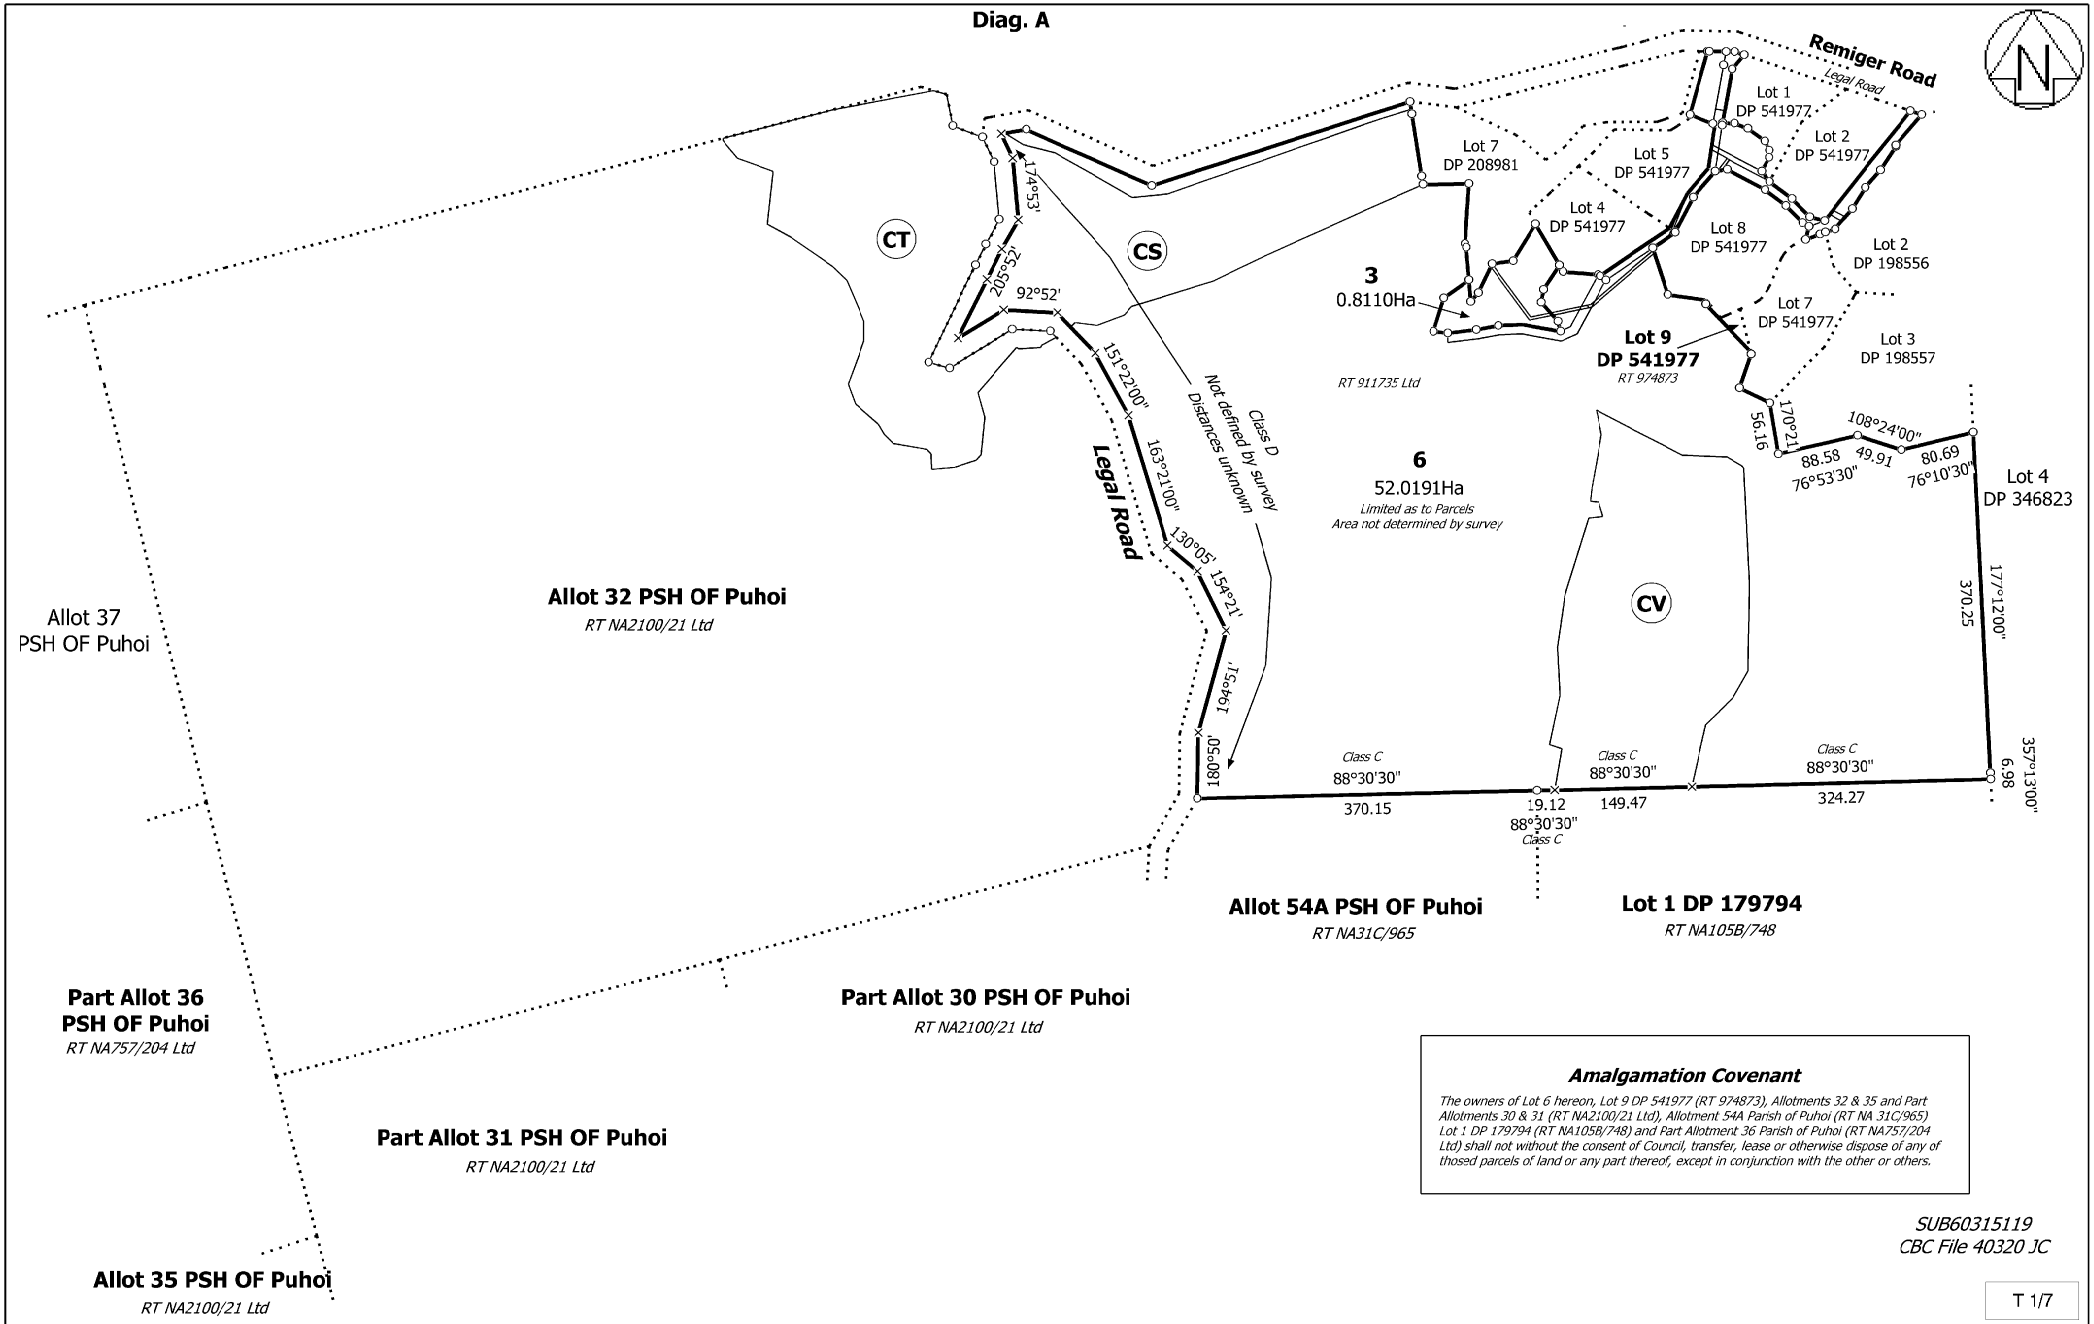



***Amalgamation Covenant***

*The owners of Lot 6 hereon, Lot 9 DP 541977 (RT 974873), Allotments 32 & 35 and Part Allotments 30 & 31 (RT NA2100/21 Ltd), Allotment 54A Parish of Puhoi (RT NA 31C/965) Lot 1 DP 179794 (RT NA105B/748) and Part Allotment 36 Parish of Puhoi (RT NA757/204 Ltd) shall not without the consent of Council, transfer, lease or otherwise dispose of any of thosed parcels of land or any part thereof, except in conjunction with the other or others.*

*SUB60315119*
*CBC File 40320 JC*

T 1/7

| | | | |
|---|---|---|---|
| Land District: North Auckland<br><br>Digitally Generated Plan<br>Generated on: 15/11/2023 11:51am Page 5 of 11 | Lots 3 & 6 Being Subdivision of Lot 6 DP 541977 and Covenant over Allot 32 Parish of Puhoi | Surveyor: Bradley Mark Mowat<br>Firm: Cato Bolam Consultants Ltd (Orewa) | Title Plan<br>LT 598139<br>DRAFT |

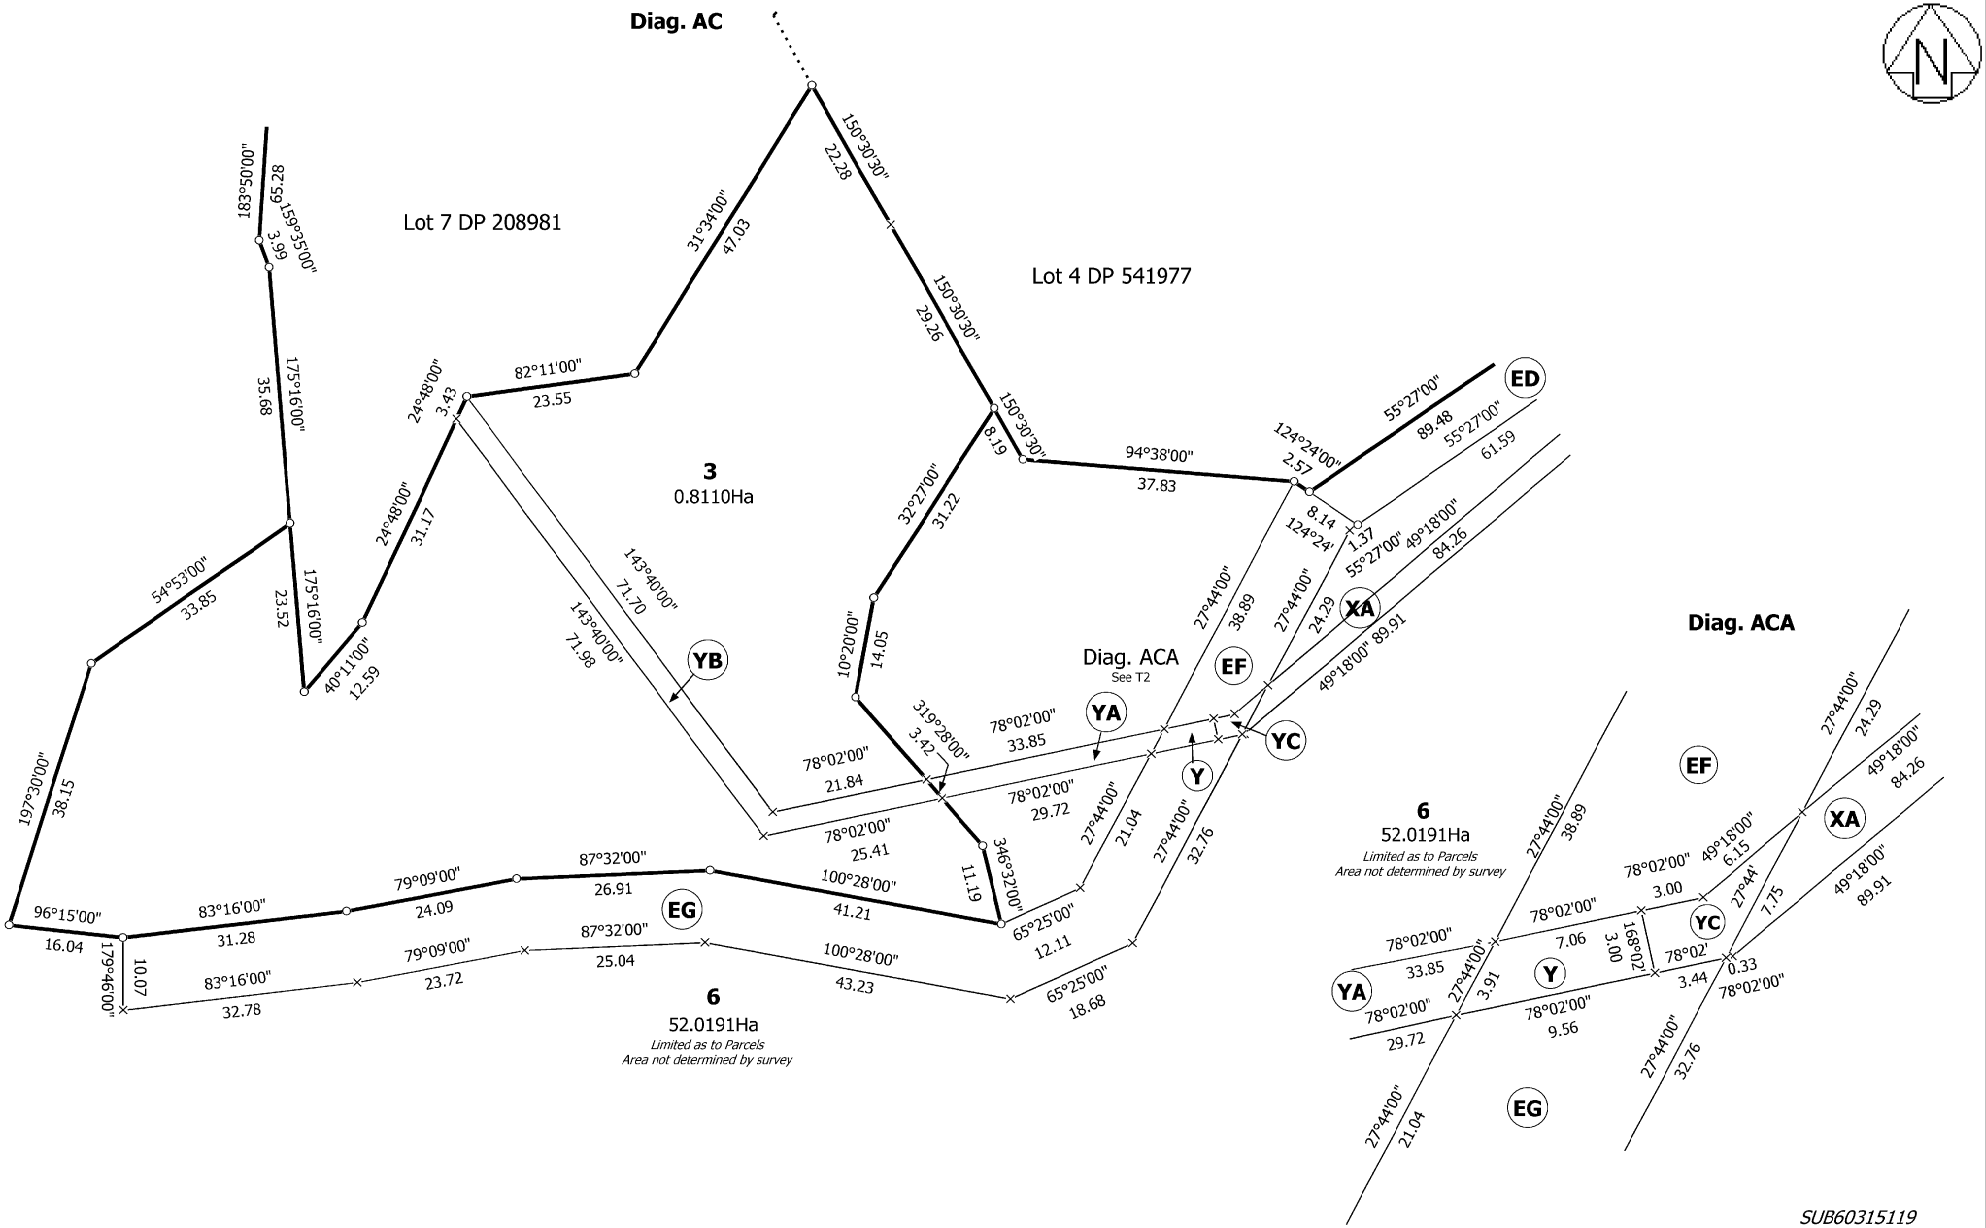



*SUB60315119*
*CBC File 40320 JC*

T 2/7

| | | | |
|---|---|---|---|
| Land District: North Auckland<br><br>Digitally Generated Plan<br>Generated on: 15/11/2023 11:51am Page 6 of 11 | Lots 3 & 6 Being Subdivision of Lot 6 DP 541977 and Covenant over Allot 32 Parish of Puhoi | Surveyor: Bradley Mark Mowat<br>Firm: Cato Bolam Consultants Ltd (Orewa) | Title Plan<br>LT 598139<br>DRAFT |


**Diag. B**

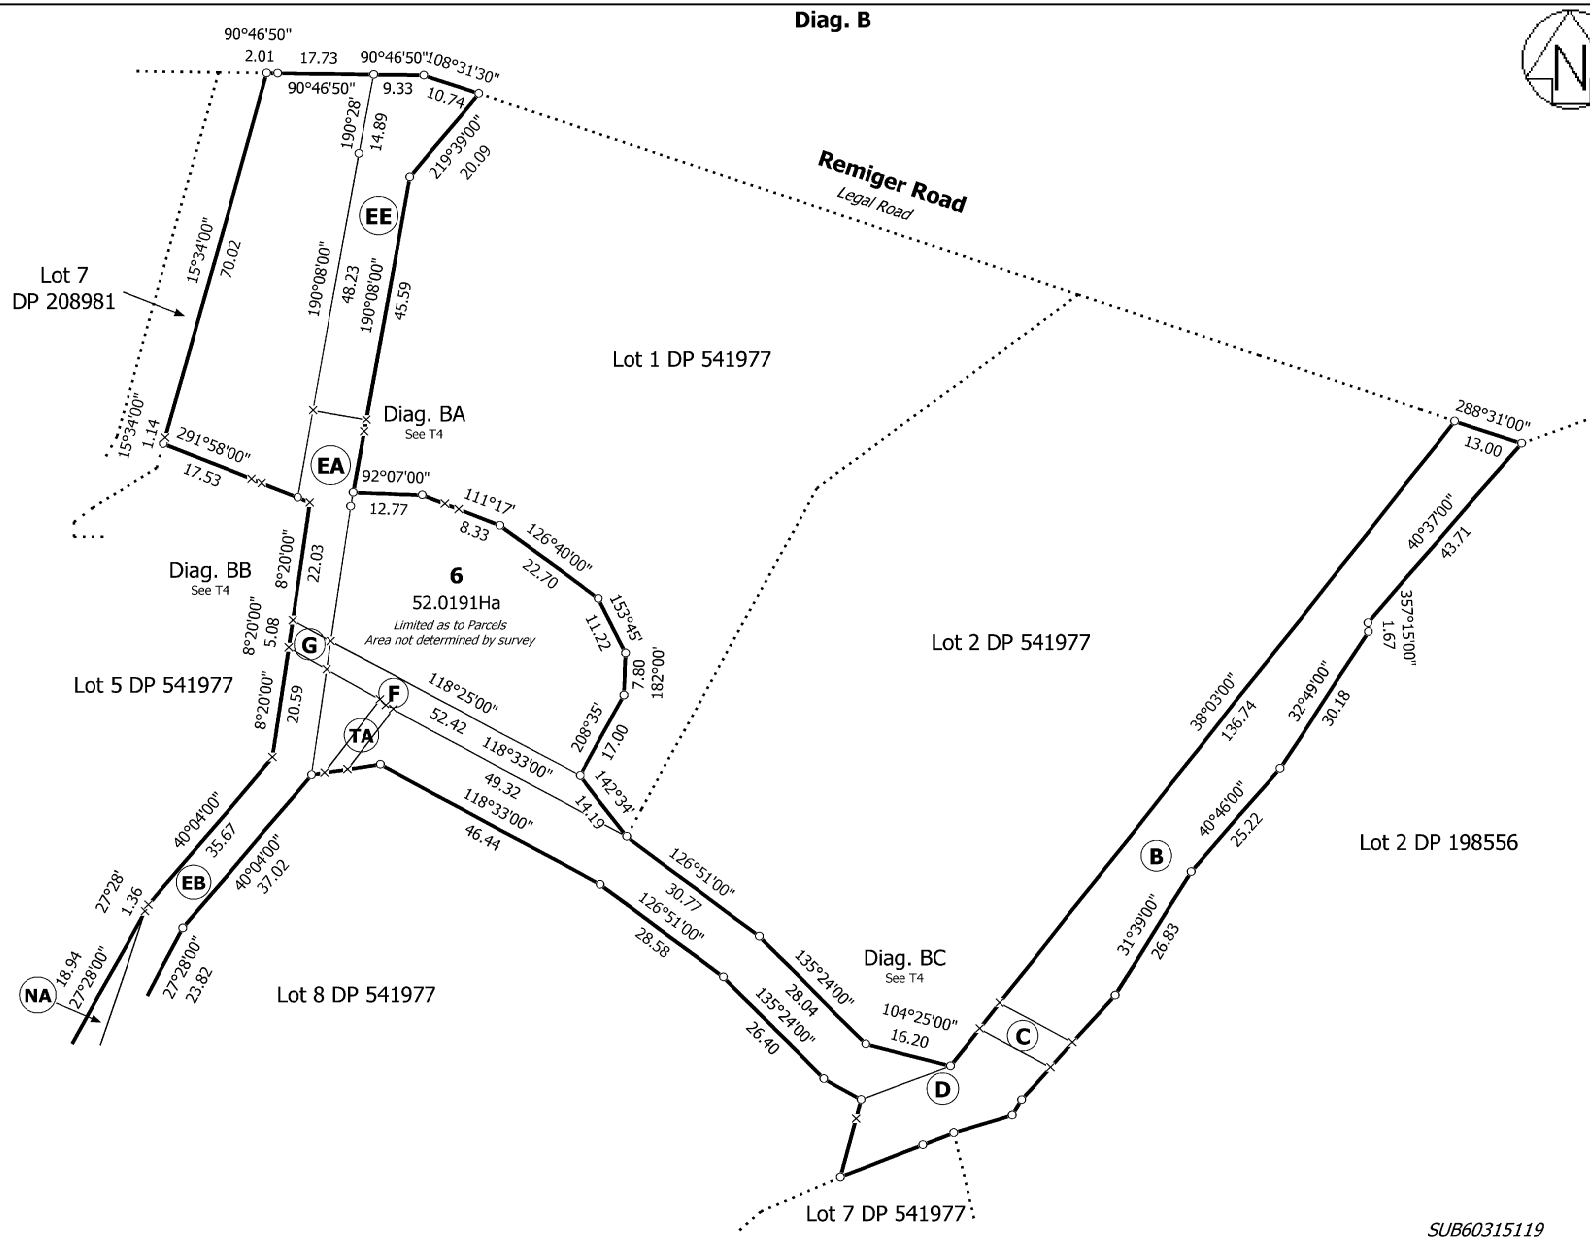


*SUB60315119*
*CBC File 40320 JC*


T 3/7

| | | | |
|---|---|---|---|
| Land District: North Auckland<br><br>Digitally Generated Plan<br>Generated on: 15/11/2023 11:51am Page 7 of 11 | Lots 3 & 6 Being Subdivision of Lot 6 DP 541977 and Covenant over Allot 32 Parish of Puhoi | Surveyor: Bradley Mark Mowat<br>Firm: Cato Bolam Consultants Ltd (Orewa) | Title Plan<br>LT 598139<br>DRAFT |

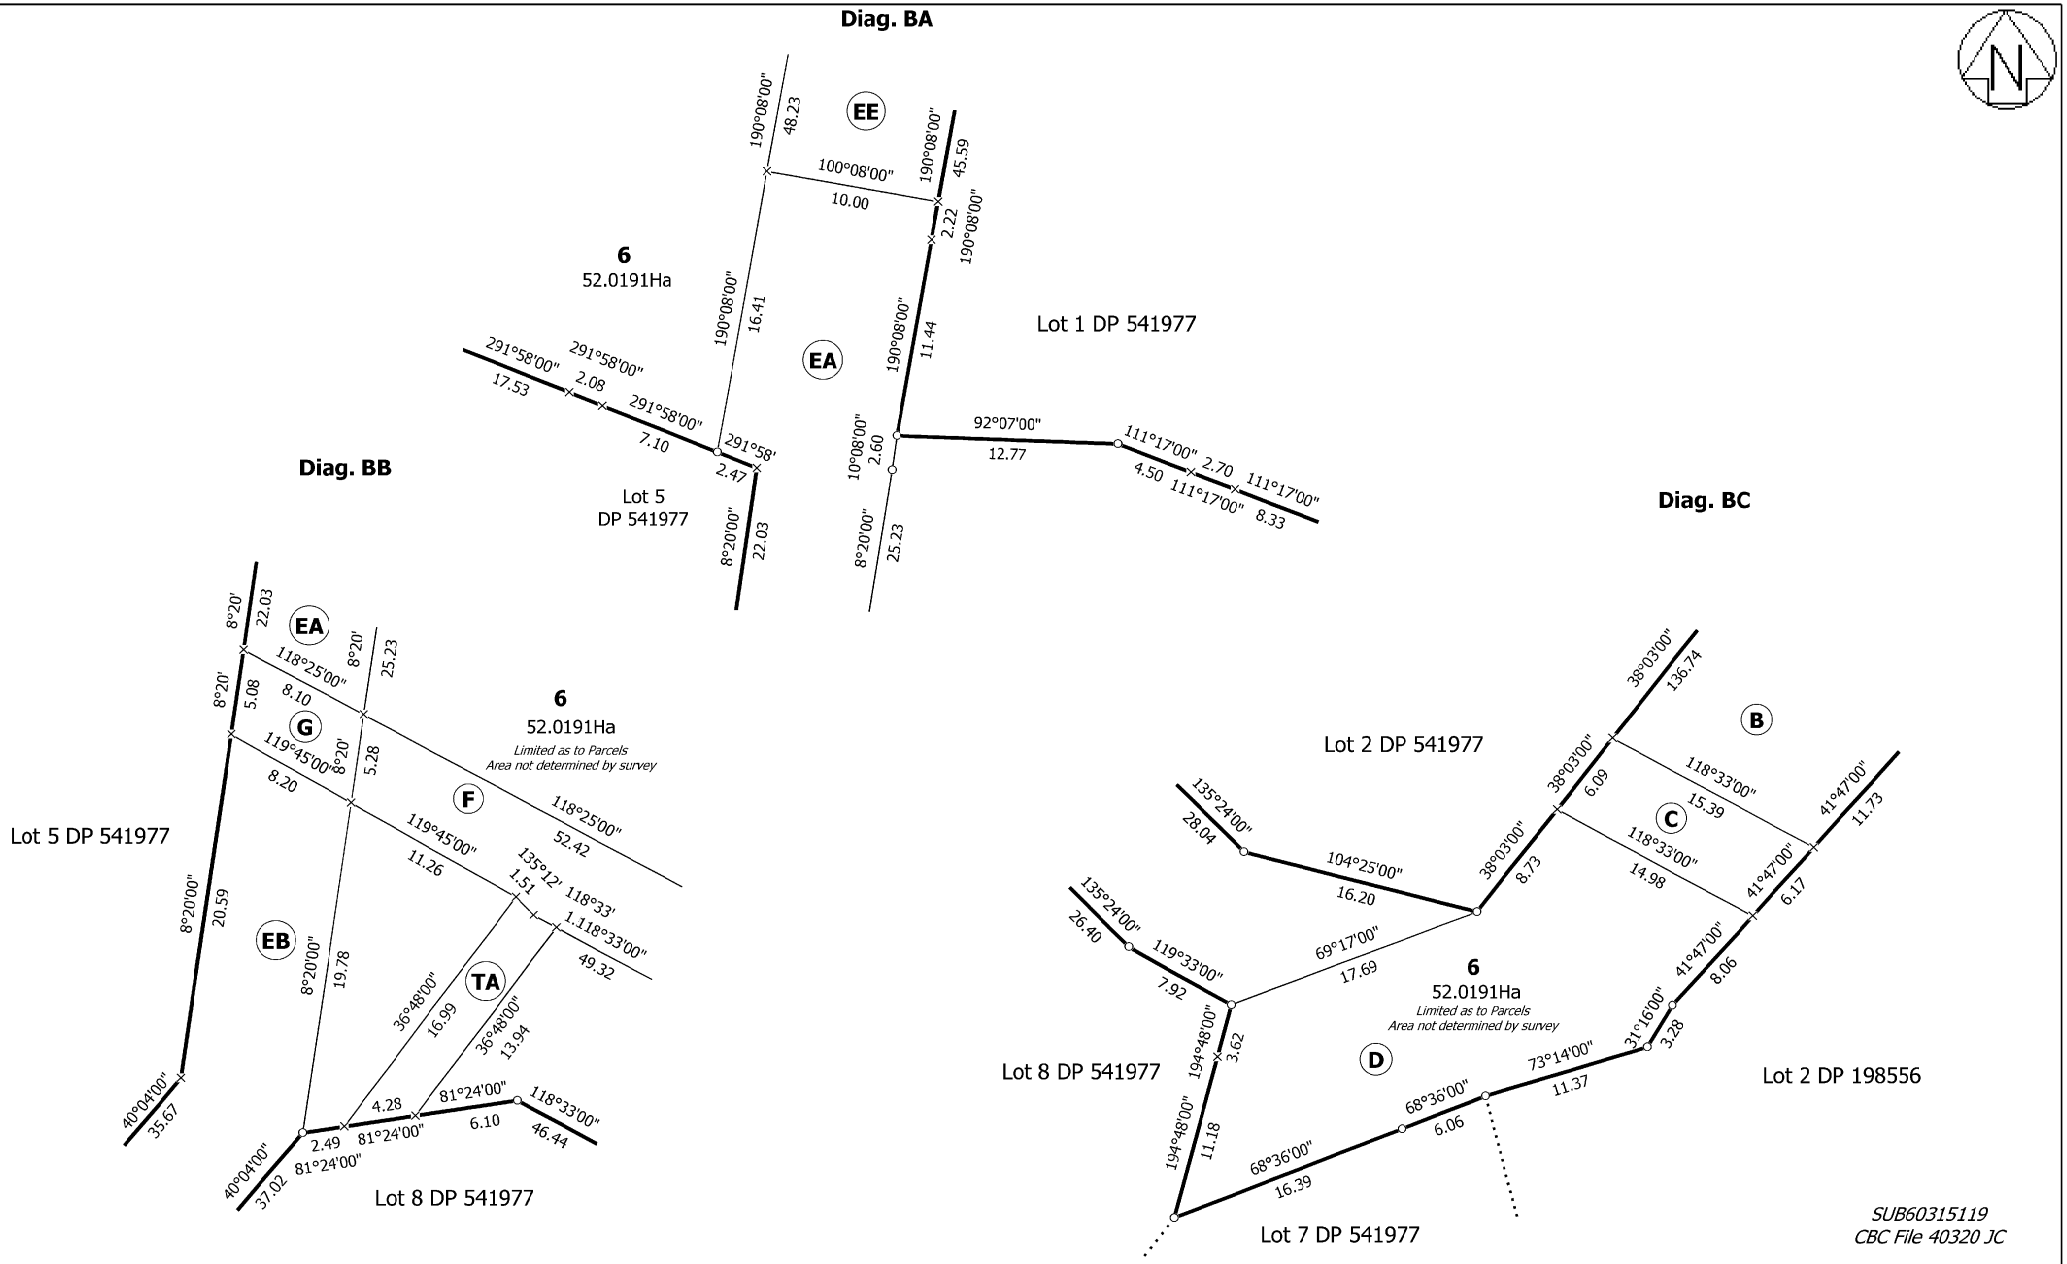



T 4/7

| | | | |
|---|---|---|---|
| Land District: North Auckland<br><br>Digitally Generated Plan<br>Generated on: 15/11/2023 11:51am Page 8 of 11 | Lots 3 & 6 Being Subdivision of Lot 6 DP 541977 and Covenant over Allot 32 Parish of Puhoi | Surveyor: Bradley Mark Mowat<br>Firm: Cato Bolam Consultants Ltd (Orewa) | Title Plan<br>LT 598139<br>DRAFT |

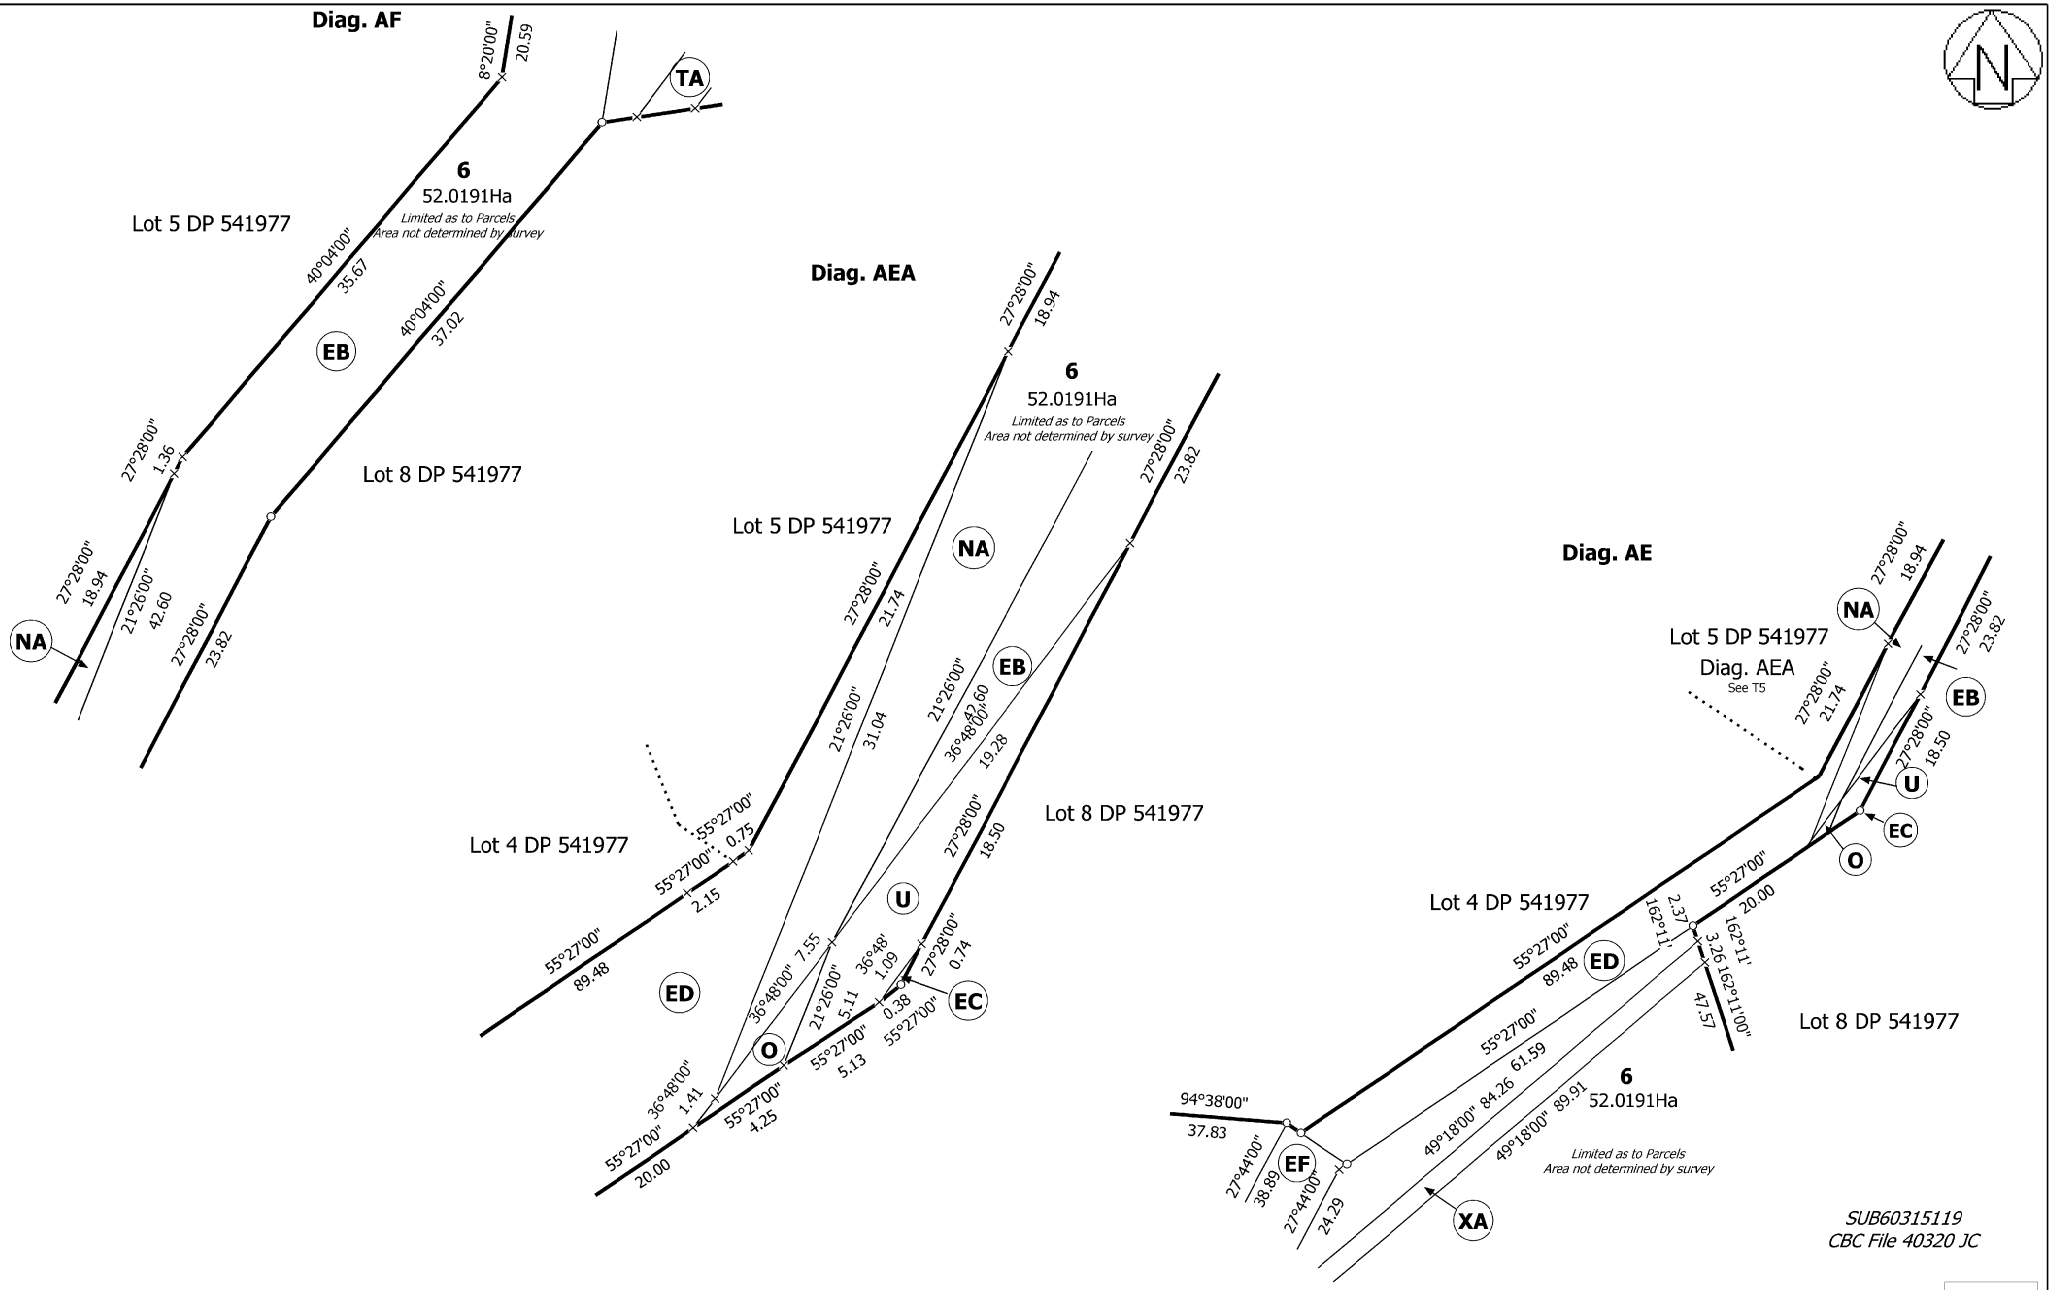


| | | | |
|---|---|---|---|
| Land District: North Auckland<br><br>Digitally Generated Plan<br>Generated on: 15/11/2023 11:51am Page 9 of 11 | Lots 3 & 6 Being Subdivision of Lot 6 DP 541977 and Covenant over Allot 32 Parish of Puhoi | Surveyor: Bradley Mark Mowat<br>Firm: Cato Bolam Consultants Ltd (Orewa) | Title Plan<br>LT 598139<br>DRAFT |

**Diag. AB**

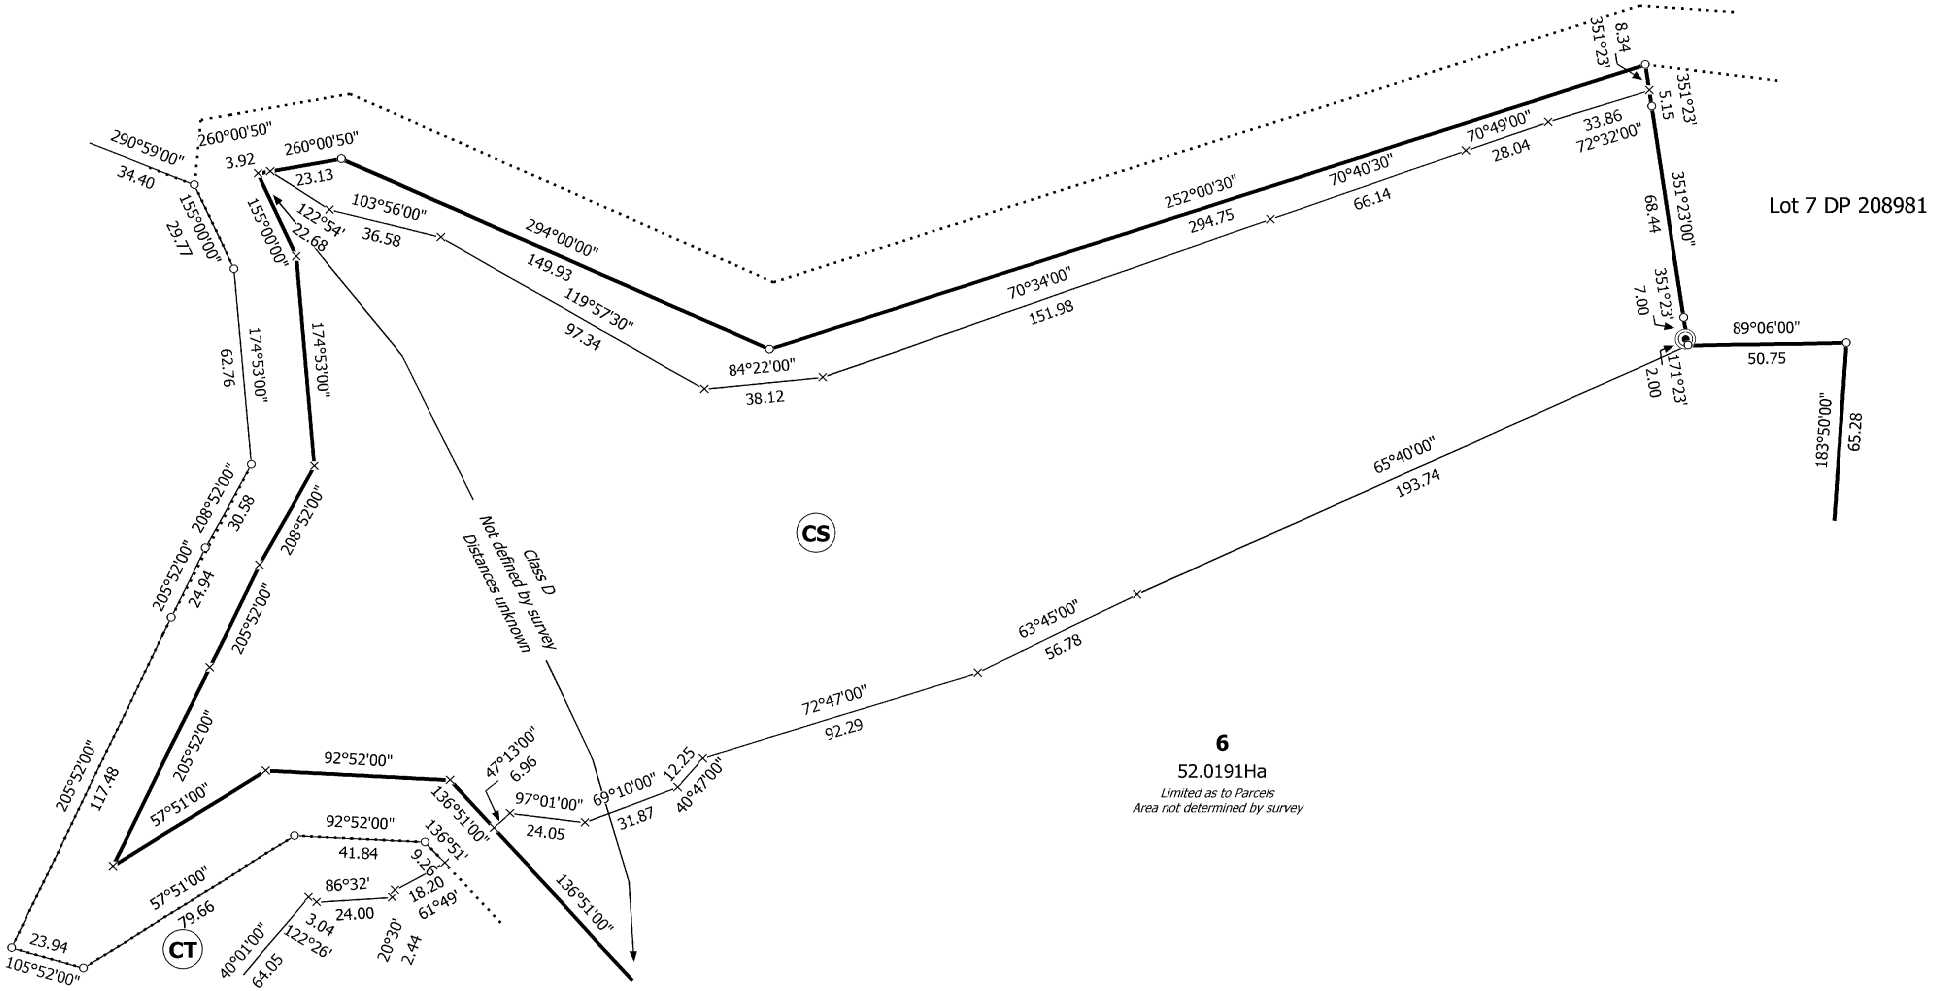


**Allot 32 PSH OF Puhoi**


*RT NA2100/21 Ltd*

*SUB60315119*
*CBC File 40320 JC*

T 6/7

| | | | |
|---|---|---|---|
| Land District: North Auckland<br><br>Digitally Generated Plan<br>Generated on: 15/11/2023 11:51am Page 10 of 11 | Lots 3 & 6 Being Subdivision of Lot 6 DP 541977 and Covenant over Allot 32 Parish of Puhoi | Surveyor: Bradley Mark Mowat<br>Firm: Cato Bolam Consultants Ltd (Orewa) | Title Plan<br>LT 598139<br>DRAFT |

**Diag. AA**

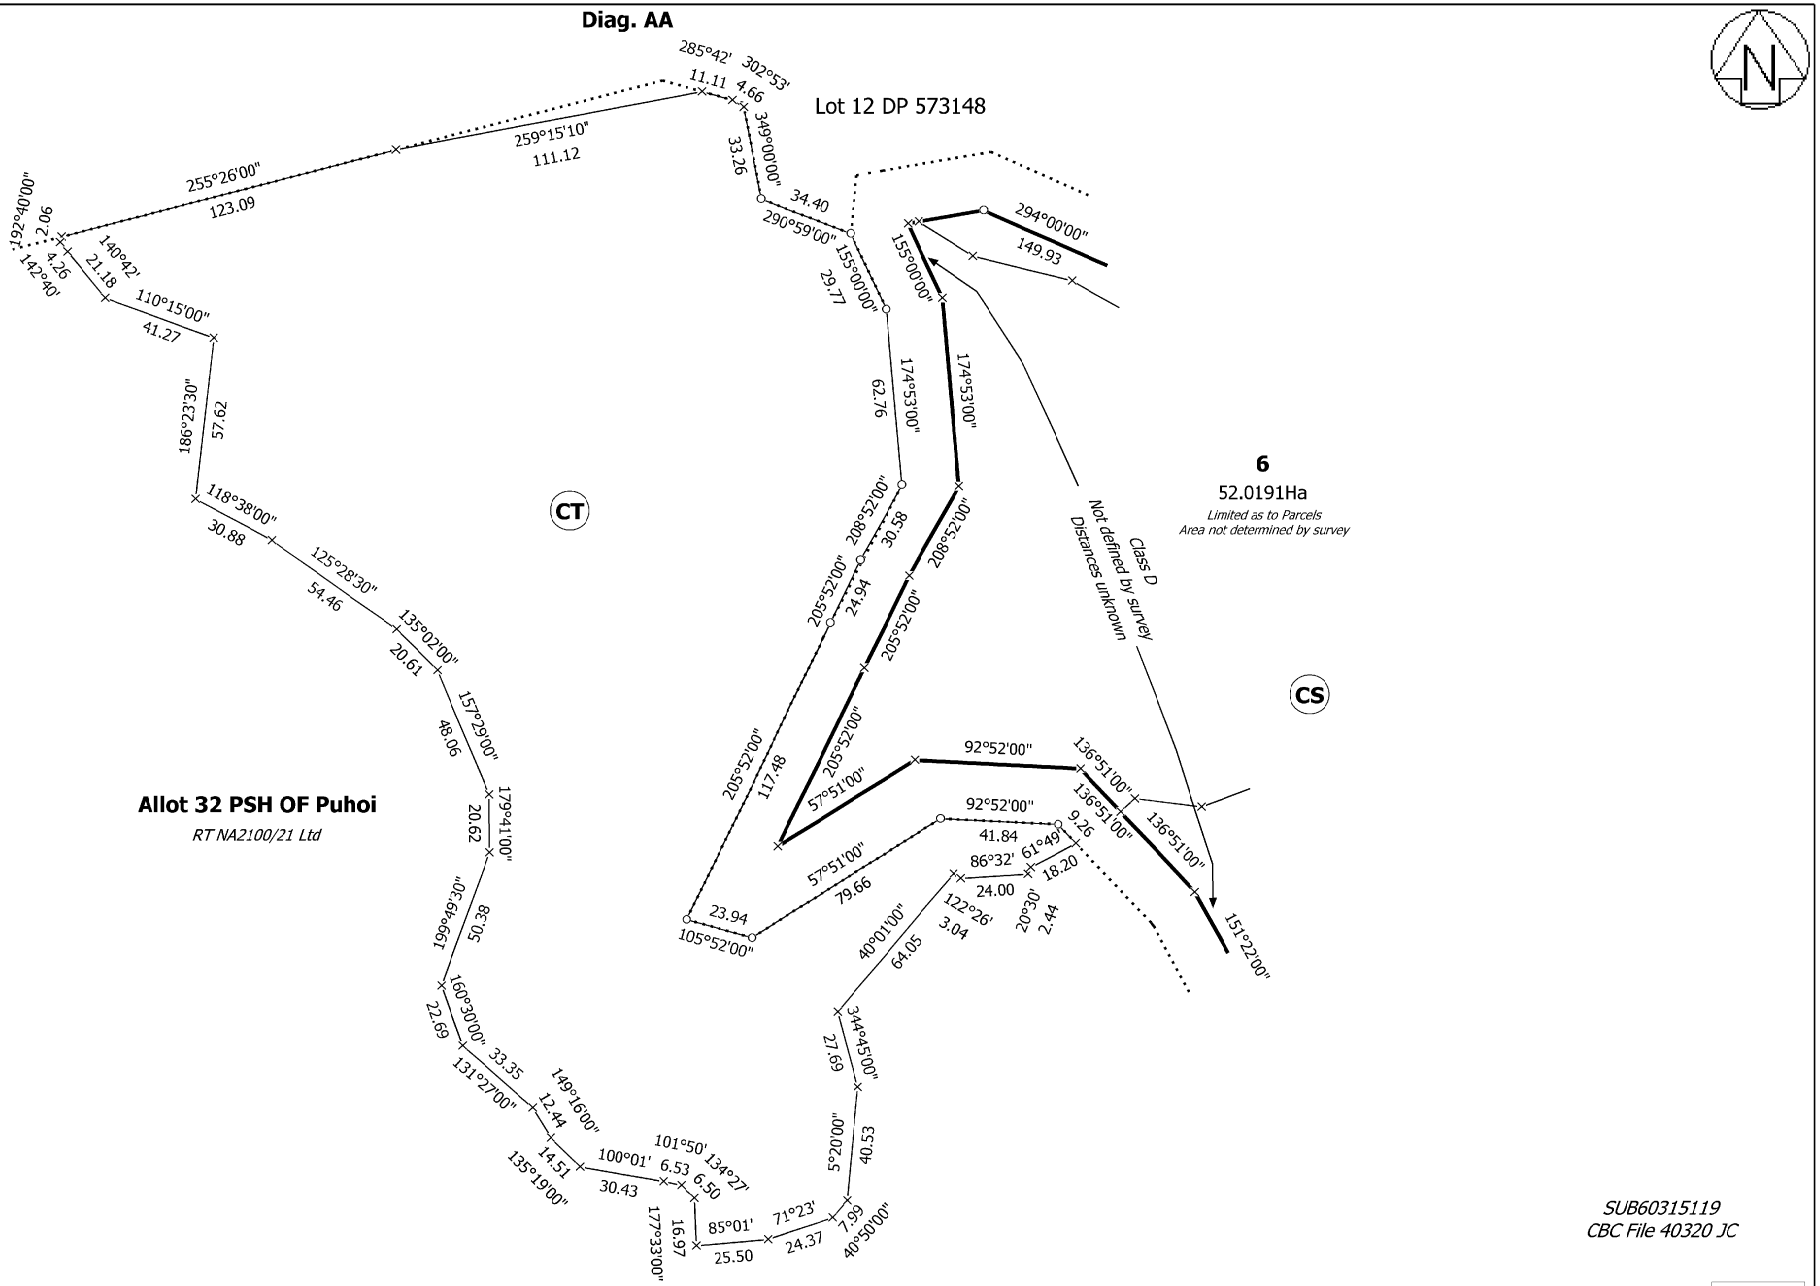


*SUB60315119*
*CBC File 40320 JC*

T 7/7

| | | | |
|---|---|---|---|
| Land District: North Auckland<br><br>Digitally Generated Plan<br>Generated on: 15/11/2023 11:51am Page 11 of 11 | Lots 3 & 6 Being Subdivision of Lot 6 DP 541977 and Covenant over Allot 32 Parish of Puhoi | Surveyor: Bradley Mark Mowat<br>Firm: Cato Bolam Consultants Ltd (Orewa) | Title Plan<br>LT 598139<br>DRAFT |