Ray Nicklin and Desma Nicklin

53B Remiger Road, Puhoi

Resource Consent Application

Cato Bolam
creating great places

<u>Appendix B:</u> Copy of Records of Title

PLANNERS
SURVEYORS
ENGINEERS
ARCHITECTS
ENVIRONMENTAL

RECORD OF TITLE
UNDER LAND TRANSFER ACT 2017
FREEHOLD
Search Copy

R.W. Muir
Registrar-General
of Land

Identifier **NA31C/965**
Land Registration District **North Auckland**
Date Issued 02 September 1975

Prior References
NA1111/288

Estate	Fee Simple
Area	21.6507 hectares more or less
Legal Description	Allotment 54A Parish of Puhoi


Registered Owners
Raymond Charles Nicklin as to a 1/2 share
Desma Elizabeth Nicklin as to a 1/2 share

Interests

Subject to Section 59 Land Act 1948

C269124.5 Mortgage to Bank of New Zealand - 28.5.1991 at 9.40 am

6170820.4 Covenant pursuant to Section 108(2)(d) Resource Management Act 1991 - 5.10.2004 at 9:00 am (Also affects CsT NA137A/506, NA2100/21, NA105B/748 and NA757/204)

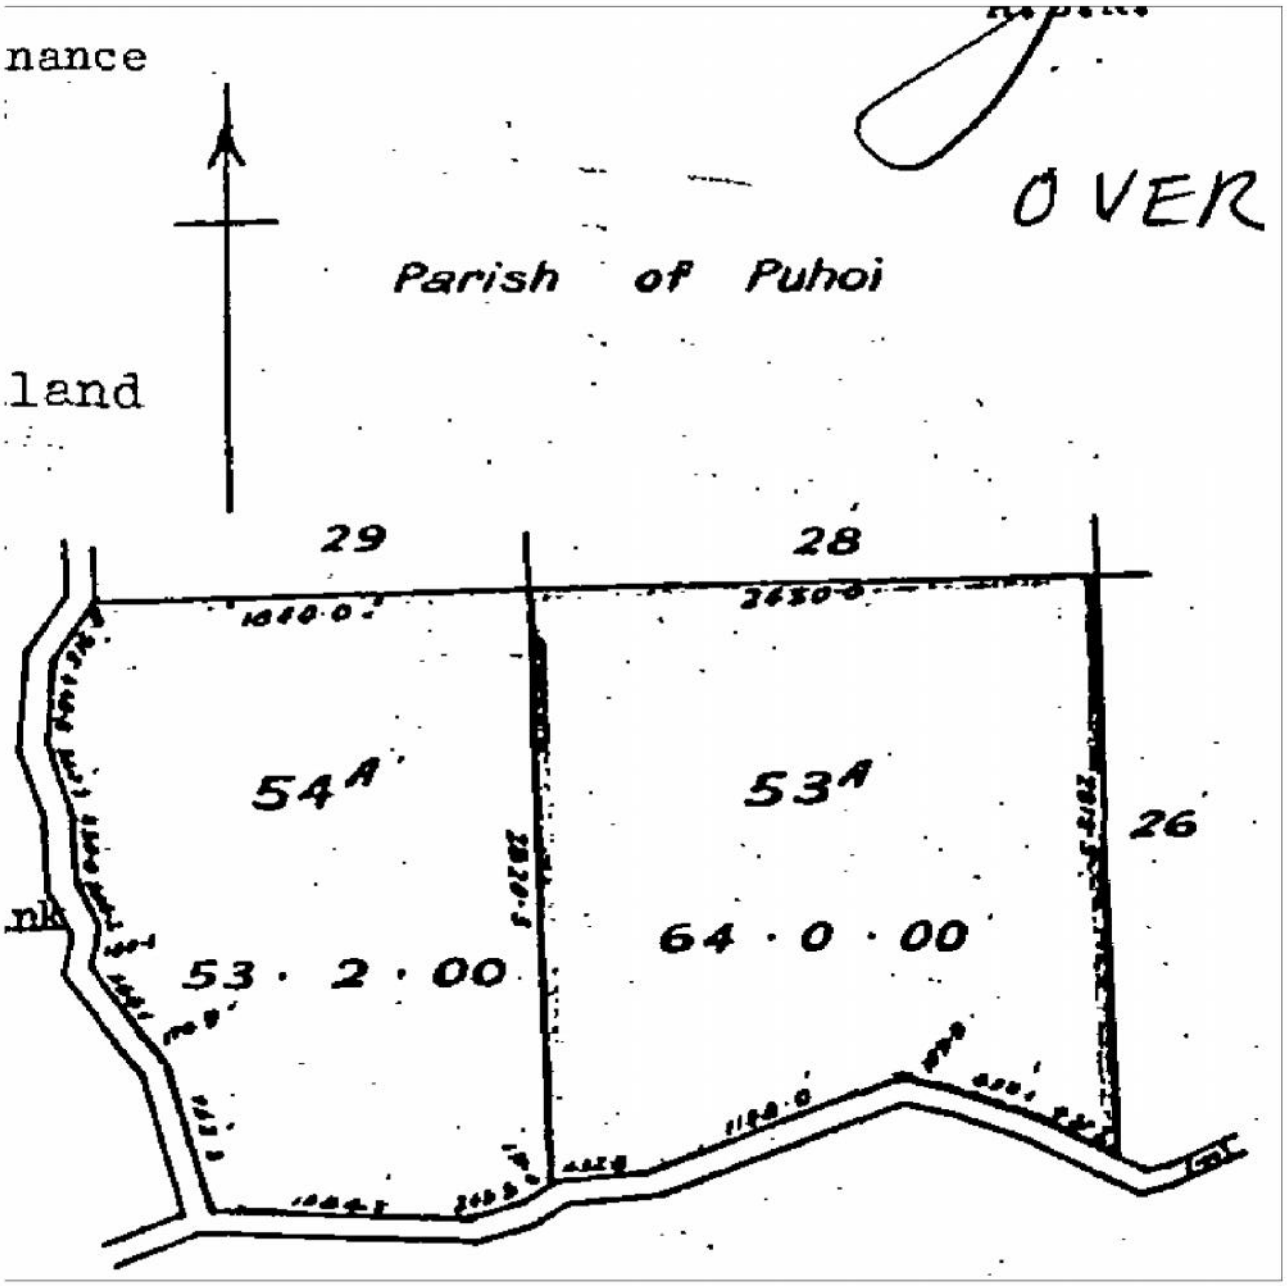
nance
OVER
Parish of Puhoi
land
29
28
54A
53A
26
53 · 2 · 00
64 · 0 · 00

RECORD OF TITLE
UNDER LAND TRANSFER ACT 2017
FREEHOLD
Limited as to Parcels
Search Copy

R.W. Muir
Registrar-General
of Land

Identifier **NA757/204**
Land Registration District **North Auckland**
Date Issued 21 September 1939

Prior References
DI 8B.692


Estate	Fee Simple
Area	37.0692 hectares more or less
Legal Description	Part Allotment 36 Parish of Puhoi

Registered Owners
Raymond Charles Nicklin as to a 1/2 share
Desma Elizabeth Nicklin as to a 1/2 share

Interests

797043A.2 Mortgage to Bank of New Zealand - 14.8.1981 at 9.47 am

6170820.4 Covenant pursuant to Section 108(2)(d) Resource Management Act 1991 - 5.10.2004 at 9:00 am (Also affects CsT NA137A/506, NA2100/21, NA31C/965 and NA105B/748)

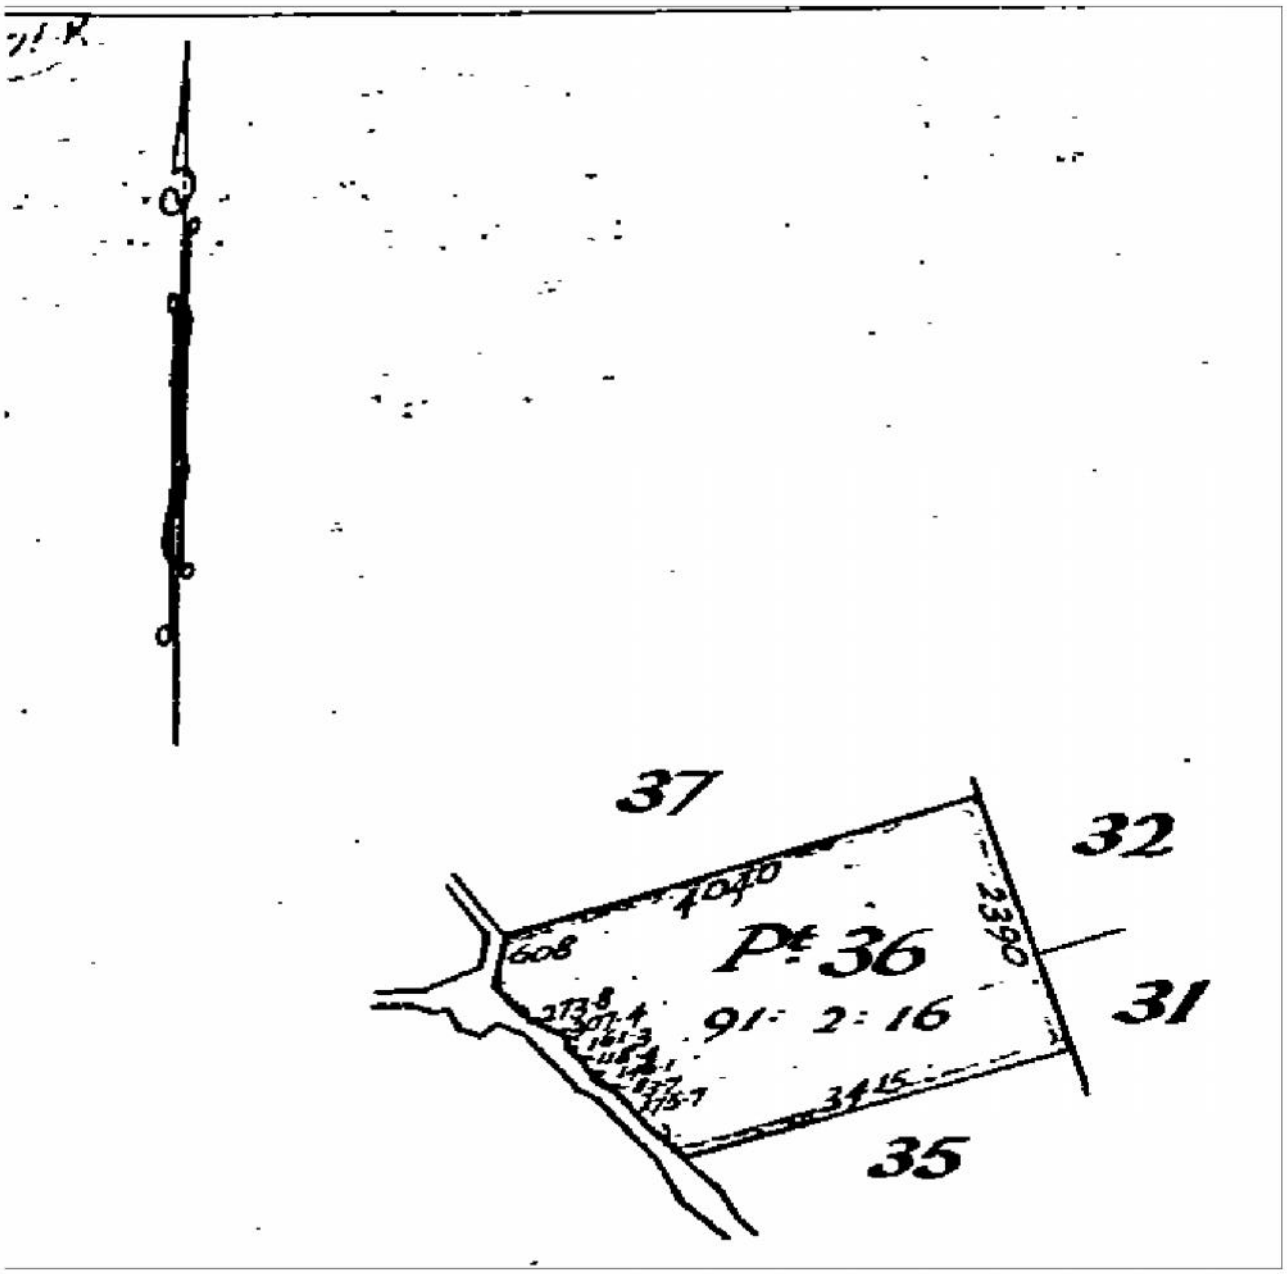
37
32
1040
2390
608
Pt 36
91: 2: 16
31
3415
35

RECORD OF TITLE
UNDER LAND TRANSFER ACT 2017
FREEHOLD
Search Copy

R.W. Muir
Registrar-General
of Land

Identifier **NA105B/748**
Land Registration District **North Auckland**
Date Issued 19 December 1996

Prior References
NA31C/964

Estate	Fee Simple
Area	24.1140 hectares more or less
Legal Description	Lot 1 Deposited Plan 179794

Registered Owners
Raymond Charles Nicklin and Desma Elizabeth Nicklin


Interests

Subject to Section 59 Land Act 1948

C269124.5 Mortgage to Bank of New Zealand - 28.5.1991 at 9.40 am

6170820.4 Covenant pursuant to Section 108(2)(d) Resource Management Act 1991 - 5.10.2004 at 9:00 am (Also affects CsT NA137A/506, NA2100/21, NA31C/965 and NA757/204)

Identifier **NA105B/748**

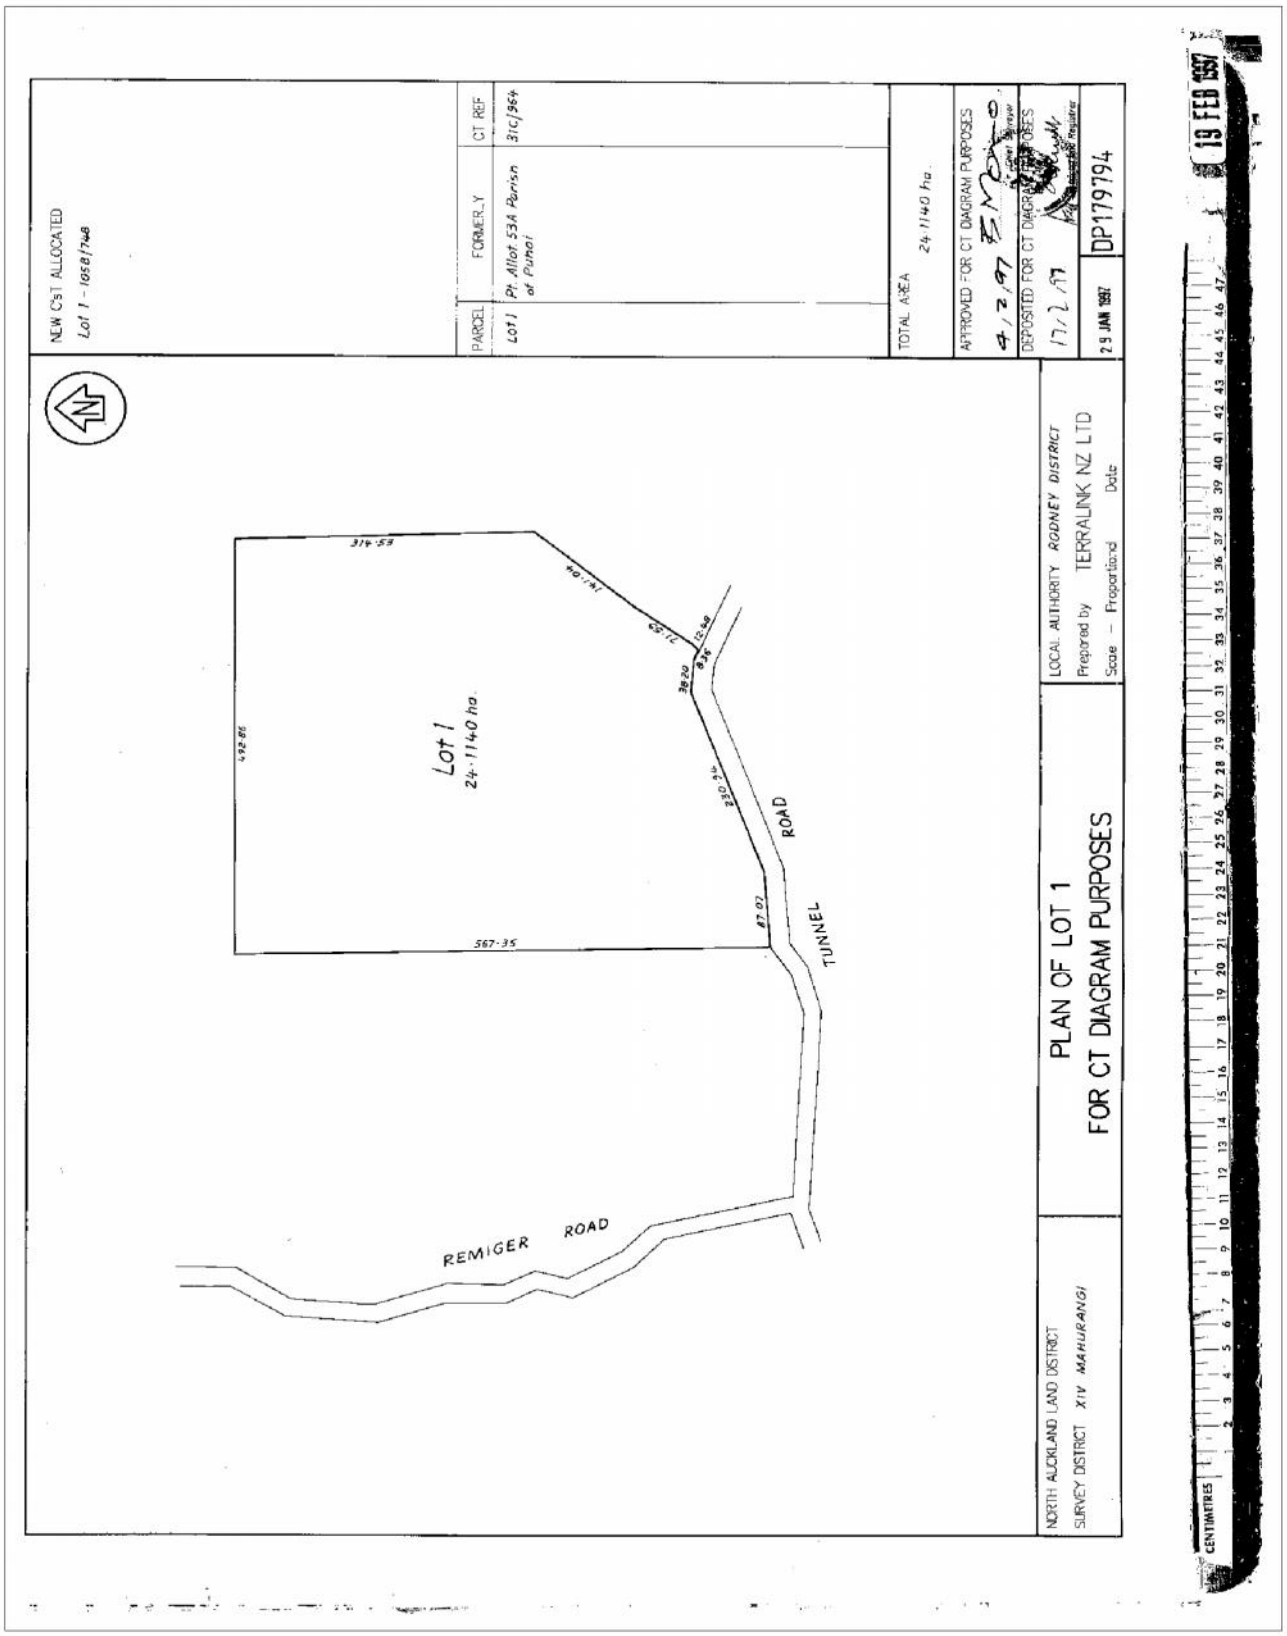

RECORD OF TITLE
UNDER LAND TRANSFER ACT 2017
FREEHOLD
Limited as to Parcels
Search Copy

R.W. Muir
Registrar-General
of Land

Identifier **NA137A/506**
Land Registration District **North Auckland**
Date Issued 05 October 2004

Prior References
NA127B/902 NA2100/21

Estate	Fee Simple
Area	57.4262 hectares more or less
Legal Description	Lot 8 Deposited Plan 208981

Registered Owners
Raymond Charles Nicklin as to a 1/2 share
Desma Elizabeth Nicklin as to a 1/2 share

Interests

C269124.5 Mortgage to Bank of New Zealand - 28.5.1991 at 9.40 am

Subject to an electricity right (in gross) over parts marked C, L, M and S on DP 208981 in favour of (now) Vector Limited created by Transfer C640690.1 - 15.8.1994 at 9.17 am

Subject to a right of way over parts marked B, C and D and to telecommunications rights over parts marked B, C, D, M, O, P and Q and to an electricity right over parts marked Q and R on DP 208981 specified in Easement Certificate D460766.5 - produced 9.12.1999 at 12.34 pm and entered 1.2.2000 at 9.00 am

Some of the easements specified in Easement Certificate D460766.5 are subject to Section 243 (a) Resource Management Act 1991

Appurtenant hereto are electricity rights specified in Easement Certificate D460766.5 - produced 9.12.1999 at 12.34 pm and entered 1.2.2000 at 9.00 am

Subject to a right of way and to a telecommunications right over parts marked B, C and D on DP 208981 specified in Easement Certificate D611644.6 - produced 11.6.2001 at 9.00 am and entered 2.7.2001 at 9.00 am

6170820.4 Covenant pursuant to Section 108(2)(d) Resource Management Act 1991 - 5.10.2004 at 9:00 am (Also affects CsT NA2100/21, NA31C/965, NA105B/748 and NA757/204)


Subject to a right to transmit an electricity easement over parts marked R, U and V on DP 208981 and a right to transmit telecommunications over parts marked O, M, P, U and V on DP 208981 created by Easement Instrument 6170820.9 - 5.10.2004 at 9:00 am

Appurtenant hereto are right to convey water & electricity easements created by Easement Instrument 8505466.1 - 28.5.2010 at 1:07 pm


9236051.3 Surrender of the electricity right parts marked L, M and S on DP 208981 created by Transfer C640690.1 - 16.11.2012 at 12:04 pm

Subject to a right (in gross) to convey electricity over parts marked D, E and F on DP 451839 in favour of Vector Limited created by Easement Instrument 9236051.4 - 16.11.2012 at 12:04 pm

Identifier **NA137A/506**

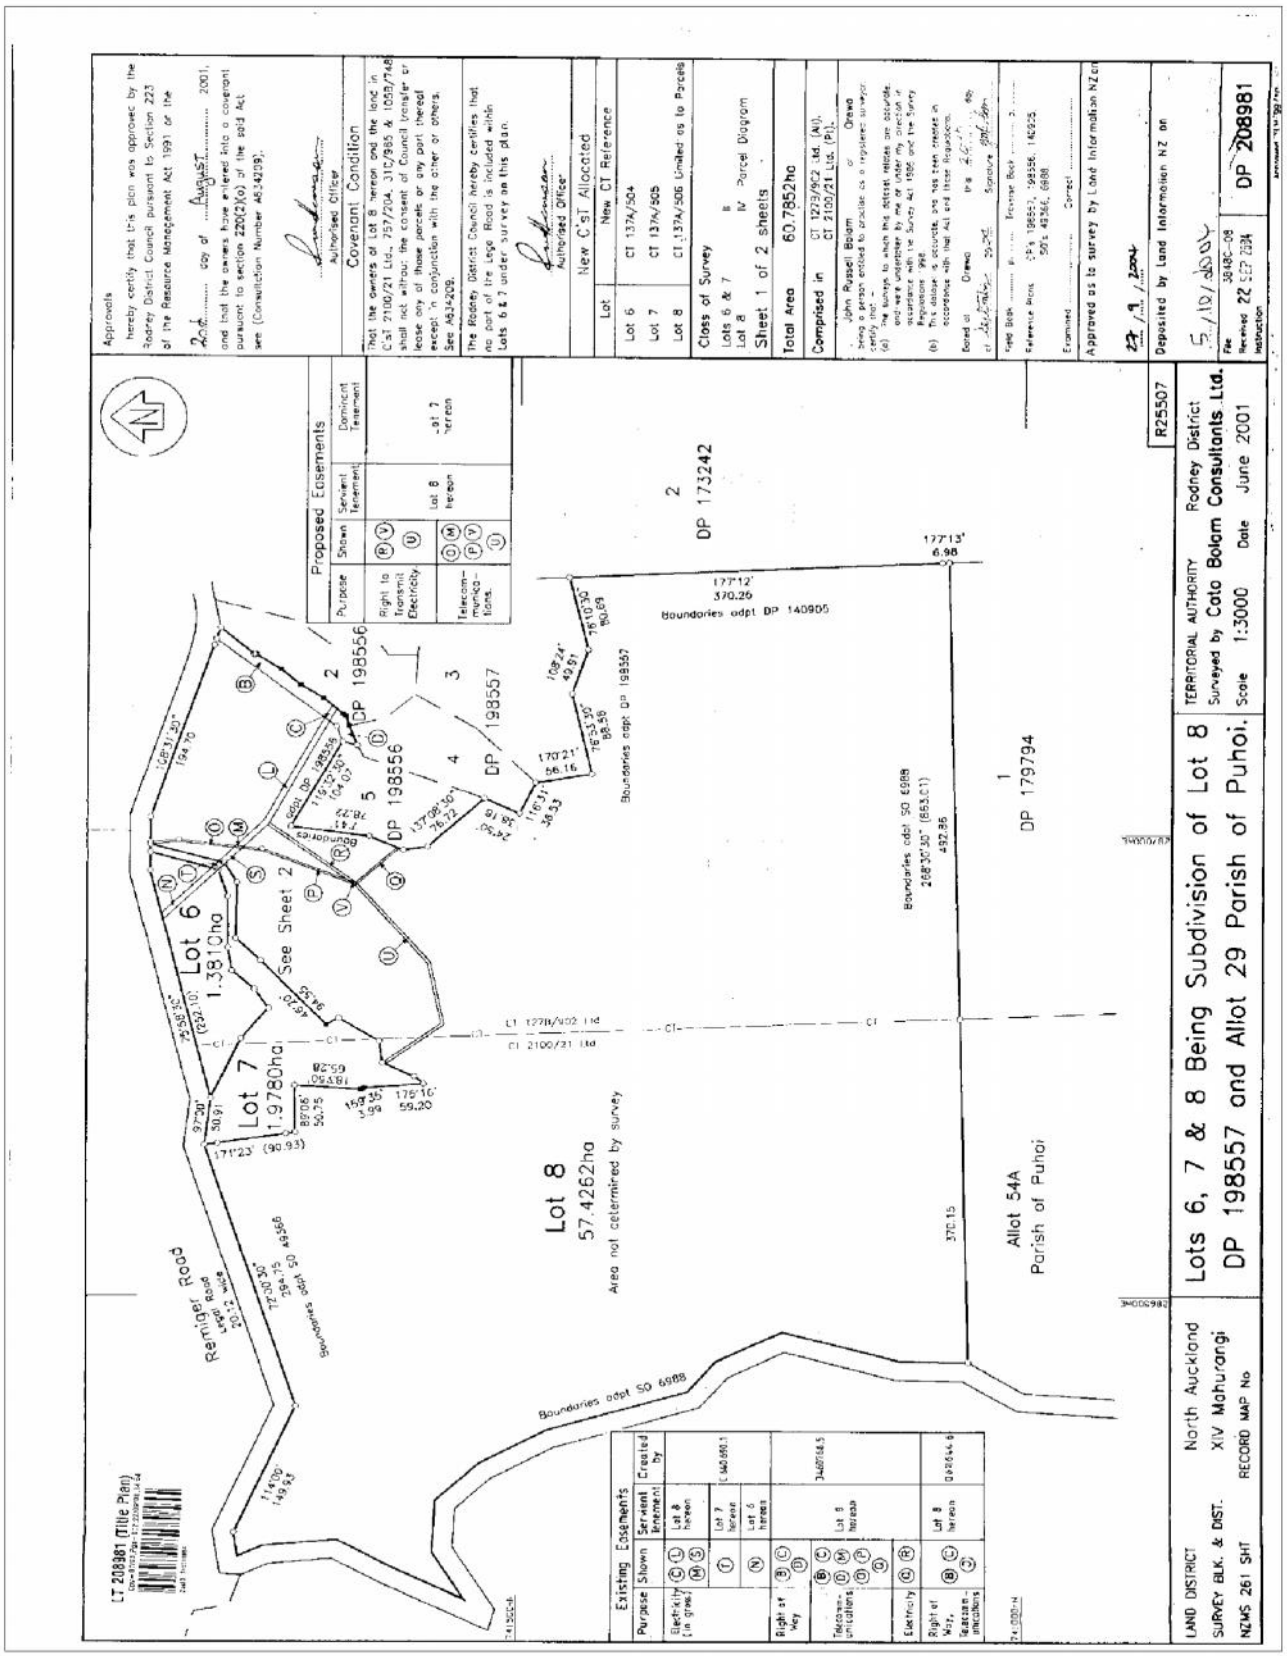

Identifier **NA137A/506**

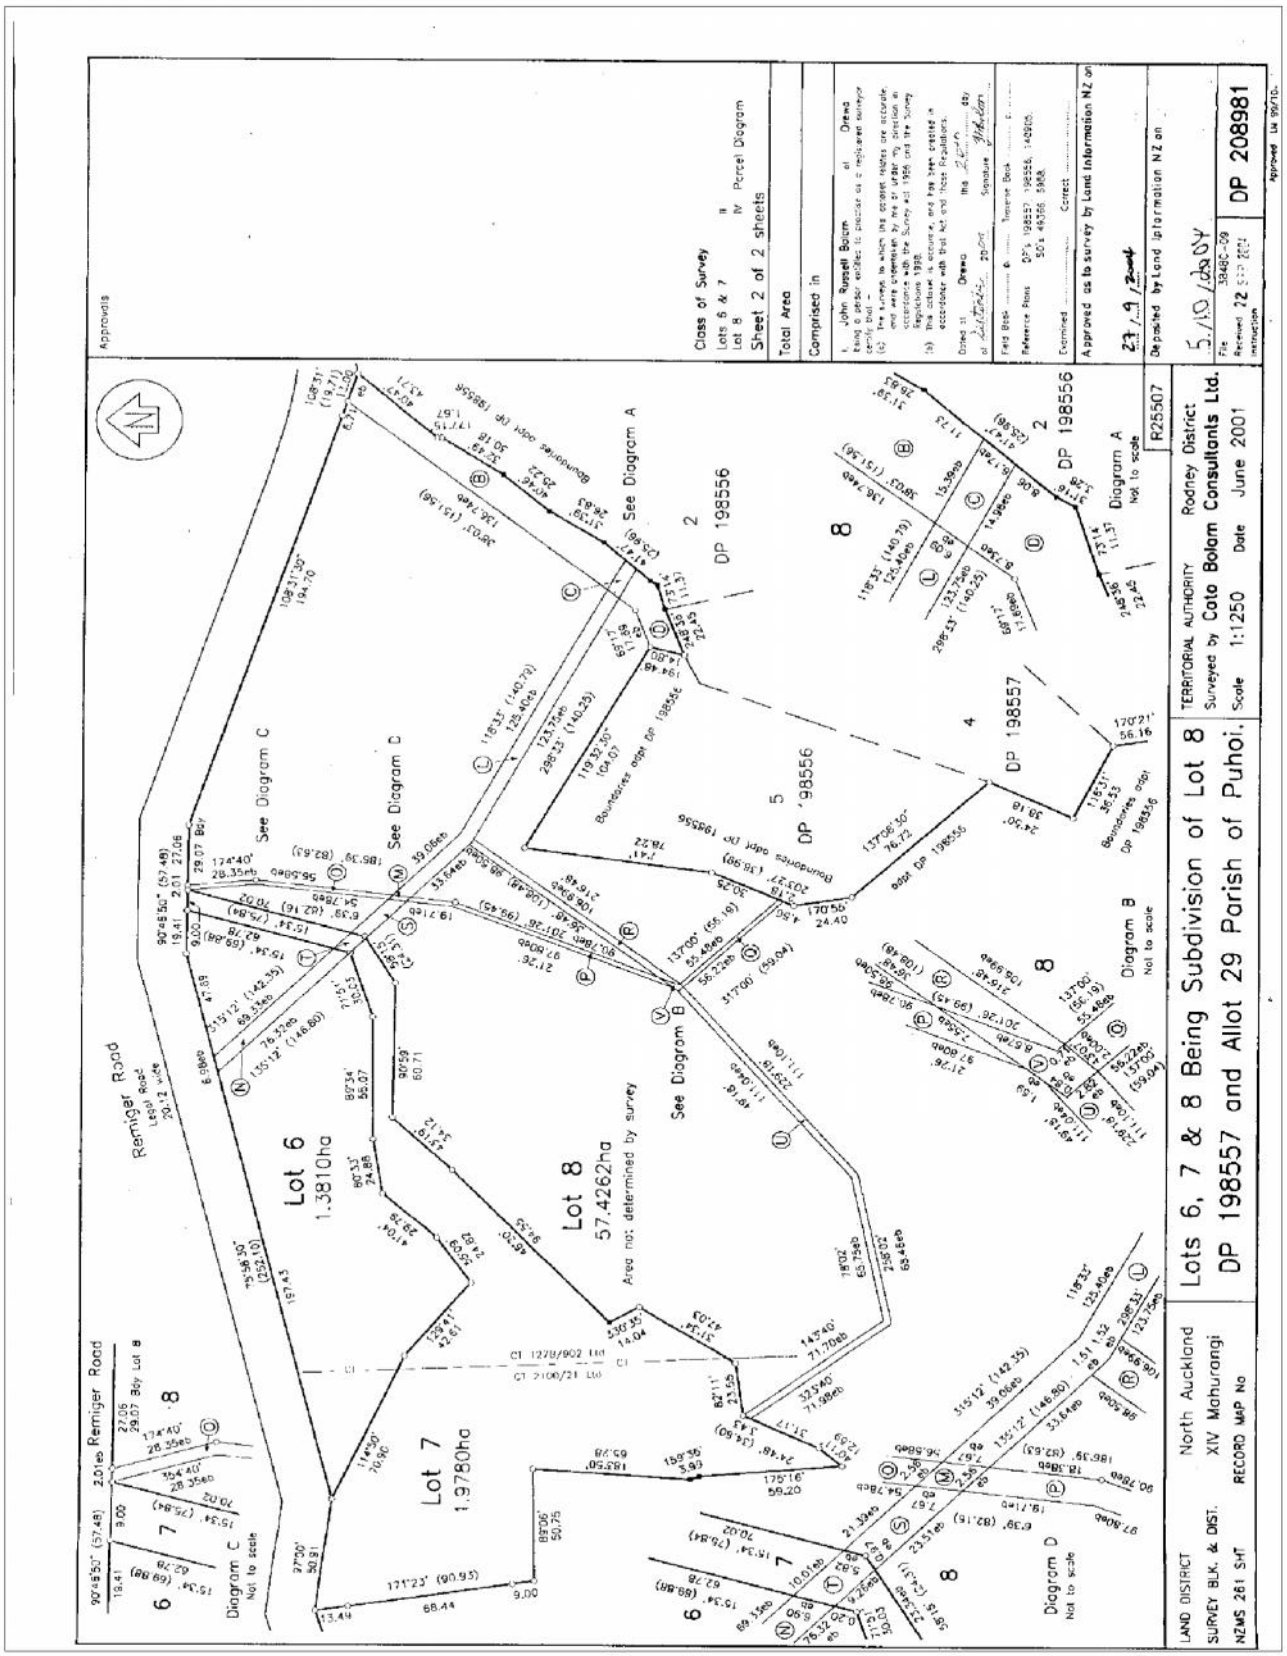

RECORD OF TITLE
UNDER LAND TRANSFER ACT 2017
FREEHOLD
Search Copy

R.W. Muir
Registrar-General
of Land

Identifier **NA127B/898**
Land Registration District **North Auckland**
Date Issued 01 February 2000

Prior References
NA2036/1 NA2100/21

Estate Fee Simple
Area 1.1705 hectares more or less
Legal Description Lot 5 Deposited Plan 198556

Registered Owners
Christopher Charles Nicklin and Kathryn Ann Nicklin


Interests


Appurtenant hereto is a right of way and telecommunications and electricity rights specified in Easement Certificate D460766.5 - produced 9.12.1999 at 12.34 pm and entered 1.2.2000 at 9.00 am

Some of the easements specified in Easement Certificate D460766.5 are subject to Section 243 (a) Resource Management Act 1991 (see DP 198556)

6231198.4 Mortgage to Bank of New Zealand - 29.11.2004 at 9:00 am

Identifier **NA127B/898**

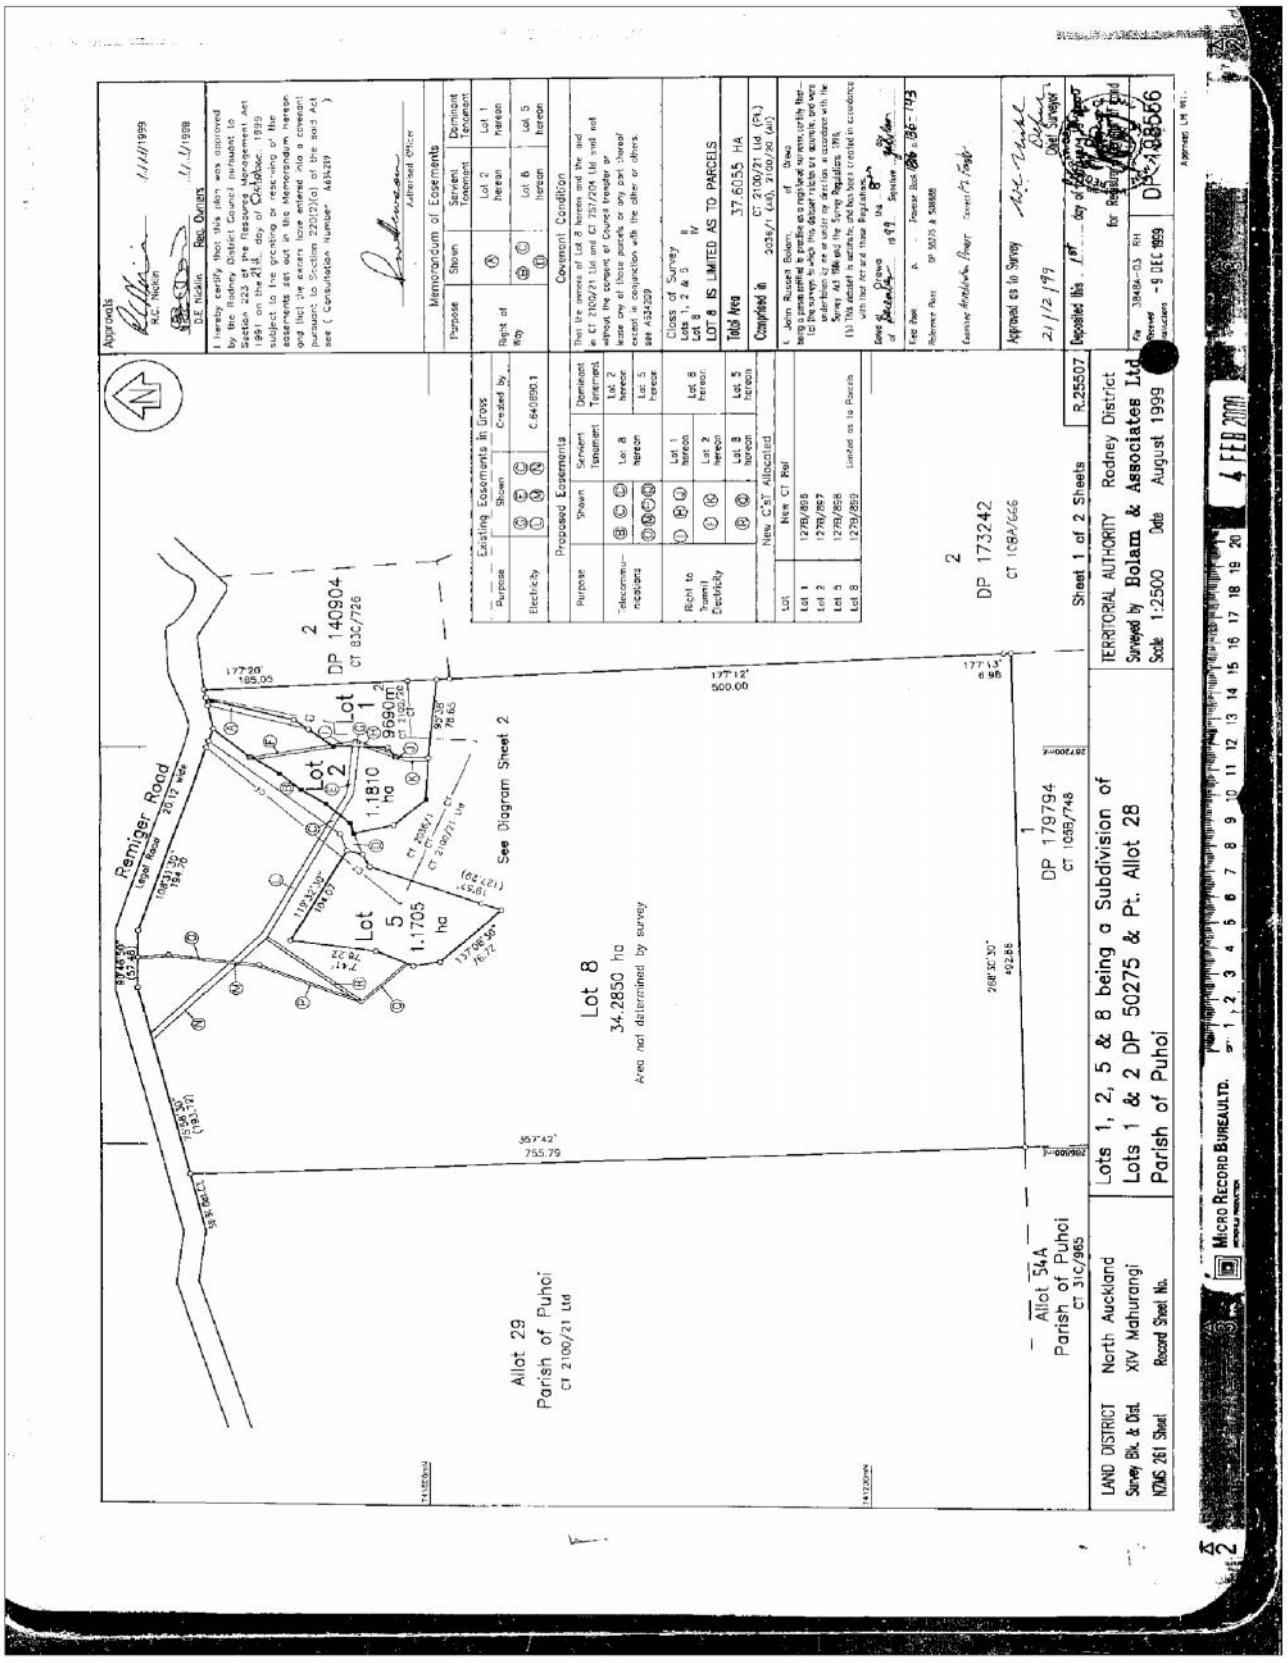

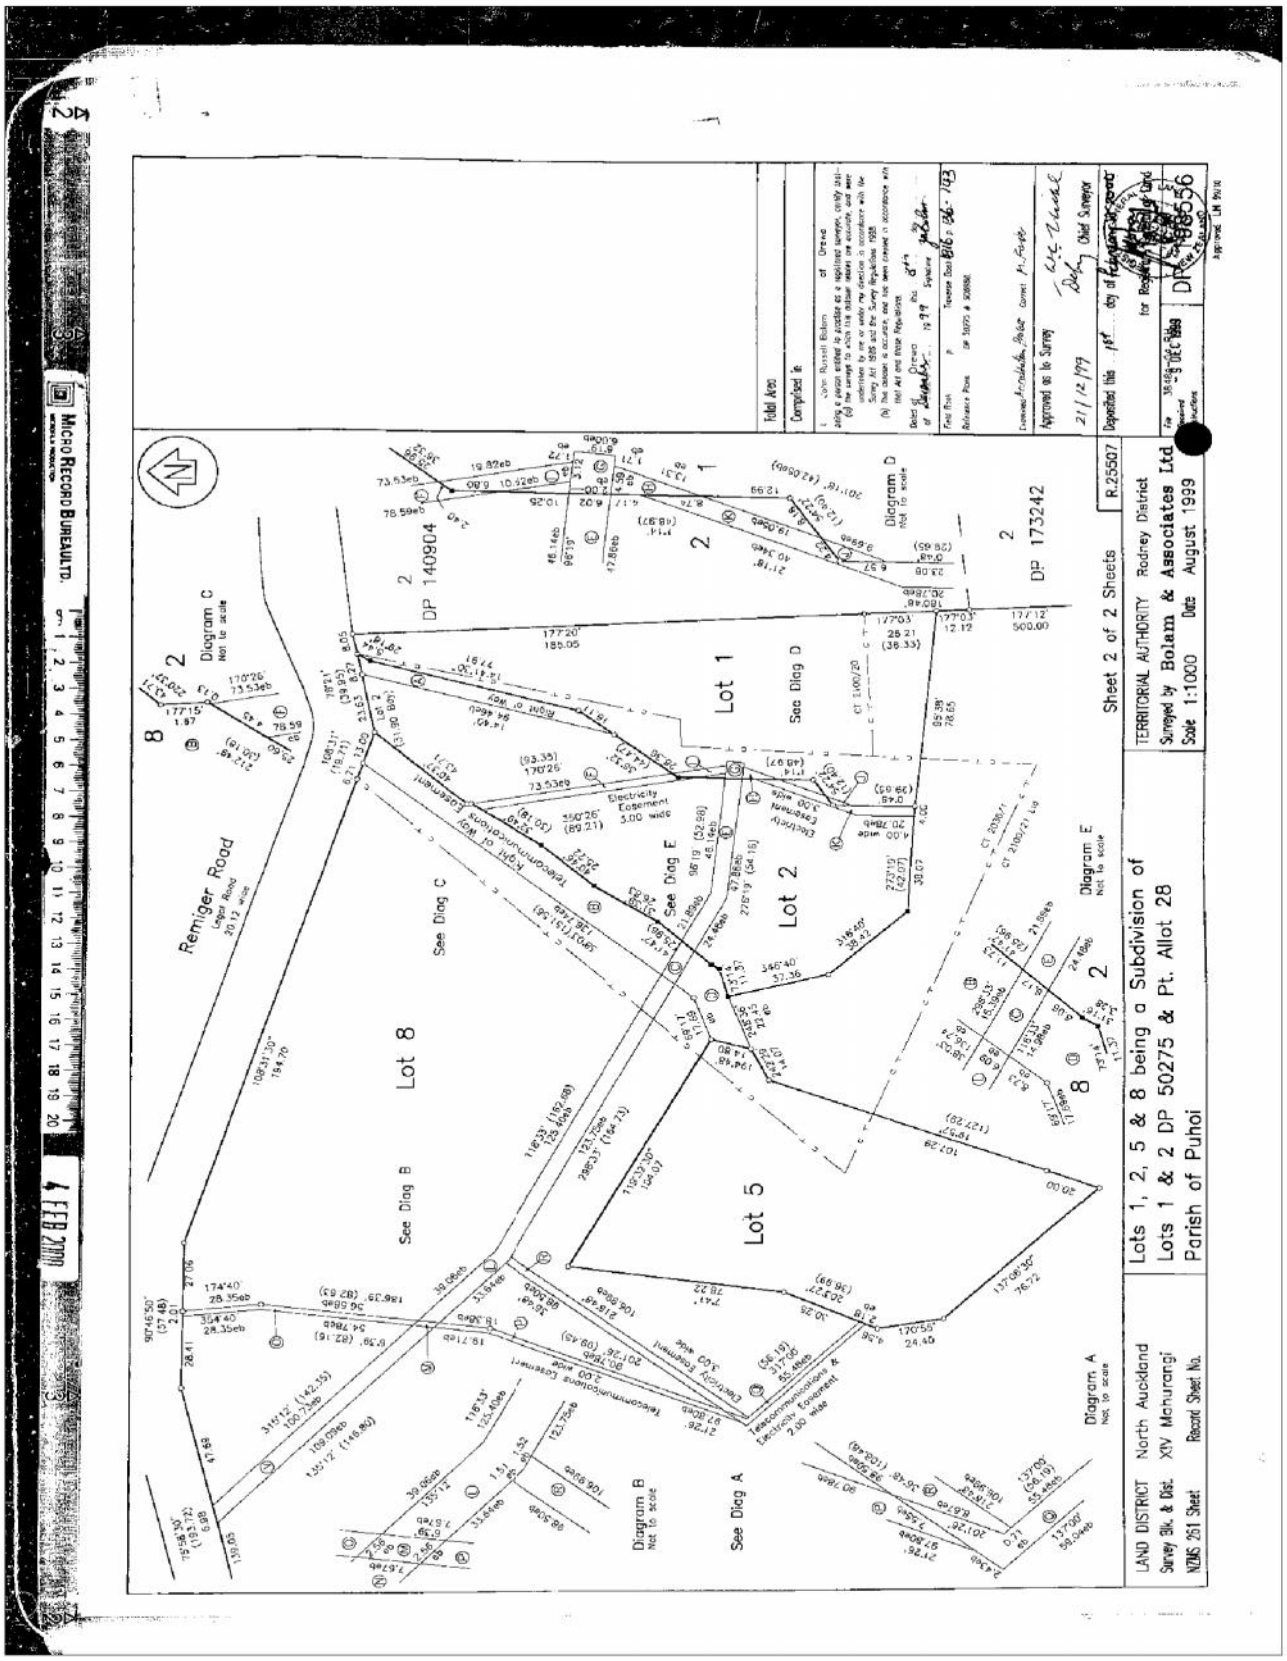
Lots 1, 2, 5 & 8 being a Subdivision of
Lots 1 & 2 DP 50275 & Pt. Allot 28
Parish of Puhoi
TERRITORIAL AUTHORITY Rodney District
Surveyed by Bolam & Associates Ltd
Scale 1:1000 Date August 1999
Sheet 2 of 2 Sheets
R.25507
LAND DISTRICT North Auckland
Survey Dist. & Dist. XIV Mahurangi
NOMS 251 Sheet Record Sheet No.
Remiger Road
Lot 1
Lot 2
Lot 5
Lot 8
DP 140904
DP 173242
Diagram A
Diagram B
Diagram C
Diagram D
Diagram E
Electricity Easement 3.00 wide
Telecommunications & Electricity Easement 2.00 wide
Telecommunications Easement 3.00 wide
Electricity Easement 3.00 wide
Telecommunications Easement 5.00 wide
Right of Way 9.45 wide
DP 385556

RECORD OF TITLE
UNDER LAND TRANSFER ACT 2017
FREEHOLD
Limited as to Parcels
Search Copy

R.W. Muir
Registrar-General
of Land

Identifier **NA2100/21**
Land Registration District **North Auckland**
Date Issued 05 November 1962

Part-Cancelled

Prior References
NA757/202

Estate	Fee Simple
Area	229.2180 hectares more or less
Legal Description	Allotment 29, 32, 35 Parish of Puhoi and Part Allotment 28, 30-31 Parish of Puhoi

Registered Owners
Raymond Charles Nicklin as to a 1/2 share
Desma Elizabeth Nicklin as to a 1/2 share

Interests

C269124.5 Mortgage to Bank of New Zealand - 28.5.1991 at 9.40 am

Subject to an electricity right (in gross) over part marked B on DP 159737 in favour of (now) Vector Limited created by Transfer C640690.1 - 15.8.1994 at 9.17 am

D460766.3 CTs NA127B/896, NA127B/898-899 issued for part Lots 1, 5, and 8 DP 198556 -produced 9.12.1999 at 12:34 pm and entered 1.2.2000 at 9:00 am

6170820.1 Certificate pursuant to Section 223 Resource Management Act 1991(affects DP 208981) - 5.10.2004 at 9:00 am

6170820.2 Certificate pursuant to Section 224(c) Resource Management Act 1991 (affects DP 208981 - 5.10.2004 at 9:00 am

6170820.3 Consent Notice pursuant to Section 221 Resource Management Act 1991 - 5.10.2004 at 9:00 am (affects Lot 6 DP 208981)

6170820.4 Covenant pursuant to Section 108(2)(d) Resource Management Act 1991 - 5.10.2004 at 9:00 am (Also affects CsT NA137A/506, NA31C/965, NA105B/748 and NA757/204)

6170820.8 CTs issued - 5.10.2004 at 9:00 am

Legal Description	Title
Lot 6 Deposited Plan 208981	NA137A/504
Lot 7 Deposited Plan 208981	NA137A/505
Lot 8 Deposited Plan 208981	NA137A/506

Identifier **NA2100/21**

